


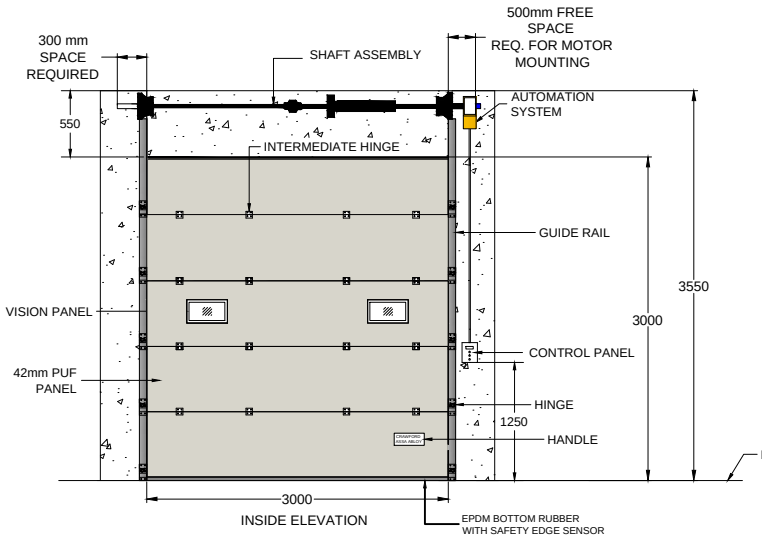


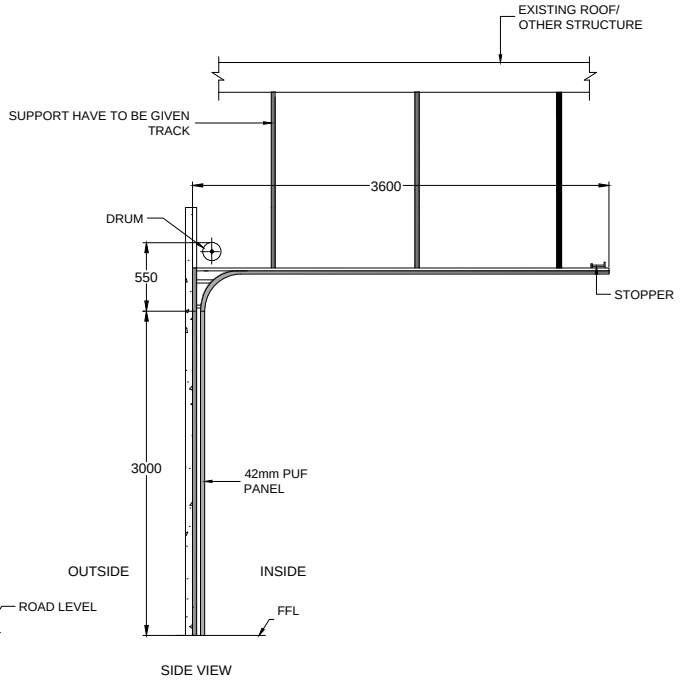

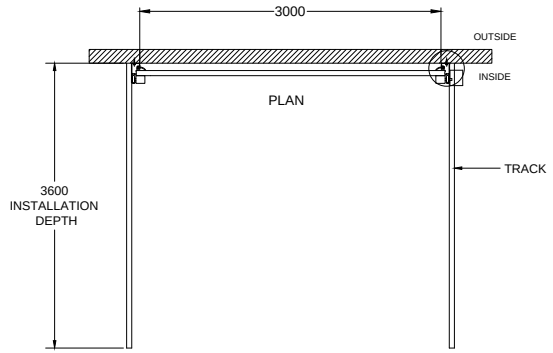

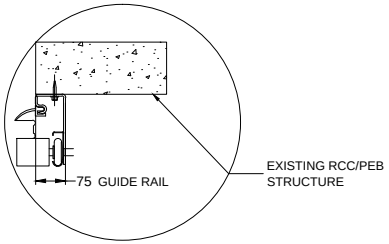

TRACK DETAILS

REV:-1.CHANGED QTY.

DIMENSION :

CLEAR WIDTH	CLEAR HEIGHT	QUANTITY
3000 mm	3000 mm	3

TECHNICAL DATA :

COMPONENTS	MATERIALS	SPECIFICATIONS
DOOR PANELS	GI & PUF	42mm CFC- FREE POLYURETHANE WITH 0.5mm THK, GI PRECOATED PANELS.
DOOR HINGE	——	HEAVY DUTY HINGES FOR INTERLOCKING OF PANELS
SHAFT ASSEMBLY	STD.	TORSIONAL SPRING WITH SHAFT & BEARING PLATES
FINISH		PANELS WILL BE COLORED IN STANDARD

ACCESSORIES-
1. SAFETY EDGE SENSOR. 2. FLASHING LIGHT BOTH SIDE

IMPORTANT NOTES:

1. REQUIRED STRUCTURE FOR DOOR SHALL BE IN CLIENT'S SCOPE.
2.SINGLE PHASE POWER SUPPLY REQUIRED AT DOOR LOCATION.
3.ALL CIVIL WORK SHALL BE CLIENT'S SCOPE.

NIHVA TECHNOLOGIES PVT. LTD.
NIHVA TECHNOLOGIES PVT. LTD. PUNE
Email:- info@nihva.com
Website:- www.nihva.com

TITLE:

SECTIONAL DOOR SL (MOTORIZED)

CLIENT'S APPROVAL :

CLIENT -DEV TECHNO SKILLS

PROJECT - AMAR TEA

SITE LOCATION - UMARGAON, GUJARAT

DWG. NO. : NIHVA/17-18/0353/R01 | REV- 01

SCALE: NTS | WT: | SHEET:1 OF 1

	NAME	DATE	SIGN.
DRAWN	SURAJ	07-03-2018	
CHECK	OMKAR	07-03-2018	
APPROVAL	SHEKHAR	07-03-2018	

If any queries contact : design@nihva.com

NOTE: ALL DIMENSIONS ARE IN mm

THIS DRAWING & DESIGNING IS THE PROPERTY OF NIHVA TECHNOLOGIES. NOT TO BE SOLD OR COPIED TO ANY OTHER CONCERN.