


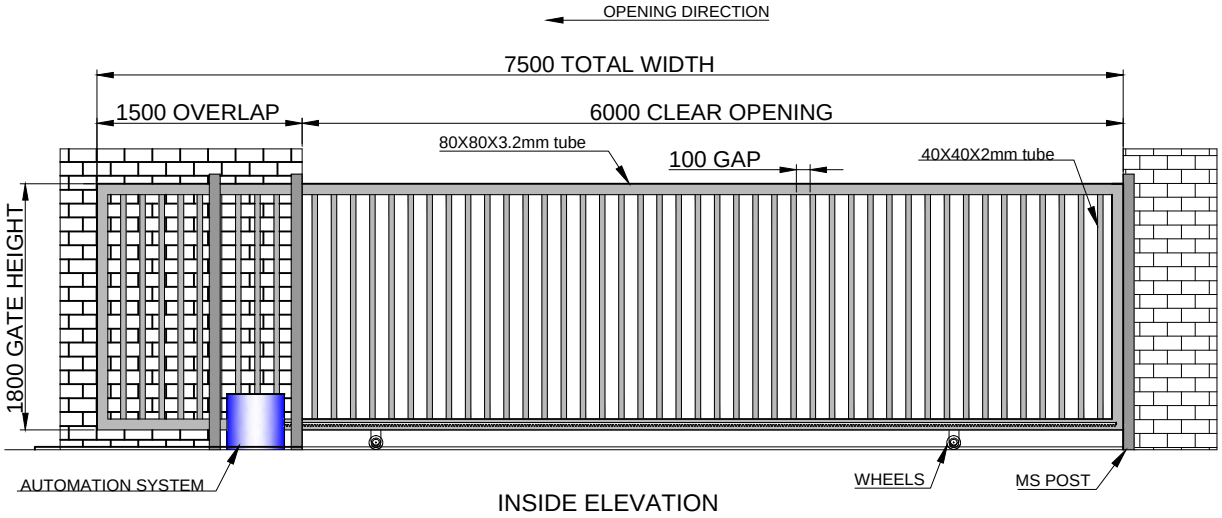



INSIDE ELEVATION

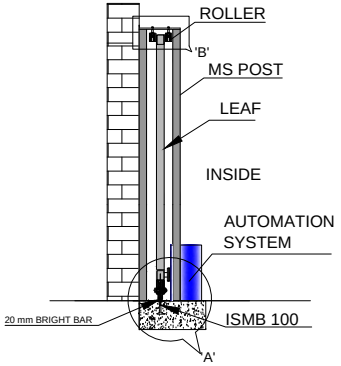

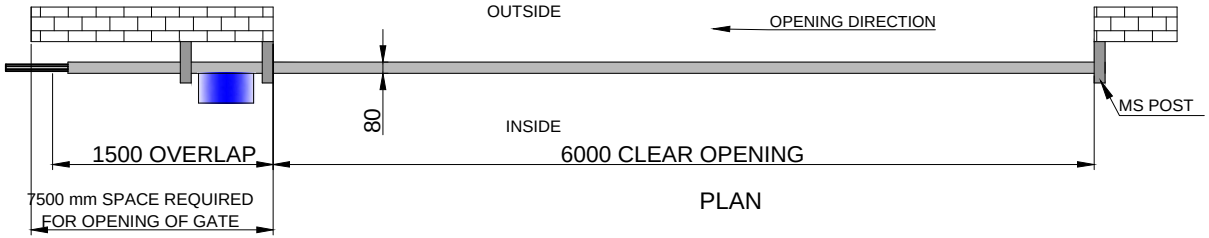

PLAN

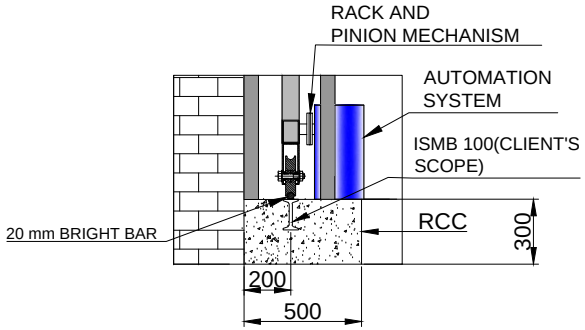

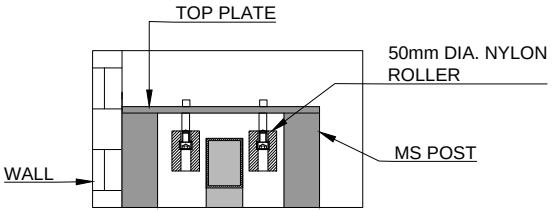

DETAIL VIEW OF B

REVISION 1- GATE SIZE REVISED.

DETAIL VIEW OF A

NOTE-
1. ALL REQUIRED CIVIL WORK WILL BE IN CLIENTS SCOPE.
2. ONE COAT OF RED OXIDE & TWO COAT OF APPROVED RAL SHADE WILL BE GIVEN TO THE GATE.
3.GATE LEAF WILL BE IN TWO PARTS FOR TRANSPORTATION & WILL BE WELD TOGETHER ON SITE.

SR NO	TUBE SPECIFICATION	
1	80X80X3.2mm	OUTER FRAME
2	40X40X2mm	INNER PATTERN
3	80X80X3.2mm	FOR MS POST

TOTAL NO OF POST ARE 4.

TOLERANCE- ±10mm

CLEAR WIDTH	CLEAR HEIGHT	QUANTITY	GATE NO
6000mm	1800mm	1 NOS	GATE NO 6

This drawing & designing is the property of NIHVA TECHNOLOGIES. Not to be sold or copied to any other concern.

TITLE: AUTOMATIC SINGLE LEAF SLIDING GATE NO 6

NIHVA TECHNOLOGIES PVT. LTD.
NIHVA TECHNOLOGIES PVT. LTD. PUNE
Tel : 020 66304033
Email:- info@nihva.com
Website:- www.nihva.com

	SIGN	DATE
DRAWN	SURAJ	17/05/17
CHECK	SAGAR P.	17/05/17
REV.		
APPROVAL	S.S	17/05/17

If any queries contact : projects@nihva.com

ALL DIMENSION ARE IN mm

CLIENT - TATA PROJECTS LIMITED
PROJECT - ALSTOM
SITE LOCATION -MADHEPURA,BIHAR
DWG. NO. : NIHVA/17-18/0080/R01
SCALE: NTS | WT: | SHEET: 01 OF 01