

Weitergabe sowie Vervielfältigung dieses Dokuments, Verwertung und Mitteilung seines Inhalts sind verboten, soweit nicht ausdrücklich gestattet. Zuwiderhandlungen verpflichten zu Schadenersatz. Alle Rechte für den Fall der Patent-, Gebrauchsmuster- oder Geschmacksmustereintragung vorbehalten.

This reproduction, distribution and utilization of this document as well as the communication of its contents to others without explicit authorization is prohibited. Offenders will be held liable for the payment of damages. All rights reserved in the event of the grant of a patent, utility model or design.

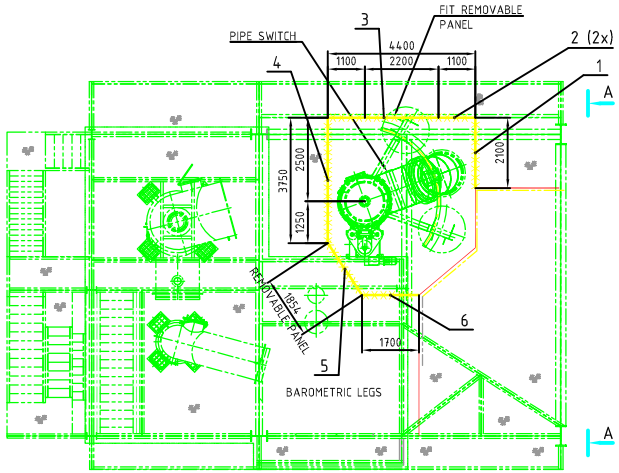


PLAN ON +9.800m LEVEL
PIPE SWITCH IN RH1
TREATMENT POSITION

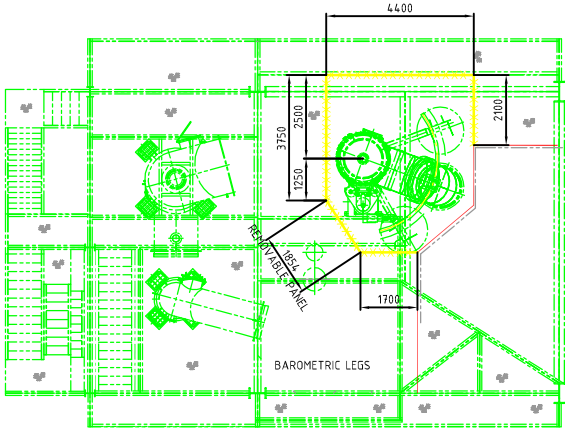


PLAN ON +9.800m LEVEL
PIPE SWITCH IN RH2
TREATMENT POSITION

ITEM NO.	DESCRIPTION	QTY.
1	MESH FENCE – 2100 x 2 Mtr. HEIGHT	1
2	MESH FENCE – 1100 x 2 Mtr. HEIGHT	2
3	MESH FENCE – 2200 x 2 Mtr. HEIGHT	2
4	MESH FENCE – 3750 x 2 Mtr. HEIGHT	1
5	MESH FENCE – 1854 x 2 Mtr. HEIGHT REMOVABLE PANEL	1
6	MESH FENCE – 1700 x 2 Mtr. HEIGHT	1
7	MESH FENCE – 550 x 2 Mtr. HEIGHT	1
8	LOCKABLE GATE – W=650 x 2 Mtr. HEIGHT	1
9	MESH FENCE – 800 x 2 Mtr. HEIGHT	1

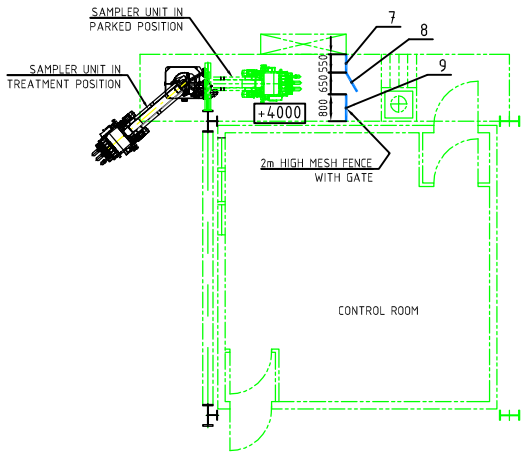

PLAN ON +4.000m LEVEL CONTROL
ROOM PULPIT

A-A

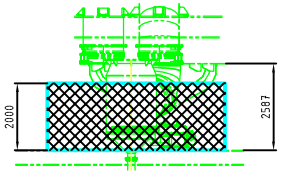

SAFETY FENCE AROUND PIPE
SWITCH FOR MAINTENANCE
PANELS SEE PLANS ON +9800
m LEVEL.

-STATUS AS ON DATE = 16.01.2015

NOTES
1. EDGES OF ALL PLATFORMS, WALKWAYS ETC. TO BE FITTED WITH STANDARD HANDRAILING UNLESS OTHERWISE NOTED.
2. ALL INTERLOCKED GATES TO BE 2m HIGH.
3. ALL REMOVABLE ACCESS PANELS TO BE REMOVED USING STANDARD TOOLS.
4. FOR LEGEND REFER TO DRAWING NUMBER 1312R-D37-001.

REV.	DATE	ZONE	DESCRIPTION	BY	CHECKED
–	–	–	–	–	–
–	–	–	–	–	–
A	16.01.15	–	DRAWING UPDATED	RASI	RAUP

REVISIONS

BASIC ENGINEERING

TATA STEEL LIMITED
JAMSHEDPUR, JHARKHAND

DEPT. CODE
AREA CODE
SUBJECT CODE
TATA DRG. NO.: REV.

Consulting Engineers: M. N. DASTUR & COMPANY (P) LTD, KOLKATA

Projekt-Nr. / Project-No.: TATA - LD 2 S3H6

Benennung / Designation: 165t DUPLEX RH UNIT
TECHNOLOGICAL STRUCTURES
SAFETY FENCING & ACCESS GATES

SMS group

	Datum	Name
Drawn	16.12.2014	PKGA
Chkd	17.12.2014	RAUP
Resp	17.12.2014	RAUP
Dept	1131	
Tel.	1752	

Maßst. / Scale: 1:75
ISO 128 Projektionsmethode 1 / First angle projection method
Fertigungsvorschriften / Manufacturing Instructions: SN 200
Werkstoff, Material
Stückgew., Unit weight: Kg
Entst. aus: A 1312R-D37-009
Format Size: 1
Zeichnungs-Nr./Drawing-Nr.: 1312R-D03-182
Format Index: A
CAD Blatt / Sheet: 2 von / of 5

SMS Siemag - AutoCAD Vordruck V-4255-1 / 03.09