



ELEVATION

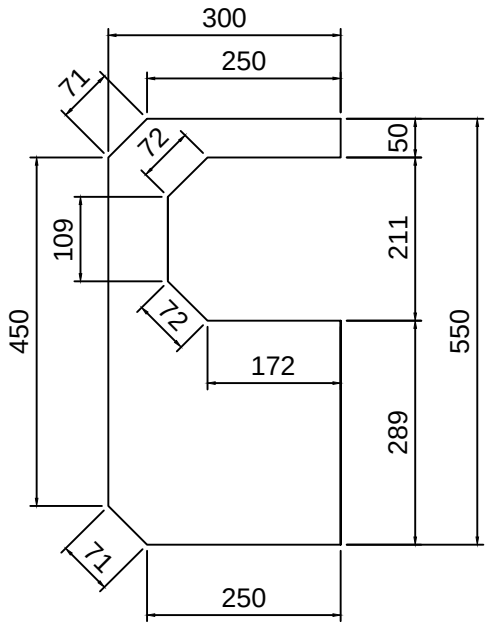

SIDE VIEW

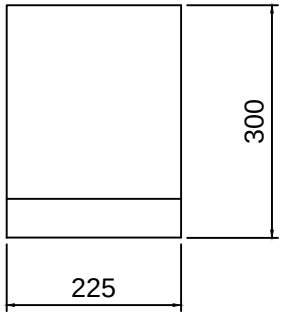

PLAN

NOTE :
1. LEFT SIDE MOTOR DOOR : 1 NO
2. RIGHT SIDE MOTOR DOOR : 10 NOS

MATERIAL:- G.I
THK:- 0.9mm

COLOR :- RAL 7035 (GREY)
POWDER COATING(GLOSSY)
QTY : 10 NOS

TOLERANCE - ±5mm

This drawing & design is the property of NIHVA TECHNOLOGIES. Not to be sold or copied to any other concern.

TITLE	MOTOR COVER LEFT SIDE			NIHVA TECHNOLOGIES PVT. LTD. PUNE Tel : 020 66304033 Email:- info@nihva.com Website:- www.nihva.com
	NAME	SIGN	DATE	
DRAWN	P.V.A		02.03.19	CLIENT -
CHECK	V.M.T		02.03.19	PROJECT -
APPRD.				SITE LOCATION -
If any queries contact : design@nihva.com				DWG. NO. : NIHVA/18-19/VDR/394
ALL DIMENSION ARE IN mm				SCALE: NTS / WT: / REV- 0