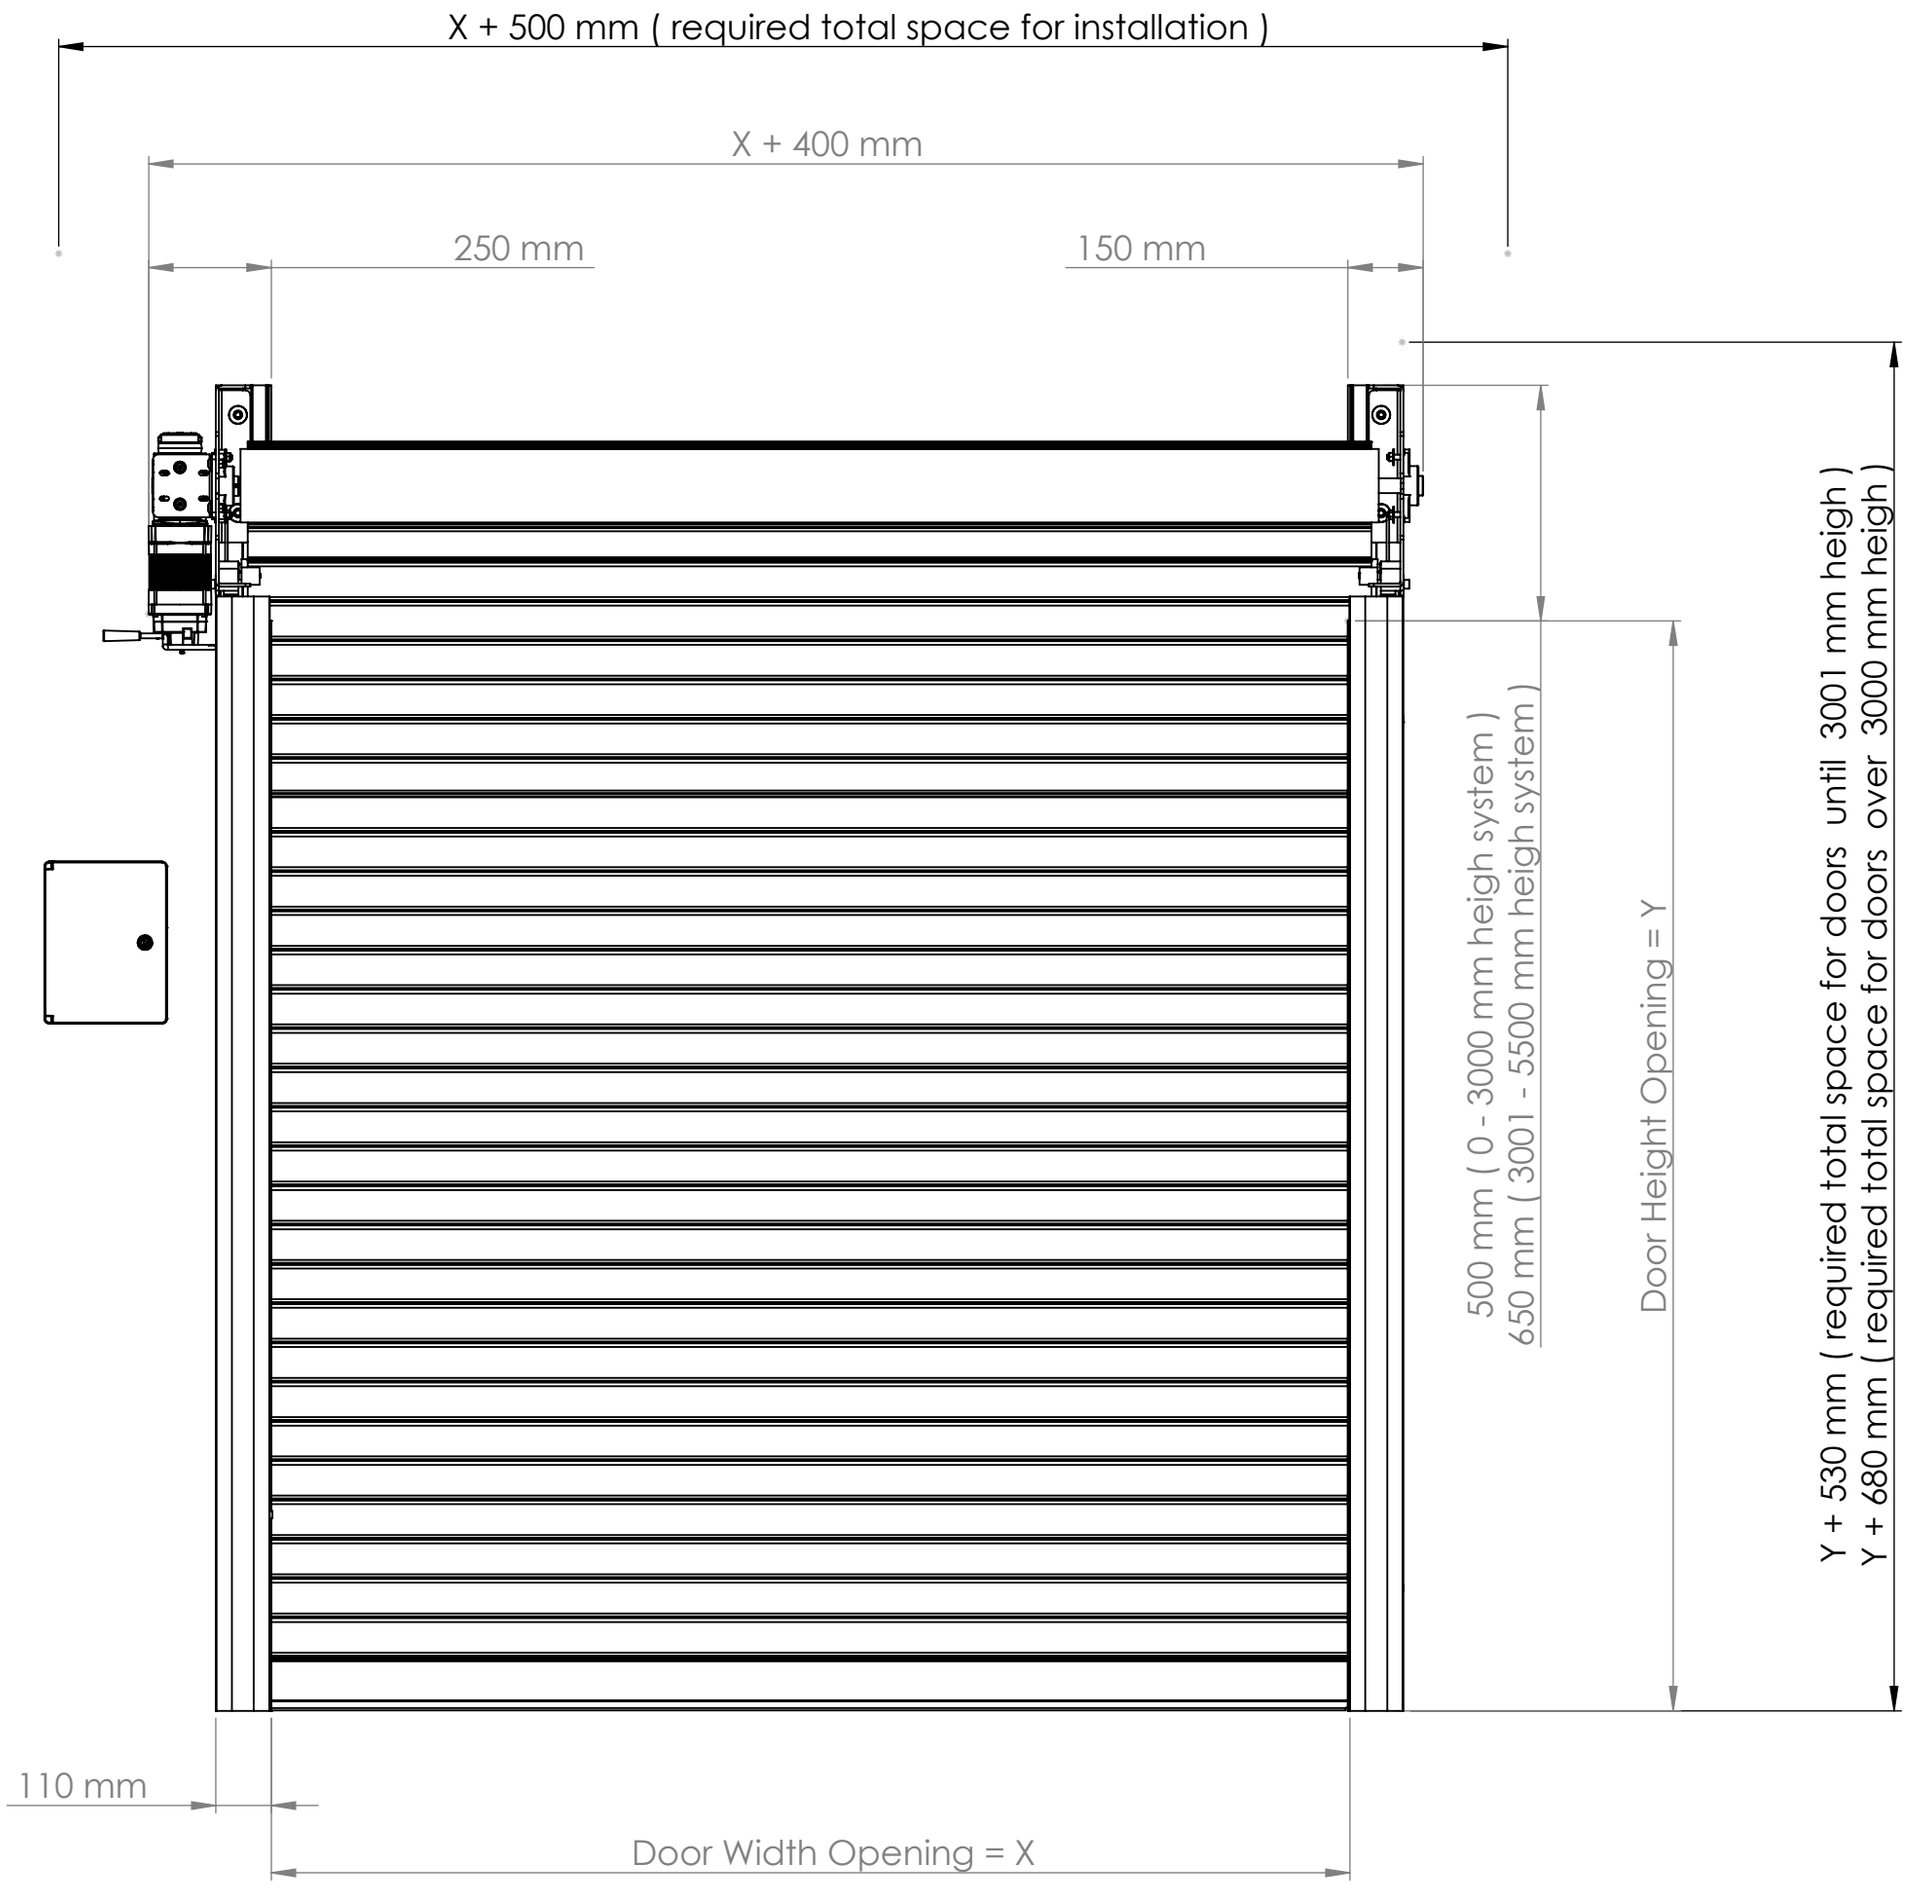

X + 500 mm (required total space for installation)
X + 400 mm
250 mm
150 mm
500 mm (0 - 3000 mm heigh system)
650 mm (3001 - 5500 mm heigh system)
Door Height Opening = Y
Y + 530 mm (required total space for doors until 3001 mm heigh)
Y + 680 mm (required total space for doors over 3000 mm heigh)
110 mm
Door Width Opening = X