
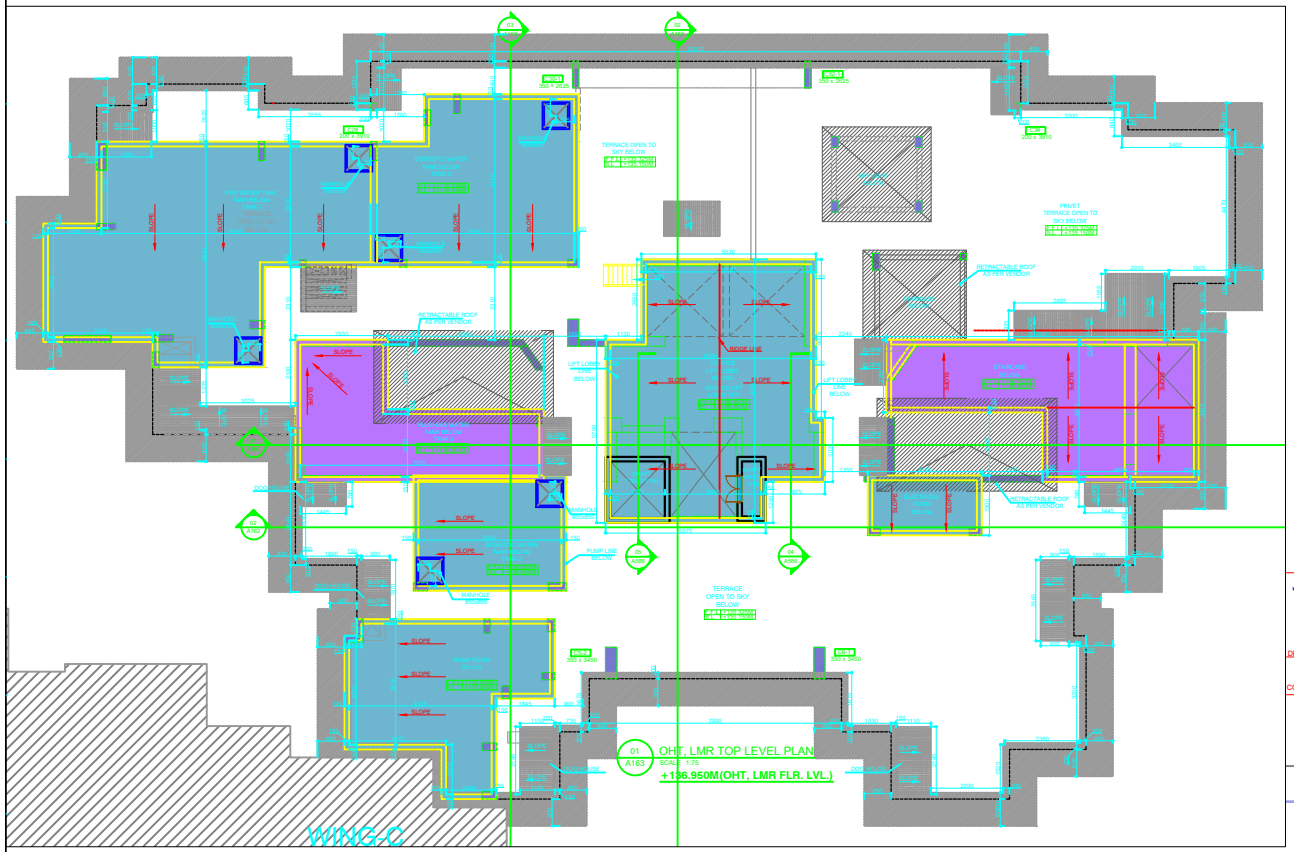


01 A163 OHT, LMR TOP LEVEL PLAN
SCALE 1:75
+136.950M(OHT, LMR FLR. LVL.)


LEGEND:-
- 250 MM TOILET SUNK
- 300 MM TOILET SUNK
- 225 MM SUNK
- SERVICE SLAB
- STRUCTURAL COLUMN & SHEARWALL
- 100 MM BLOCK WORK
- 150 MM BLOCK WORK
- 200 MM BLOCK WORK
- 100 MM NS MIVAN WALL
- 150 MM NS WALL
- 200 MM NS MIVAN WALL
- FACADE ELEMENT
- 150 MM BLOCK WORK
- MESH
- GRC
- MEP SERVICES
- TERMINATED COLUMN
- 150 MM NS WALL (2950MM HIGH)

DOOR SCHEDULE AND OPENING


DOOR	WIDTH	HEIGHT	SILL HT
D04	800	2400	0
D09	1200	1900	0
D08	1050	1900	0
D08a	1050	1650	0
D10	1050	1800	0
D11	1000	1650	300
D12	900	850	300
D13	650	850	300
D14	750	850	300
D15	750	300	250

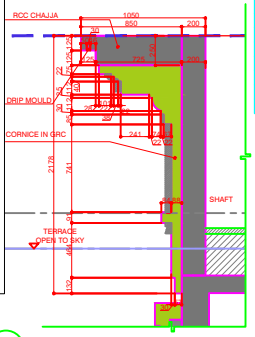

04 A163 PARAPET CORNICE DETAIL
SCALE 1:20

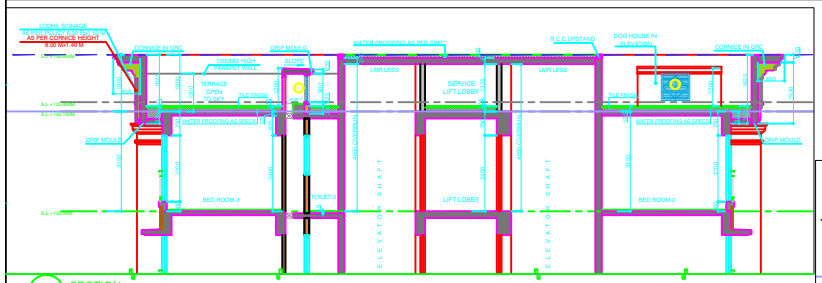

02 A163 SECTION
SCALE 1:75

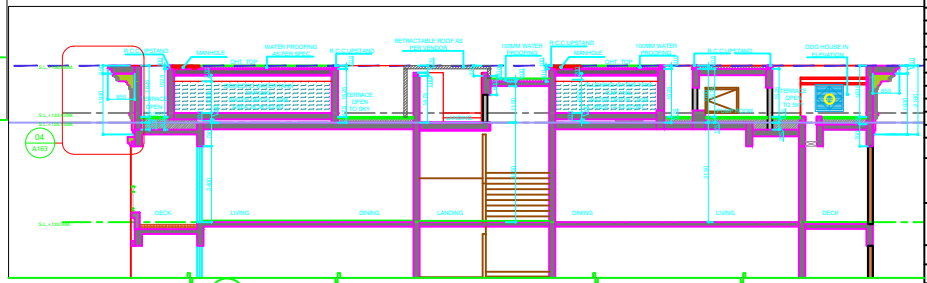

03 A163 SECTION
SCALE 1:75

#FINAL LAYOUT AS PER APPROVED I.D.SCHEME
TENTATIVE LAYOUT SHOWN FOR MEP,STRUCTURE COORDINATION

General Notes :
The term "Architect" herein specifically makes reference to "Architect Hafeez Contractor". Use of this drawing for construction shall explicitly confirm acceptance of following conditions :

1. All General Notes as per sheet G01 (General Information & Index Sheet) are applicable to this drawing sheet.
2. Do not Scale Drawings. Dimensions govern.
3. All dimensions are in millimeters unless noted otherwise.
4. All dimensions are from unfinished to unfinished levels unless otherwise specified.
5. In case of discrepancies larger scale detailed drawings shall supersede smaller scale drawings.
6. Any discrepancy in between Plan, Elevation, Section shall be immediately brought to Architects notice prior to construction on site.
7. Any discrepancy between Architecture, Structure, MEPF, Facade,other drawings shall be immediately brought to Architects notice prior to construction on site.
8. Any Irregularities in construction which occurs as a result discrepancy between Architecture, Structure, MEP, others drawings which have not been brought to the Architects notice prior to execution shall become the responsibility of the Contractor.
9. All services (MEPF) drawings are to be referred only for technical content , only coordinated working drawings to be followed for all work at site.
10. All structural sizes and details to be referred from drawings schedules given by structural consultants. However profile coordinates to be strictly as per architectural drawings.
11. All Floor Levels are Unfinished floor level (SSL) unless otherwise specified.
12. Supervision if specifically asked would be provided but responsibility regarding correct & sound construction shall solely rest with contractor/builder.
13. All relevant samples to be approved by architect prior to procurement.
14. No Shell plan/Shop drawings/Formwork drawing's issued by any agency is valid for construction unless stamped and signed by architect along with comments if any.
15. All open spaces between proposed Built Structures to site / plot boundaries Open spaces between built structures shall be cross-verified with the municipal approved drawing at site prior to commencement of construction.
16. Any discrepancy between the VFC drawings and the municipal approved drawings must be immediately brought to notice of the Architect prior to execution.

KEY PLAN



Architect

REV.	DATE	DESCRIPTION	BY
R0	25/05/2022	R0	MANGESH

Project : TOWER-C2 WING D
Zone :
Title : OHT, LMR FLOOR & SECTION
Job No : 2020-21
Drawn By : MANGESH
Scale : 1:75
Sheet : A1
Date of Plot : 25/05/2022
Check By : SAGAR
Drawing No: A163
Revision : R0