



INSIDE ELEVATION

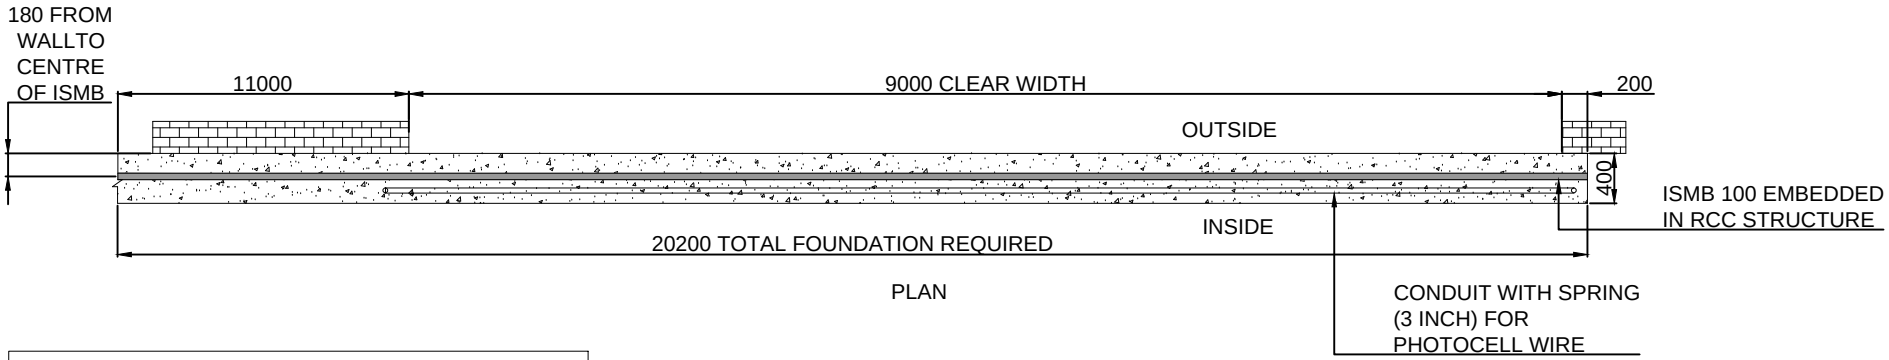

PLAN

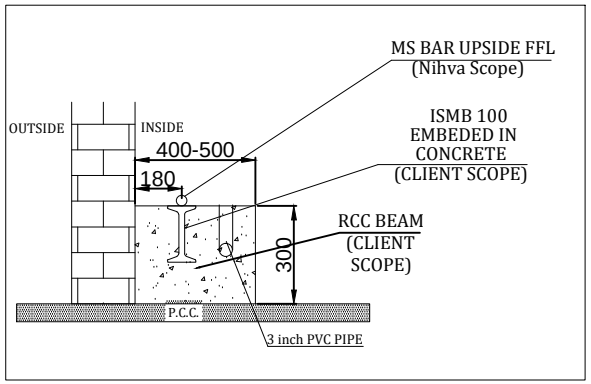

9.0m SLIDING GATE FOUNDATION

This drawing & design is the property of NIHVA TECHNOLOGIES. Not to be sold or copied to any other concern.

TITLE: FOUNDATION FOR 9M SLIDING GATE	NIHVA TECHNOLOGIES PVT. LTD.	NIHVA TECHNOLOGIES PVT. LTD. PUNE Tel : 020 66304033 Email:- info@nihva.com Website:- www.nihva.com
	SIGN	DATE
DRAWN	OMKAR	31/08/17
CHECK	SHEKHAR	31/08/17
REV.		
APPROVAL	SHEKHAR	31/08/17
If any queries contact : projects@nihva.com	CLIENT - SHILCHAR TECHNOLOGIES LTD.	
ALL DIMENSION ARE IN mm	PROJECT -	
	SITE - VADODARA	
	DWG. NO. : NIHVA/17-18/0189	
	SCALE: NTS	WT: SHEET: 01 OF 01