

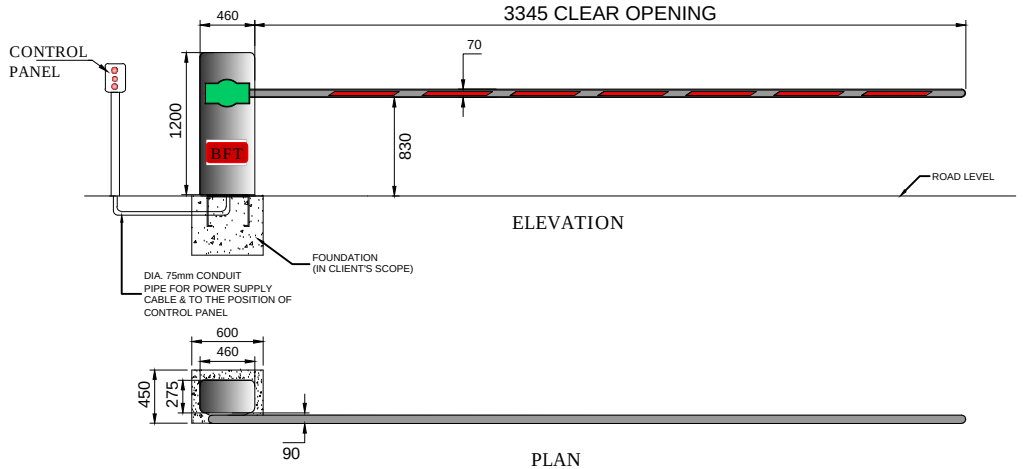


ELEVATION

PLAN

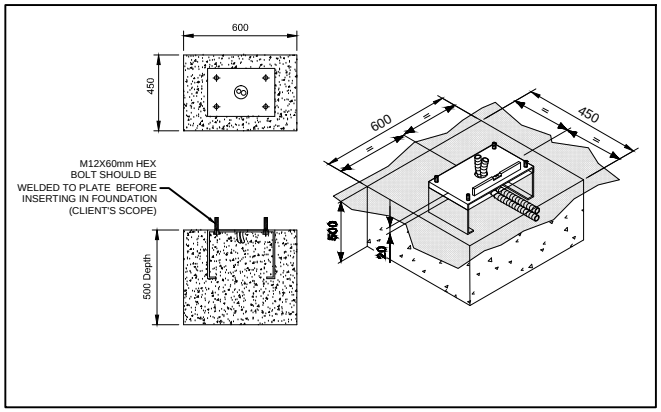

FOUNDATION DETAILS (IN CLIENT'S SCOPE)

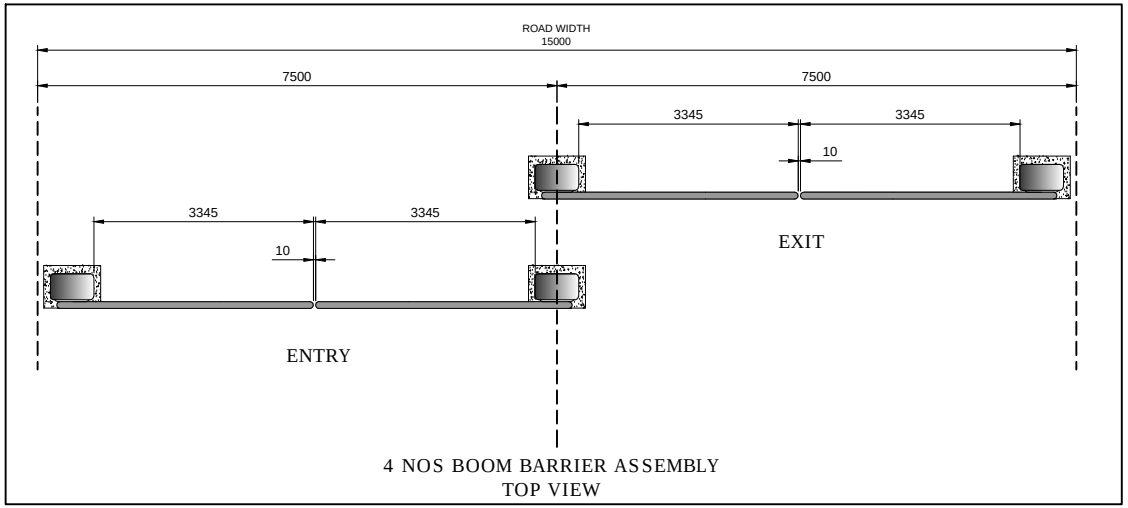

4 NOS BOOM BARRIER ASSEMBLY
TOP VIEW

R01	03.06.20	P.A	1. DETAIL VIEW ADDED
REV NO	DATE	DRAWN	REMARK

TOLERANCE - ±10mm

This drawing & design is the property of NIHVA TECHNOLOGIES. Not to be sold or copied to any other concern.

TITLE
BOOM BARRIER

NIHVA TECHNOLOGIES PVT. LTD. PUNE
Tel : 020 66304033
Email:- info@nihva.com
Website:- www.nihva.com

	NAME	SIGN	DATE
DRAWN	P.A		14.04.2020
CHECK	G.J		14.04.2020
APPROVAL			

CLIENT - SEZ BIOTECH SERVICES PVT LTD
PROJECT -
SITE LOCATION - MANJARI BK, PUNE
DWG. NO. : NIHVA/ 20-21/0002/R01 REV-R01
SCALE: NTS WT: SHEET: 01 OF 01

If any queries contact : projects@nihva.com
ALL DIMENSION ARE IN mm

R01	04.06.20	P.A	1. DETAILS ADDED
REV NO	DATE	DRAWN	REMARK