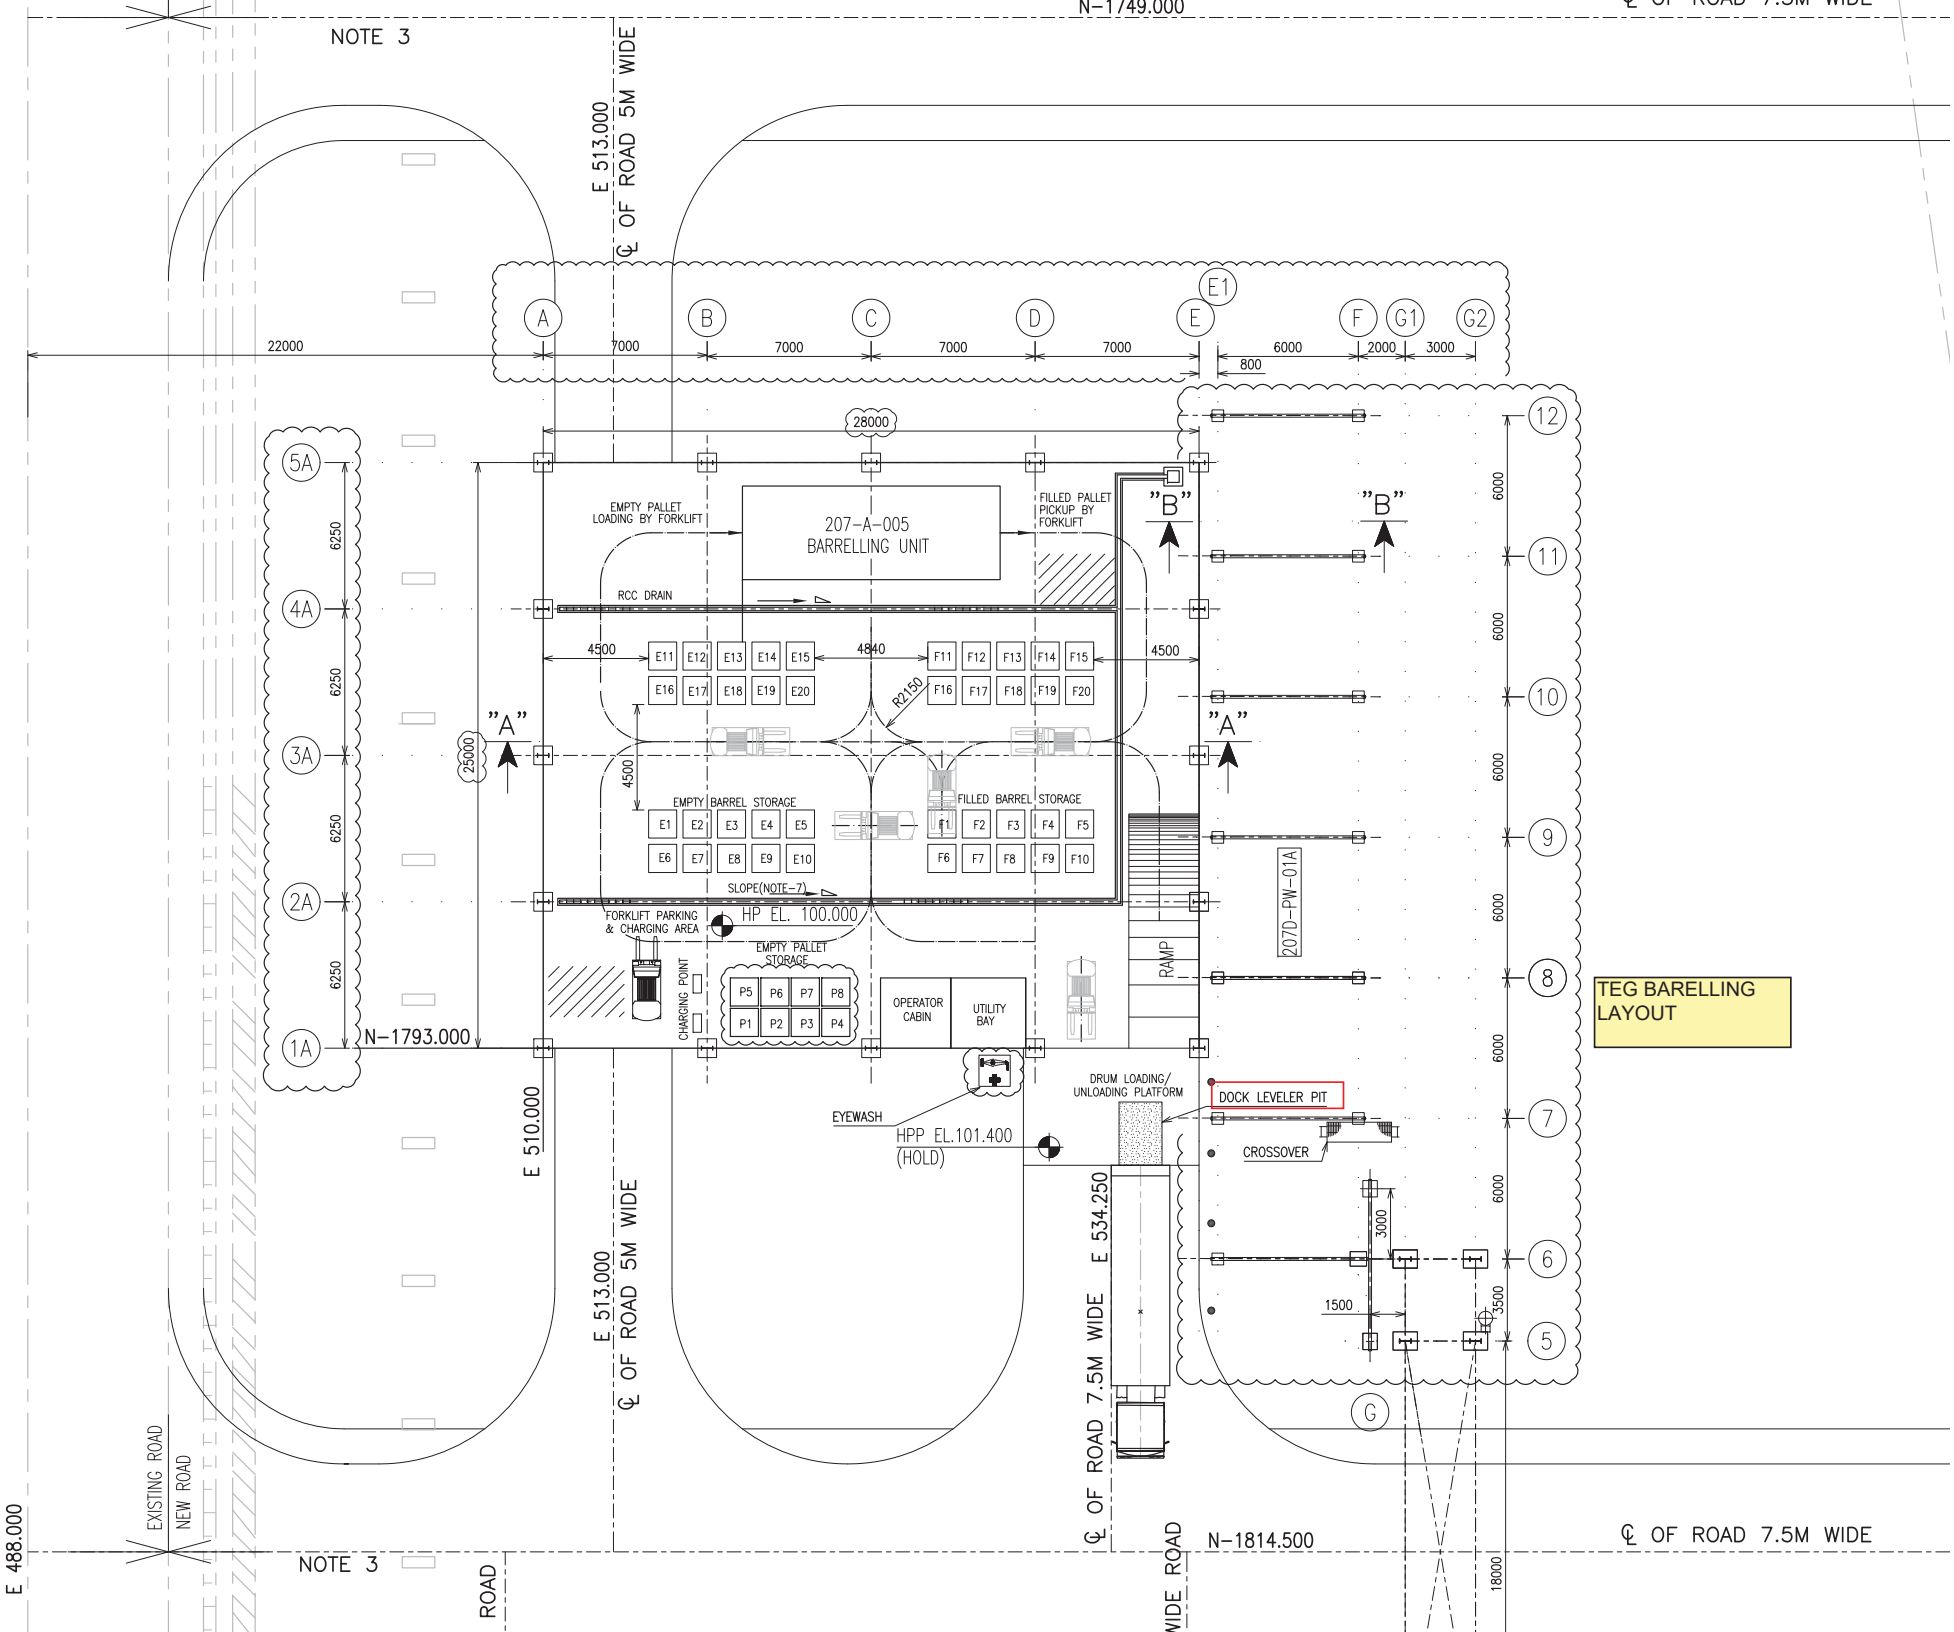

NOTE 3
N-1749.000
℄ OF ROAD 7.5M WIDE
E 513.000
℄ OF ROAD 5M WIDE
A
B
C
D
E
E1
F
G1
G2
22000
7000
7000
7000
7000
6000
2000
3000
800
28000
5A
4A
3A
2A
1A
6250
6250
6250
6250
N-1793.000
EMPTY PALLET LOADING BY FORKLIFT
207-A-005 BARRELLING UNIT
FILLED PALLET PICKUP BY FORKLIFT
RCC DRAIN
4500
4840
4500
E11 E12 E13 E14 E15
E16 E17 E18 E19 E20
F11 F12 F13 F14 F15
F16 F17 F18 F19 F20
R2150
"A"
"B"
25000
4500
EMPTY BARREL STORAGE
E1 E2 E3 E4 E5
E6 E7 E8 E9 E10
FILLED BARREL STORAGE
F1 F2 F3 F4 F5
F6 F7 F8 F9 F10
SLOPE(NOTE-7)
FORKLIFT PARKING & CHARGING AREA
HP EL. 100.000
CHARGING POINT
EMPTY PALLET STORAGE
P5 P6 P7 P8
P1 P2 P3 P4
OPERATOR CABIN
UTILITY BAY
RAMP
207D-PW-01A
EYEWASH
HPP EL.101.400 (HOLD)
DRUM LOADING/ UNLOADING PLATFORM
DOCK LEVELER PIT
CROSSOVER
3000
1500
3500
6000
12
11
10
9
8
7
6
5
G
E 510.000
E 513.000
℄ OF ROAD 5M WIDE
E 534.250
℄ OF ROAD 7.5M WIDE
TEG BARELLING LAYOUT
E 488.000
EXISTING ROAD
NEW ROAD
NOTE 3
N-1814.500
℄ OF ROAD 7.5M WIDE
ROAD
WIDE ROAD
18000