
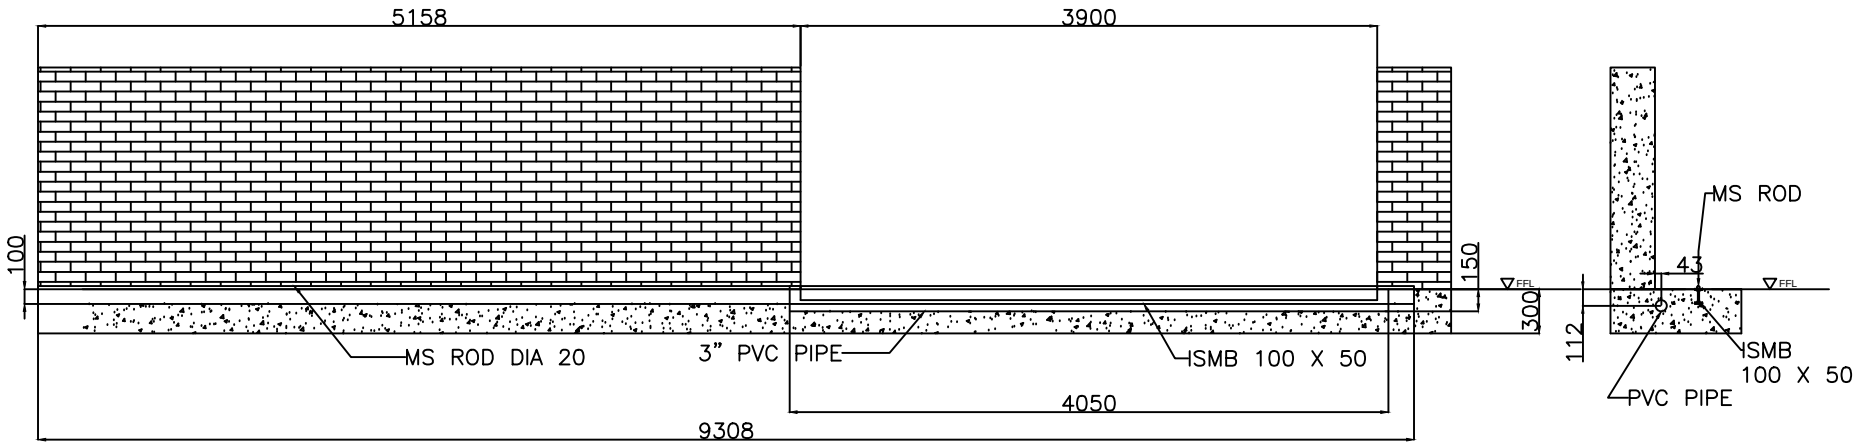


ELEVATION VIEW

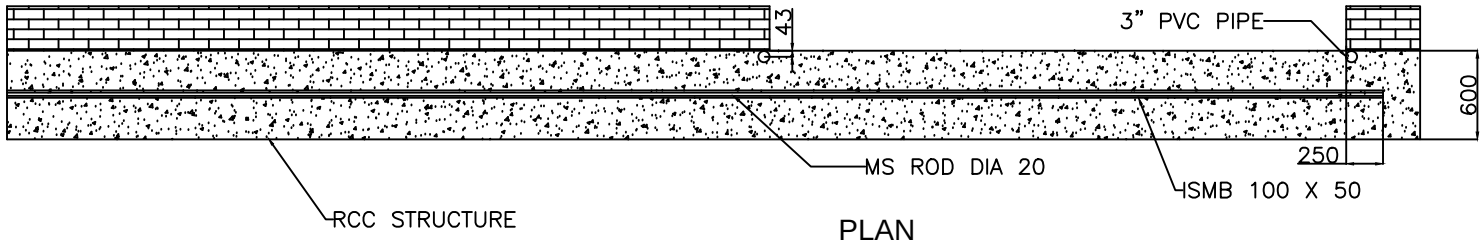

PLAN

Technical Specs of Motorized Sliding Gate

1. Parking length required - 5250mm
2. Bottom Rail - Bright bar Ø20mm
3. Total leaf weight ≈ 825 kg
4. ISMB 100 X 50 positioned in the foundation.

Note-

1. All dimension are in mm.
2. All civil work is under client scope.
3. 3" PVC pipe in the foundation to be provided by NIHVA.
4. Power supply 3 phase 440v, 50hz.
5. Cable for power supply 2.5 sqmm 4 core
6. Cable for photocell - 1.5 sqmm 4 core

This drawing & design is the property of NIHVA TECHNOLOGIES. Not to be sold or copied to any other concern.

TITLE	NAME	SIGN	DATE	
SLIDING GATE FOUNDATION DRAWING				NIHVA TECHNOLOGIES PVT. LTD. PUNE Tel : 020 66304033 Email:- info@nihva.com Website:- www.nihva.com
DRAWN	G.P.		08.09.21	CLIENT -HAIMAVATHY PROPERTIES PVT. LTD.
CHECK	A.K.		08.09.21	LOCATION - MUMBAI
APPRD.	V.T.		08.09.21	PRODUCT - SLIDING GATE 3900 X 2000
If any queries contact : design@nihva.com				NIHVA\21-22\0230 / REV- 00
ALL DIMENSION ARE IN mm				SCALE: NTS / SHEET: 02 OF 02