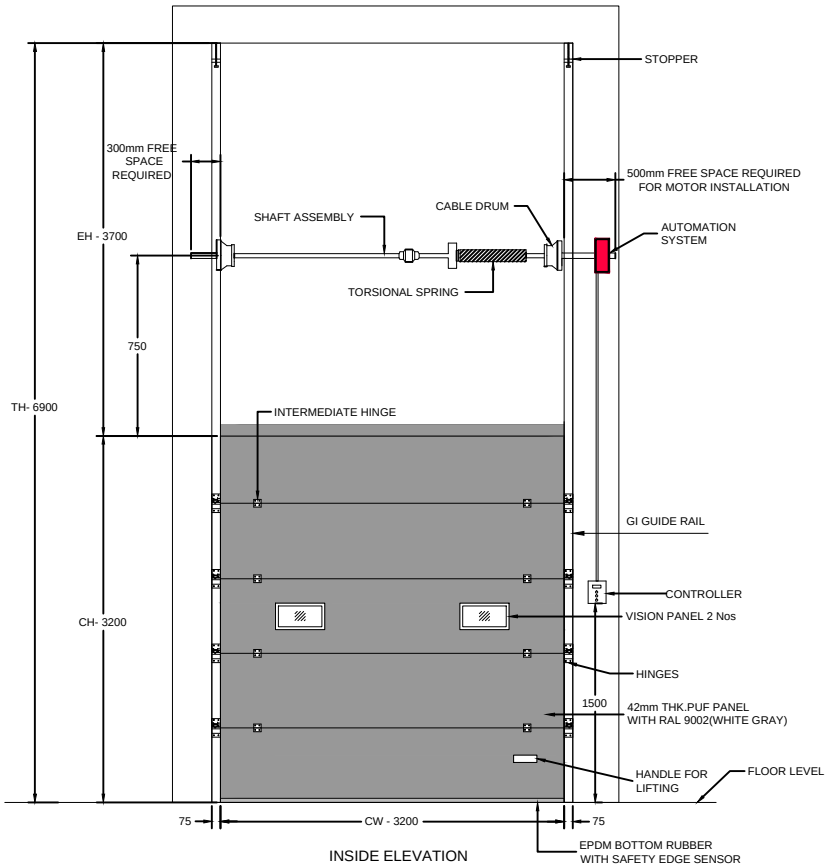
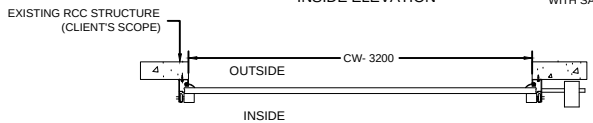
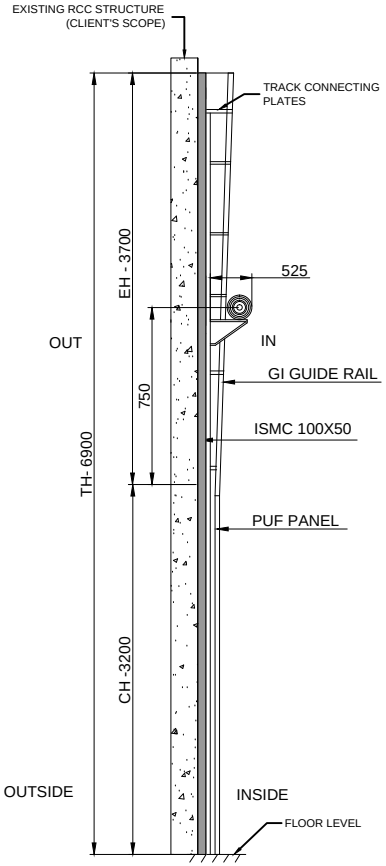


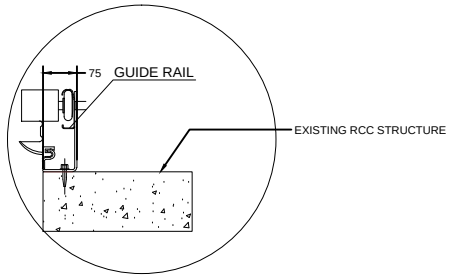

INSIDE ELEVATION




PLAN




SIDE VIEW




TRACK DETAILS

IMPORTANT NOTES:

1. REQUIRED STRUCTURE FOR DOOR SHALL BE IN CLIENT'S SCOPE.
2.SINGLE PHASE POWER SUPPLY REQUIRED AT DOOR LOCATION.
3.ALL CIVIL WORK SHALL BE CLIENT'S SCOPE.

| SR NO | CLEAR WIDTH (CW) | CLEAR HEIGHT (CH) | QUANTITY | EH | TH | RAL |
|---|---|---|---|---|---|---|
| 1 | 3200 | 3200 | 1 | 3700 | 6900 | 9002 |

This drawing & design is the property of NIHVA TECHNOLOGIES. Not be sold or copy to any other concern.

TITLE: SECTIONAL DOOR VL (MOTORIZED)

NIHVA TECHNOLOGIES PVT. LTD. PUNE
Tel : 020 66304033
Email:- info@nihva.com
Website:- www.nihva.com

| | NAME | SIGN | DATE |
|---|---|---|---|
| DRAWN | P.V.A | | 26.06.2019 |
| CHECK | V.M.T | | 26.06.2019 |
| APPROVAL | | | |

CLIENT - WELSPUN INDIA PVT LTD
PROJECT -
SITE LOCATION- GUJRAT
DWG. NO. : NIHVA/19-20/0040 | REV : R00
If any queries contact : projects@nihva.com | SCALE: NTS | WT: | SHEET: 01 OF 01
ALL DIMENSION ARE IN mm