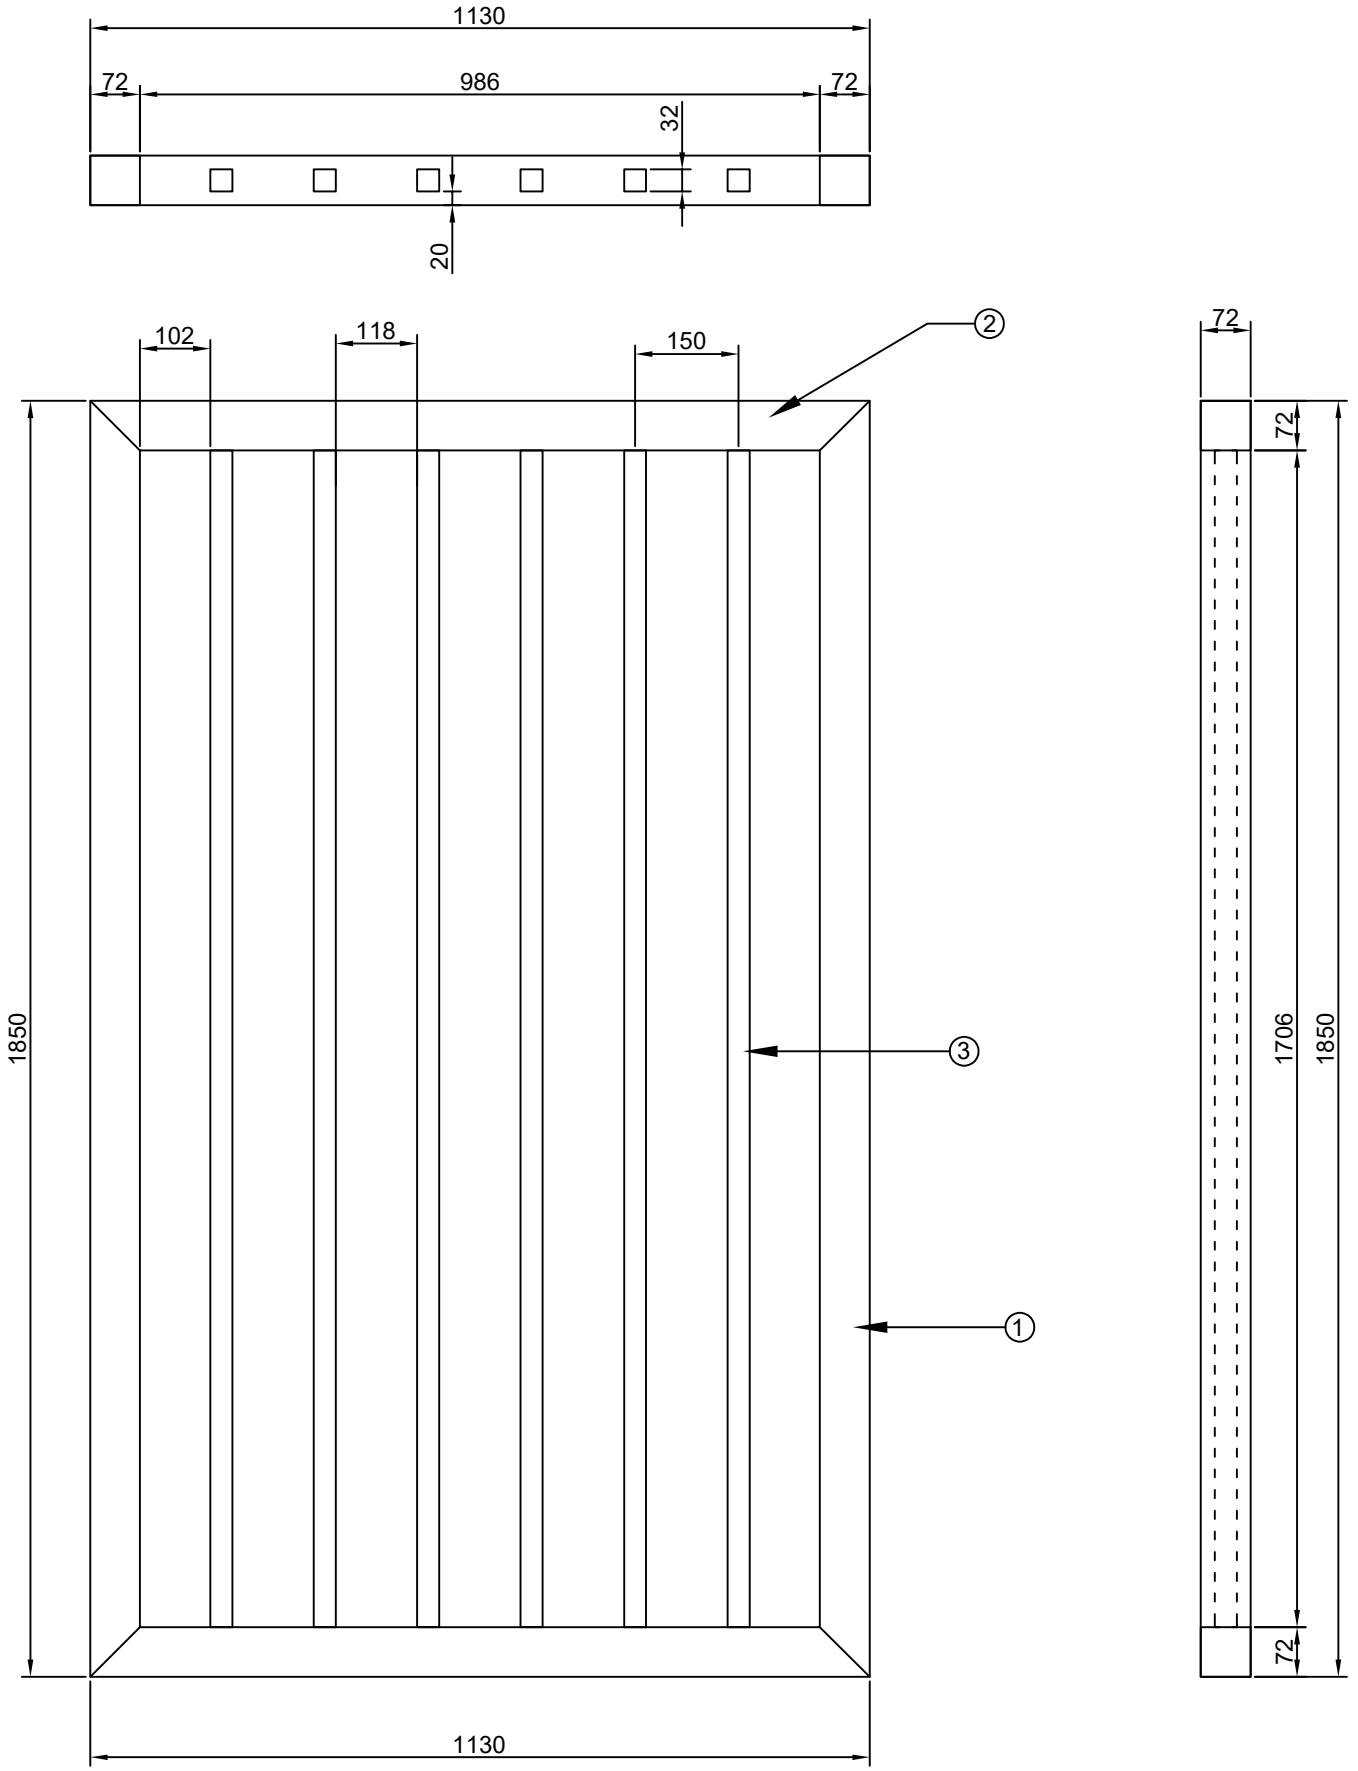


QTY:-2 NOS

BOM			
SL NO.	DESCRIPTION	SPECIFICATION	QTY
1	MS SQ. TUBE	72X72X3.2X1850L	2NOS
2	MS SQ. TUBE	72X72X3.2X1130L	2NOS
3	MS SQ. TUBE	32X32X2.6X1706	6NOS

This drawing & design is the property of NIHVA TECHNOLOGIES. Not to be sold or copied to any other concern.

TITLE:- WICKET GATE

NIHVA TECHNOLOGIES PVT. LTD.

	NAME	DATE	SIGN
DRAWN	SUJATA	06/10/2022	
CHECK			
APPRD.			

If any queries contact : design1@nihva.com

ALL DIMENSION ARE IN mm

CLIENT - Fluxcon Infrateck Pvt Ltd

LOCATION -Pune

PRODUCT - WICKET GATE | QTY:-2 NOS

DWG NO:-NIHVA/22-23/MFG/0091 | REV- 01

SCALE: NTS | SCALE:-- 1:1 | SHEET: 01 OF 01

1.	Revision	Date	Revised By