


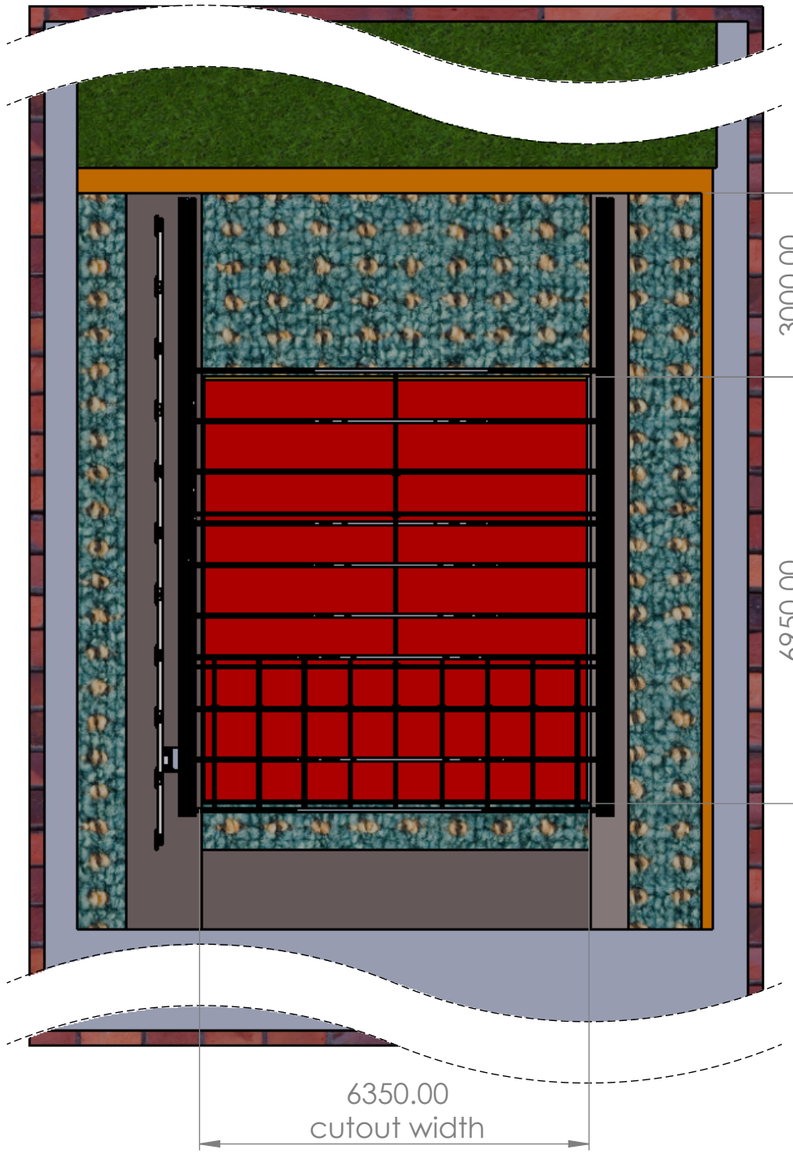


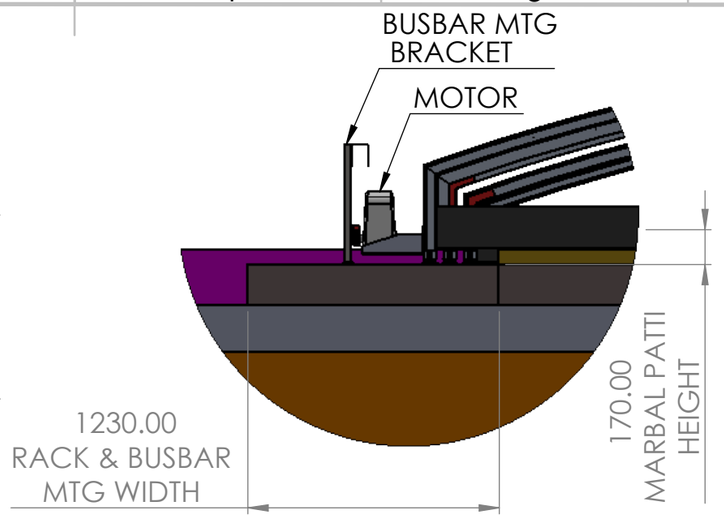


DETAIL B
SCALE 1 : 30

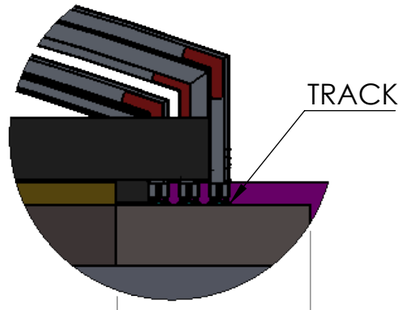

DETAIL C
SCALE 1 : 20

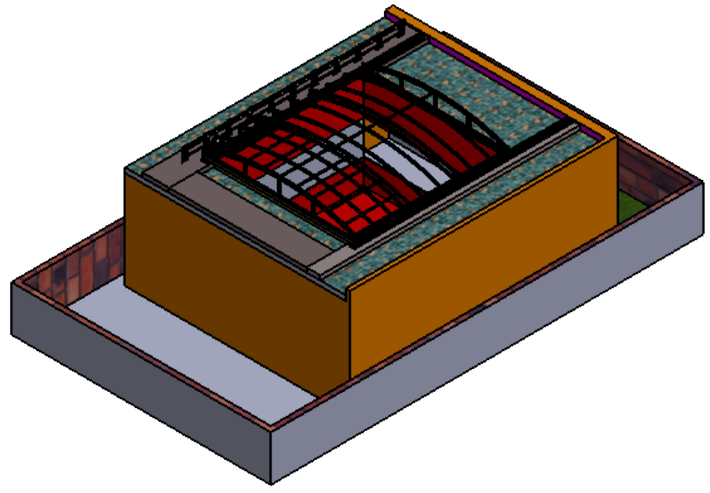

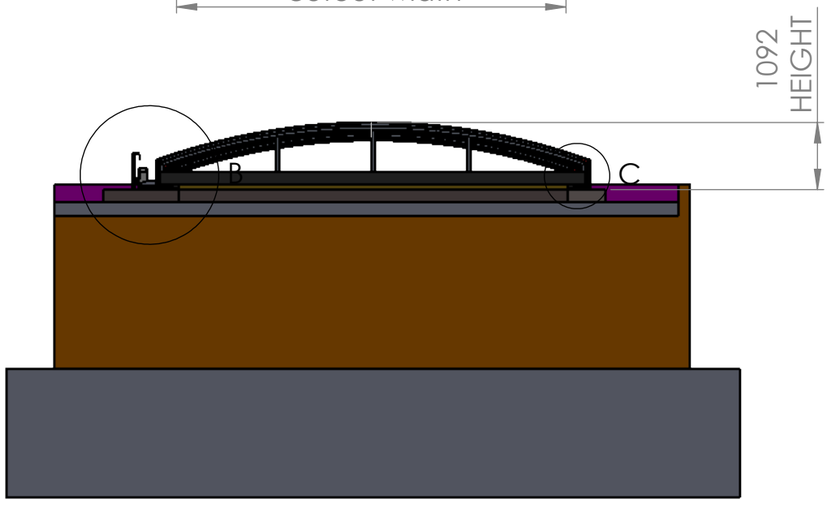

TITLE :	GA		
	NAME	SIGNATURE	DATE
DRAWN	SURAJ . W		22-03-2025
CHK'D	PRANAV M.		23-03-2025
APPV'D	VIJAY T.		23-03-2025
		DIMENSIONS ARE IN MILLIMETERS	

NIHVA Technologies Pvt. Ltd.
NIHVA TECHNOLOGIES PVT LTD

CLIENT NAME :	SALAVI MAM
PRODUCT NAME :	RETRACTABLE ROOF
SITE LOCATION :	GUJARAT
DWG NO.	GA
	A3
REVISION :	0
SCALE:	SHEET 1 OF 1