
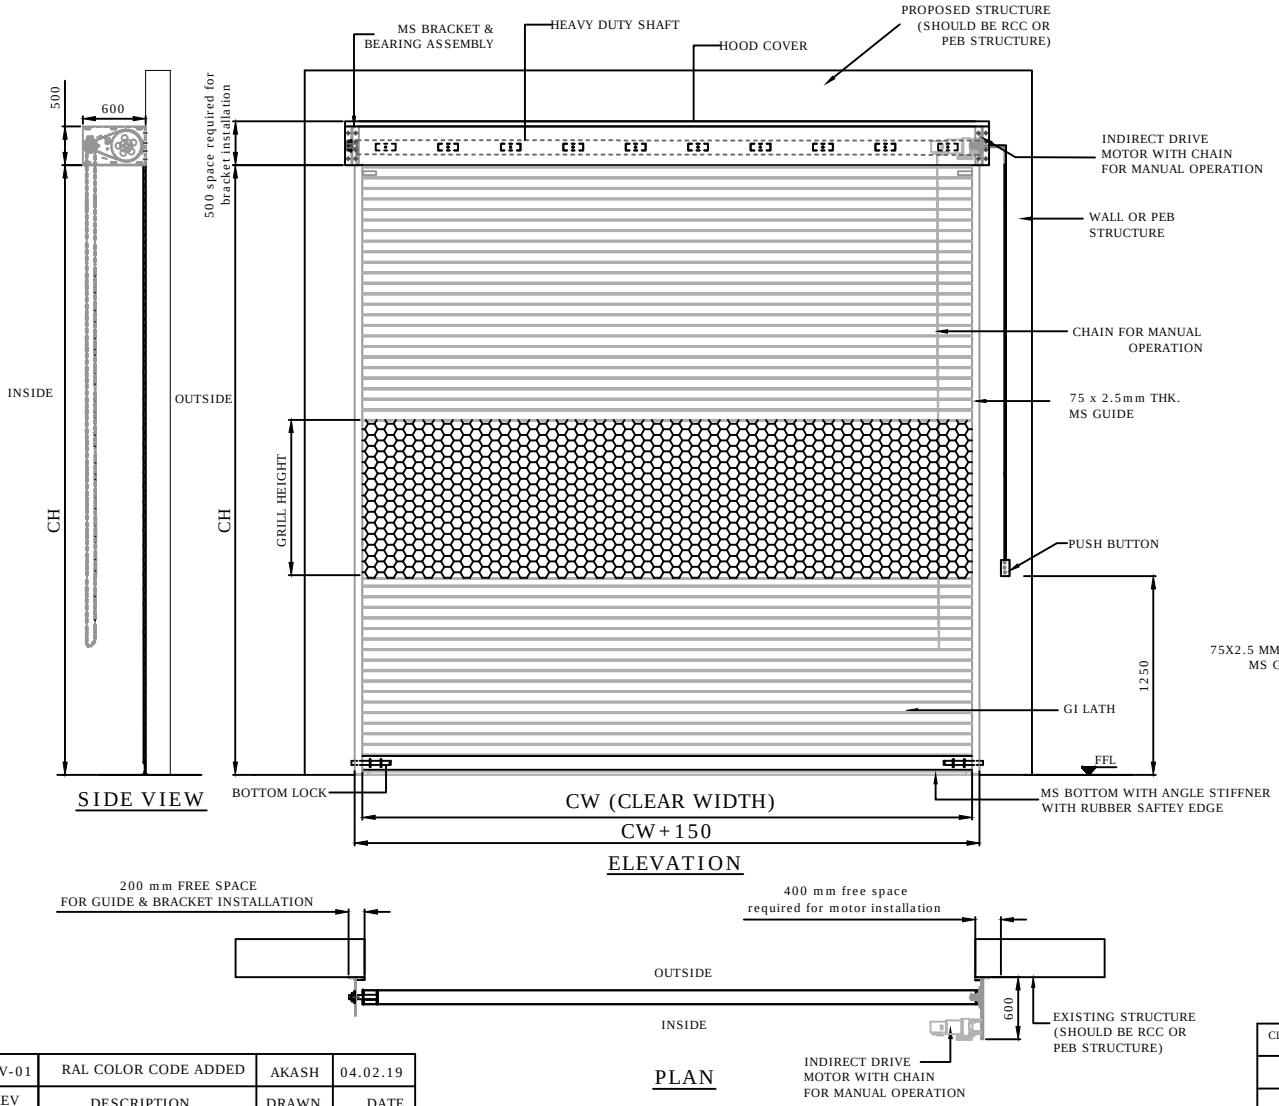
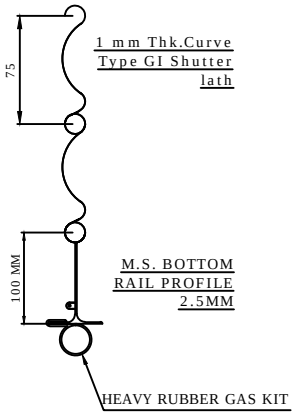



M.S. BOTTOM RAIL PROFILE 2.5MM

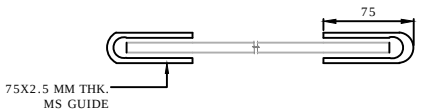


RAL Code - 7035 Grey

| CLEAR WIDTH (CW) | CLEAR HEIGHT (CH) | QUANTITY | GRILL HEIGHT |
|---|---|---|---|
| 3000mm | 3000mm | 10 NOS | 1000mm |
| 2400mm | 3000mm | 01 NOS | 1000mm |

| REV | DESCRIPTION | DRAWN | DATE |
|---|---|---|---|
| REV-01 | RAL COLOR CODE ADDED | AKASH | 04.02.19 |

DIMENSION :

| CLEAR WIDTH | CLEAR HEIGHT | QUANTITY |
|---|---|---|
| 3000 | 3000 | 10 NOS |
| 2400 | 3000 | 01 NOS |

MATERIAL:

THICKNESS :

NOTE:
1. REQUIRED STRUCTURE FOR ROLLING SHUTTER WILL BE CLIENT'S SCOPE.
2. ONE COAT OF RED OXIDE PRIMER WILL BE GIVEN TO THE SHUTTER.
3. SINGLE PHASE. 3 CORE 1.5 SQ. CABLE REQUIRE AT SITE(CLIENT'S SCOPE)
4. FINAL FINISH WILL BE AS SUPPLIED EARLIER.

NIHVA TECHNOLOGIES PVT. LTD.
NIHVA TECHNOLOGIES PVT. LTD. PUNE
Email:- info@nihva.com
Website:- www.nihva.com

TITLE:

# MOTORIZED ROLLING SHUTTER

CLIENT'S APPROVAL :

CLIENT - TATA PROJECT LTD.

PROJECT -ALSTOM.

SITE LOCATION - MADHEPURA

DWG. NO. : NIHVA/18-19/0265/R01

| SCALE: NTS | WT: | SHEET:1 OF 1 |
|---|---|---|

| | |
|---|---|
| DRAWN BY: A.K. | DATE: 04.02.2019 |
| CHECK BY : P.A. | DATE: 04.02.2019 |
| APPROVED BY : R.D | DATE: 04.02.2019 |

If any queries contact : projects@nihva.com

NOTE: ALL DIMENSIONS ARE IN mm

THIS DRAWING & DESIGN IS THE PROPERTY OF NIHVA TECHNOLOGIES. NOT TO BE SOLD OR COPIED TO ANY OTHER CONCERN.