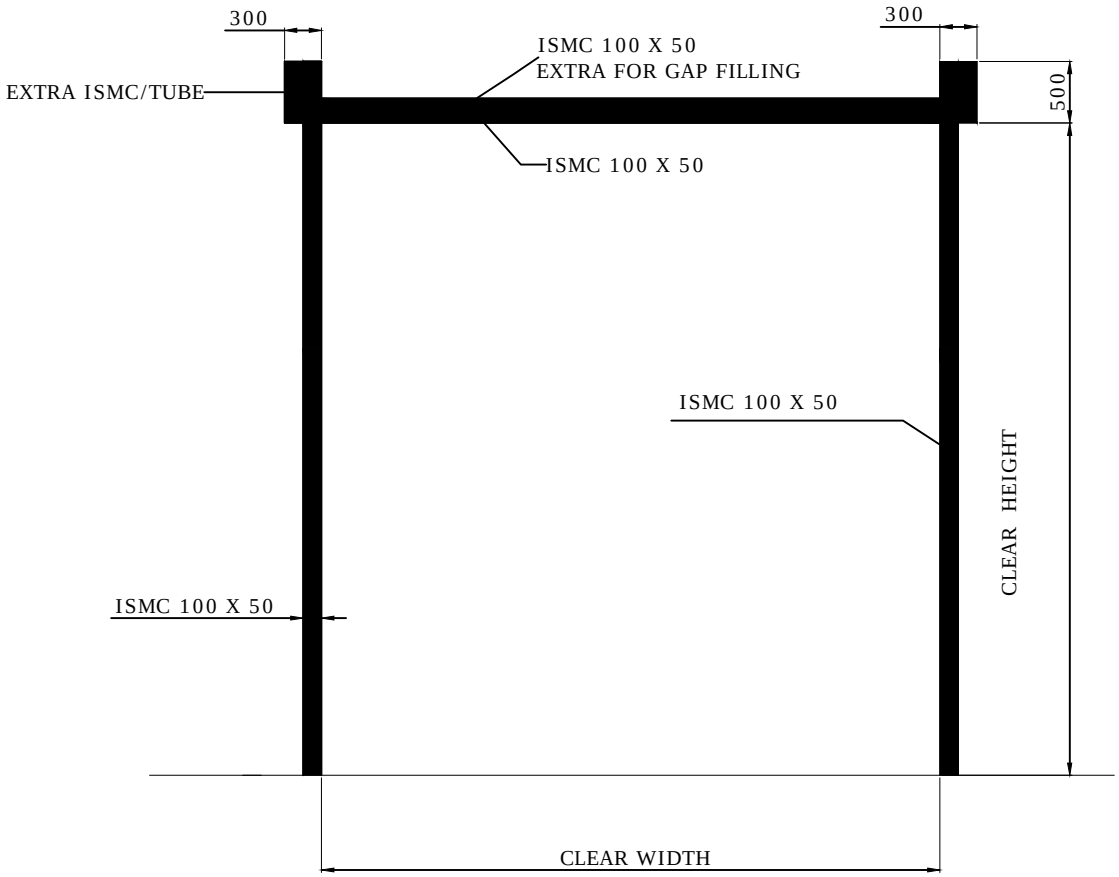


| CLEAR WIDTH | CLEAR HEIGHT | QTY. |
|---|---|---|
| 4000mm | 3150mm | 01NO |

NOTE :

1. MATERIAL FOR ALL STRUCTURE = M.S
2. REQ. CIVIL WORK & M.S STRUCTURE WILL BE IN CLIENT SCOPE.

| CLEAR WIDTH (CW) | CLEAR HEIGHT (CH) | QUANTITY |
|---|---|---|
| 4000 | 3150 | 1 NO |

TOLERANCE ±10 MM

| REV NO | DATE | DRAWN | REMARK |
|---|---|---|---|
| R01 | 25.12.19 | P.A | 1. EXTRA ISMC ADDED |

This drawing & designing is the property of NIHVA TECHNOLOGIES. Not to be sold or copied to any other concern.

TITLE MOTORIZED ROLLING SHUTTER STRUCTURE

NIHVA TECHNOLOGIES PVT. LTD. PUNE
Tel : 020 66304033
Email:- info@nihva.com
Website:- www.nihva.com

| | NAME | | DATE |
|---|---|---|---|
| DRAWN | P.A | | 19.12.19 |
| CHECK | G.J | | 19.12.19 |
| REV. | | | |
| APPROVAL | | | |

If any queries contact : projects@nihva.com

ALL DIMENSION ARE IN mm

CLIENT - BSA

PROJECT -

SITE LOCATION - CHAKAN

DWG. NO. : NIHVA/19-20/0179/R01 REV : R01

SCALE: NTS WT: SHEET: 01 OF 01