


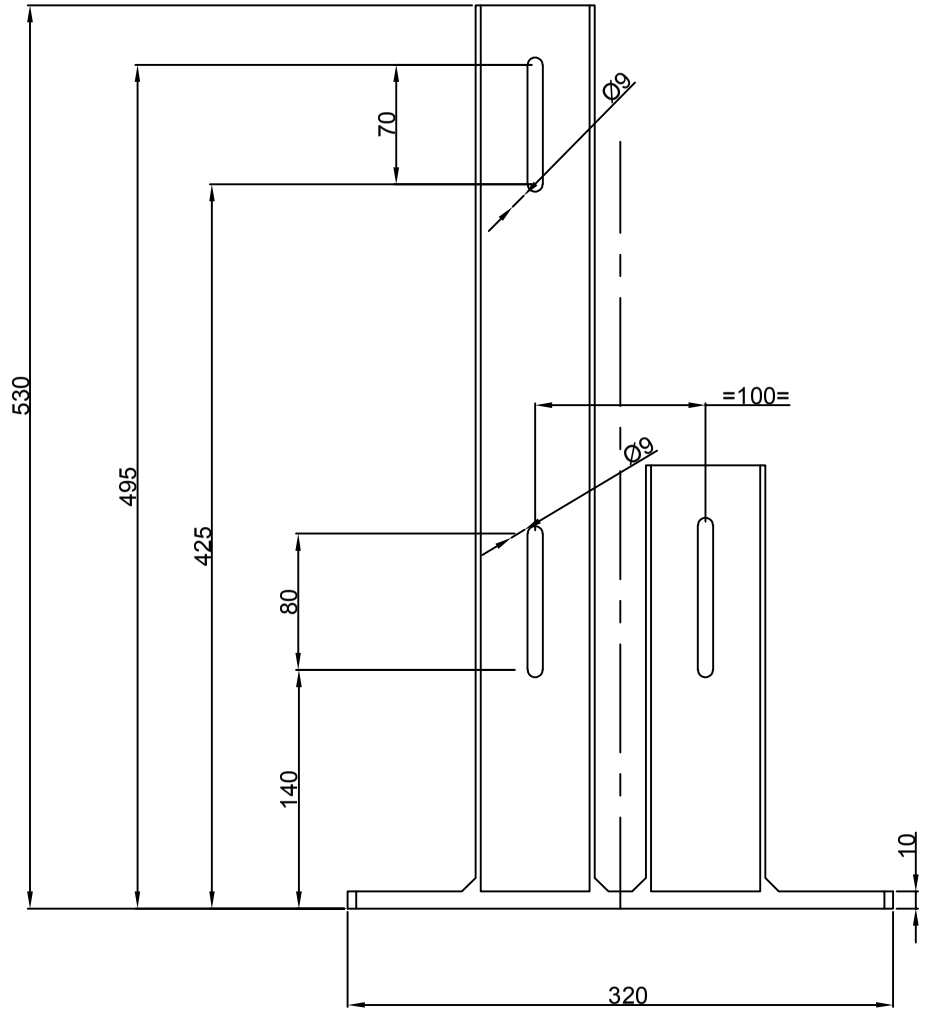

C CHANNEL FRAME-02
MATL-MS
QTY-02
DRG NO-01-02

SR NO.	REV NO.	Date	Revised By

TITLE:- C CHANNEL FRAME-02				NIHVA TECHNOLOGIES PVT. LTD. PUNE Tel : 020 66304033 Email:- info@nihva.com Website:- www.nihva.com
	NAME	DATE	SIGN	
DRAWN	KISHAN	20/07/22		CLIENT - NIHVA TECHNOLOGIES PVT.LTD
CHECK	G. JAIN	20/07/22		LOCATION -
APPRD.	V. TARAK			PRODUCT - RETRACTABLE ROOF
If any queries contact : design@nihva.com				DWG NO:-NIHVA/22-23/MFG/0036 / REV- 0
ALL DIMENSION ARE IN mm				SCALE: NTS / SCALE:-- 1:1 / SHEET: 01 OF 01