
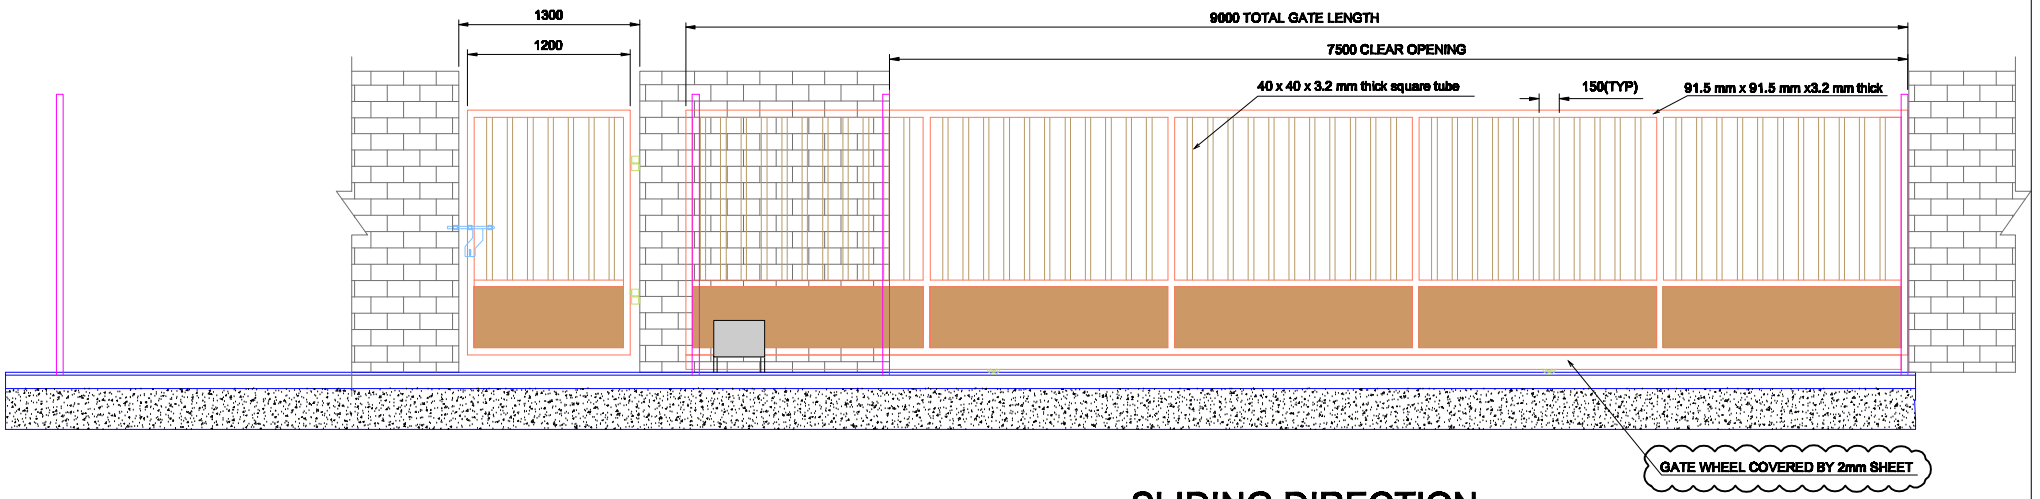
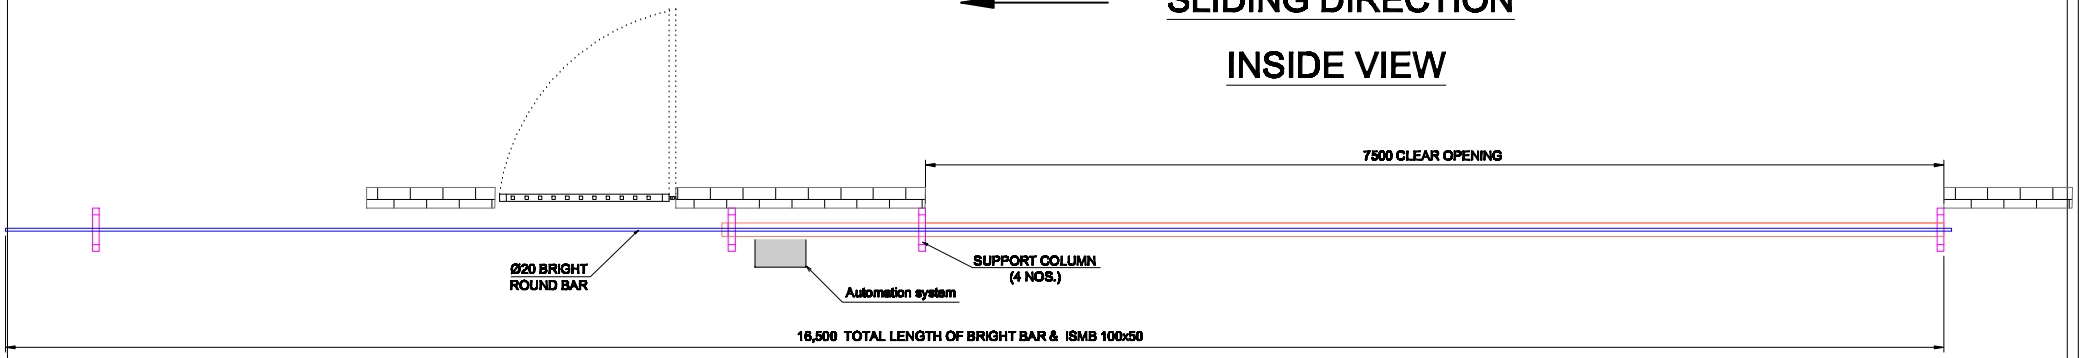
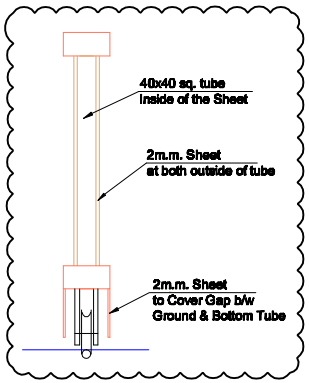



## SLIDING DIRECTION

## INSIDE VIEW

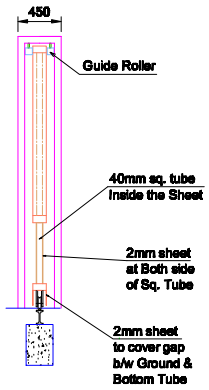


Clear Opening size - 7500X1800mm
Total length of gate - 9000 1800mm
Wicket gate size - 1200X1800mm , Qty - 2 nos.
Saftey Photo cell - 1 pair.
No. Of Column - 4 nos.
Factory paint finish - Red oxide primer coat
NOTE :- Supply of 'c' channel for vertical support of wicket gate in NIHVA scope
*Excavation and civil work for grouting of 'c' channel & I beam will be in client scope.

This drawing & designing is the property of NIHVA TECHNOLOGIES. Not be sold or copy to any other concern.

| TITLE | MOTORIZED SLIDING GATE | | NIHVA TECHNOLOGIES PVT. LTD. |
|---|---|---|---|
| | SIGN | DATE | |
| DRAWN | ABHIJIT | 20/04/15 | CLIENT - PMP DRIVE SYSTEM |
| CHECK | ANIL | 20/04/15 | PROJECT - PMP DRIVE SYSTEM |
| REV. | 01 | | SITE - CHAKAN |
| APPROVAL | | | DWG. NO. : NIHVA/15-16/013 |
| If any queries contact : projects@nihva.com | | | SCALE: 01 / WT: / SHEET: 01 OF 02 |
| ALL DIMENSION ARE IN mm | | | |

NIHVA TECHNOLOGY PVT. LTD. PUNE
Tel : 020 66304033
Email:- info@nihva.com
Website:- www.nihva.com