

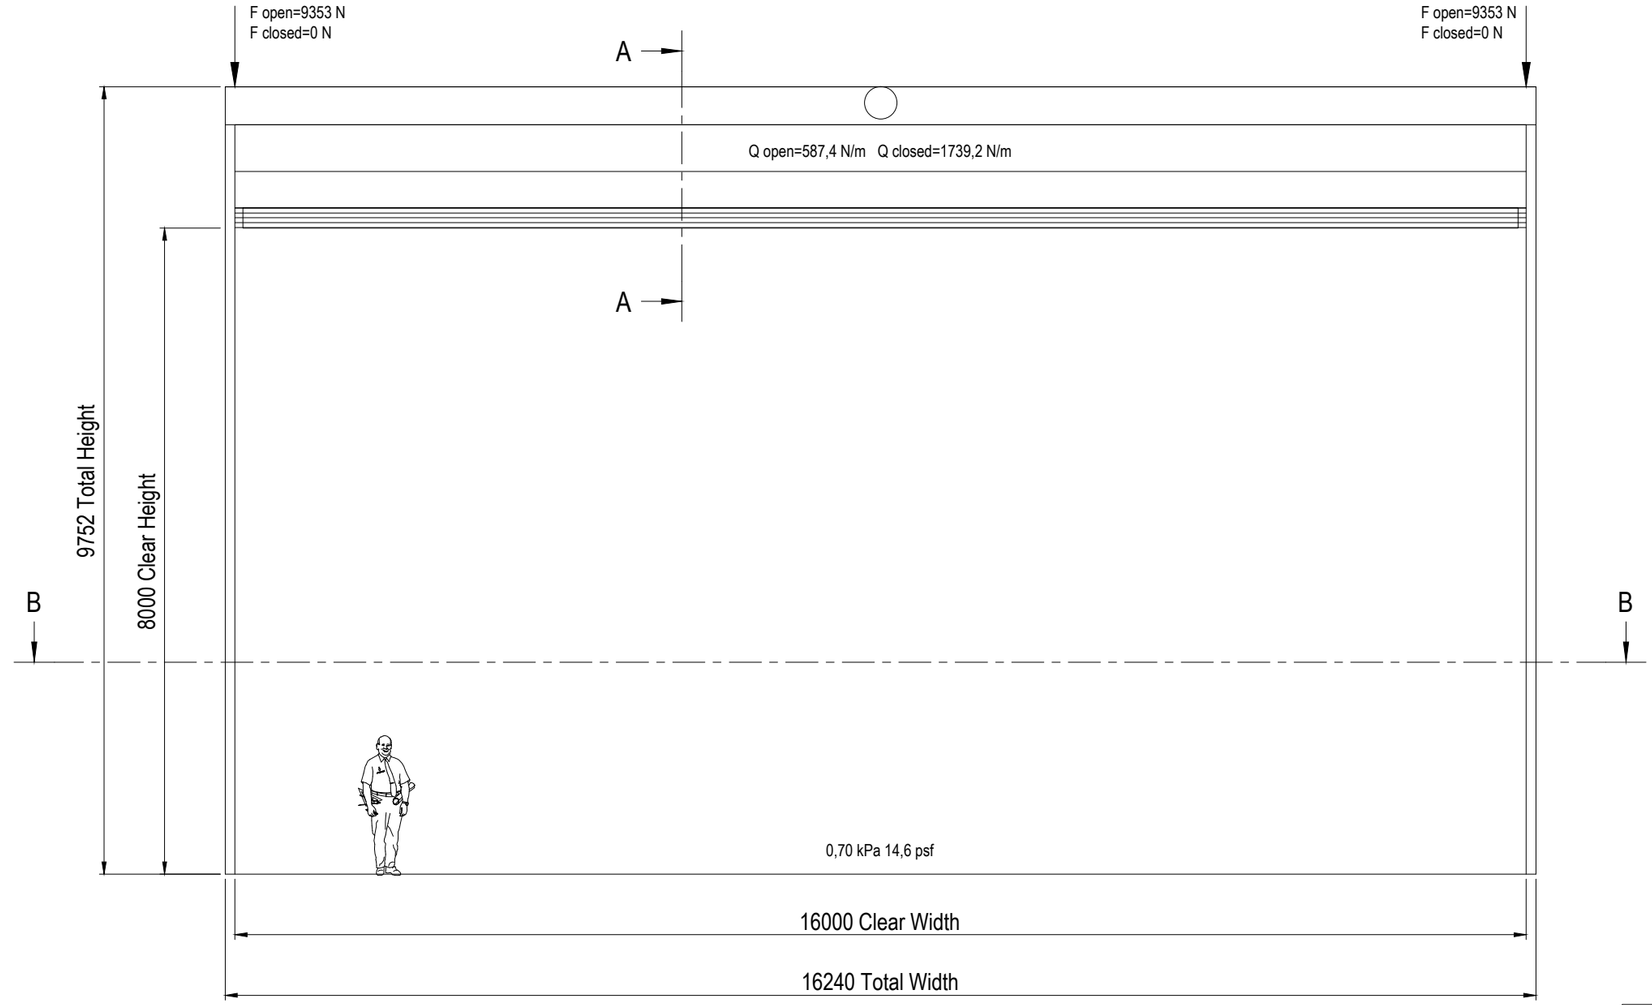


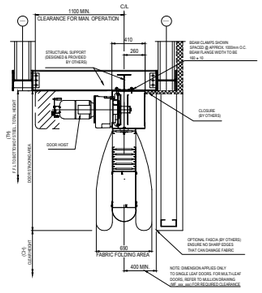


*PRELIMINARY DESIGN DATA: SHOULD NOT BE USED FOR FINAL DESIGN

SECTION A-A

Quotation only. Do not use for design.
Nominal static vertical loads are indicated.
A dynamic surload factor of 1.25 should be added to door leaf loads in open position.
Includes items provided by ASSA ABLOY Entrance Systems only.
Total weight: 3073 kg
Total static weight: 2893 kg
Total motor power: 5,0 kW
Total rated current: 10,2 A
Total peak current: 45,0 A
Power supply: 400V/50Hz/3ph
(max. allowed voltage drop at start: 5%)
Control system: 24V
Mains power to control panel supplied by others than ASSA ABLOY Entrance Systems.

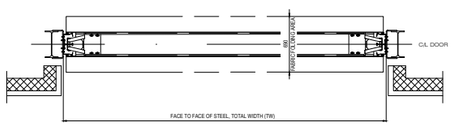

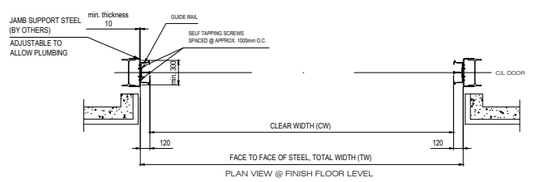

*PRELIMINARY DESIGN DATA: SHOULD NOT BE USED FOR FINAL DESIGN

SECTION B-B

ASSA ABLOY

SALES REP. Peter Bergmark	DATE ISSUED 2017-11-27
SALES No. 217399	DATE DRAWN 2017-11-27
SCALE N.T.S.	
DRAWING No. 217399	REVISION

Cummins

India

Load diagram

NIHVA