
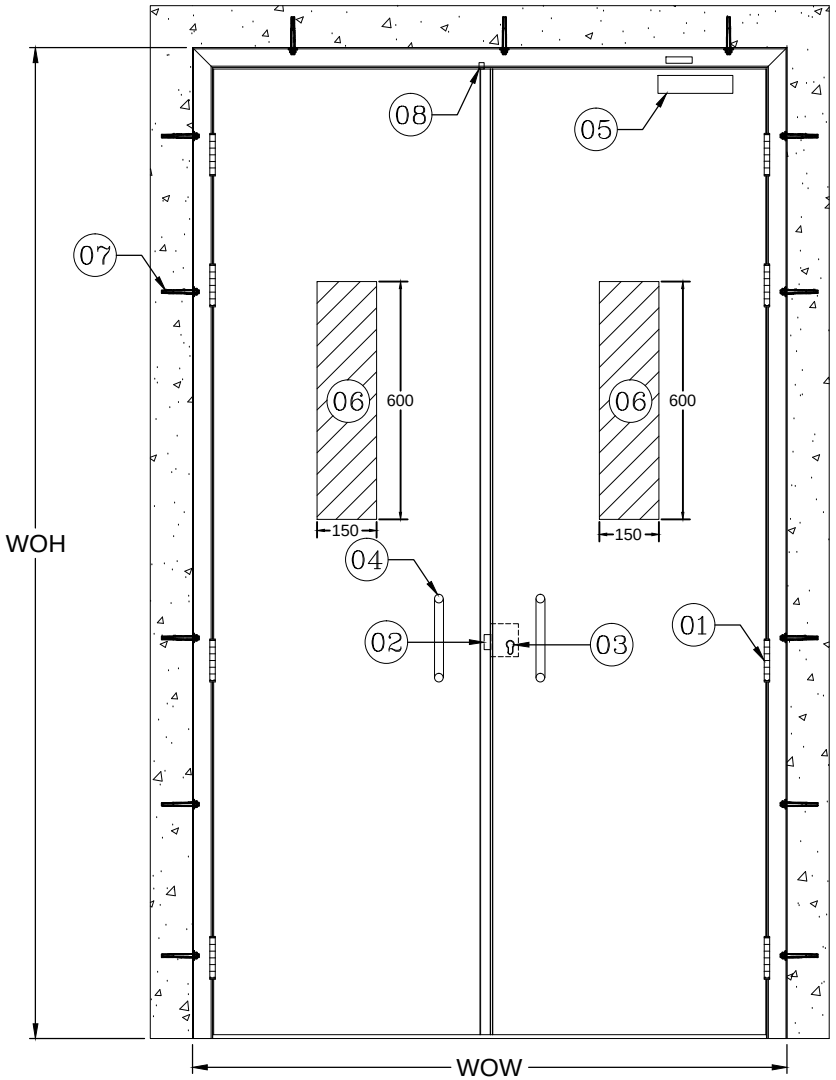


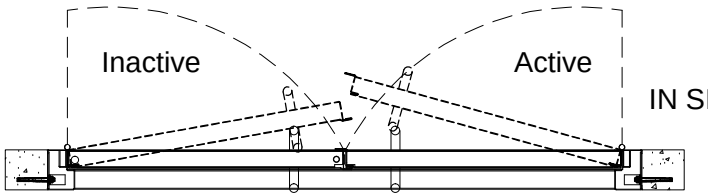

Abbrevation's:
WOW-Wall Opening Width
WOH-Wall Opening Height

Hardware List:-

SR.NO	DESCRIPTION	QTY.
01	HINGES	08 Nos.
02	DEAD LOCK	01 No.
03	CYLINDER WITH BOTH SIDE KEY	01 No.
04	BOTH SIDE`D'HANDLE	02 Nos.
05	DOOR CLOSER	01 No.
06	VISION PANEL 150X600	02 Nos.
07	ANCHOR FASTENERS	13 Nos.
08	CONCELED TOWER BOLT	01 No.

DOOR OPENING TYPE: TYPE 6 - RIGHT HAND ACTIVE

(for opening type refer door handling sheet)

Door Sizes :-

SR.NO	WOW	WOH	QTY.
01	1495	2495	01 No.
02	1490	2445	01 No.

COLOR : RAL 9016 TRAFFIC WHITE

NOTE:-
*All Dimensions are in mm.
*Tolerance:-All Linear Dimensions ±3mm,Others ±0.5mm.
*The Drawing Is For Location of Hardware only. Drawing Does Not Represent The Hardware For More Clarity, Please Go Through Hardware Broucher.

NIHVA TECHNOLOGIES PVT. LTD.
NIHVA TECHNOLOGIES PVT. LTD. PUNE
Email:- info@nihva.com
Website:- www.nihva.com

TITLE:
STEEL DOOR(DOUBLE LEAF)

CLIENT'S APPROVAL :

CLIENT - RUTCON CONSTRUCTION PROJECT PVT. LTD.
PROJECT - JISL SITE HUBBALLI
SITE LOCATION -
DWG. NO. : NIHVA/16-17/0045
SCALE: NTS | WT: | SHEET:1 OF 1
DRAWN BY: ANIL KHOT DATE: 25-07-2016
CHECK : ANIL DATE: 25-07-2016
If any queries contact : projects@nihva.com
NOTE: ALL DIMENSION ARE IN mm

THIS DRAWING & DESIGNING IS THE PROPERTY OF NIHVA TECHNOLOGIES. NOT BE SOLD OR COPY TO ANY OTHER CONCERN.