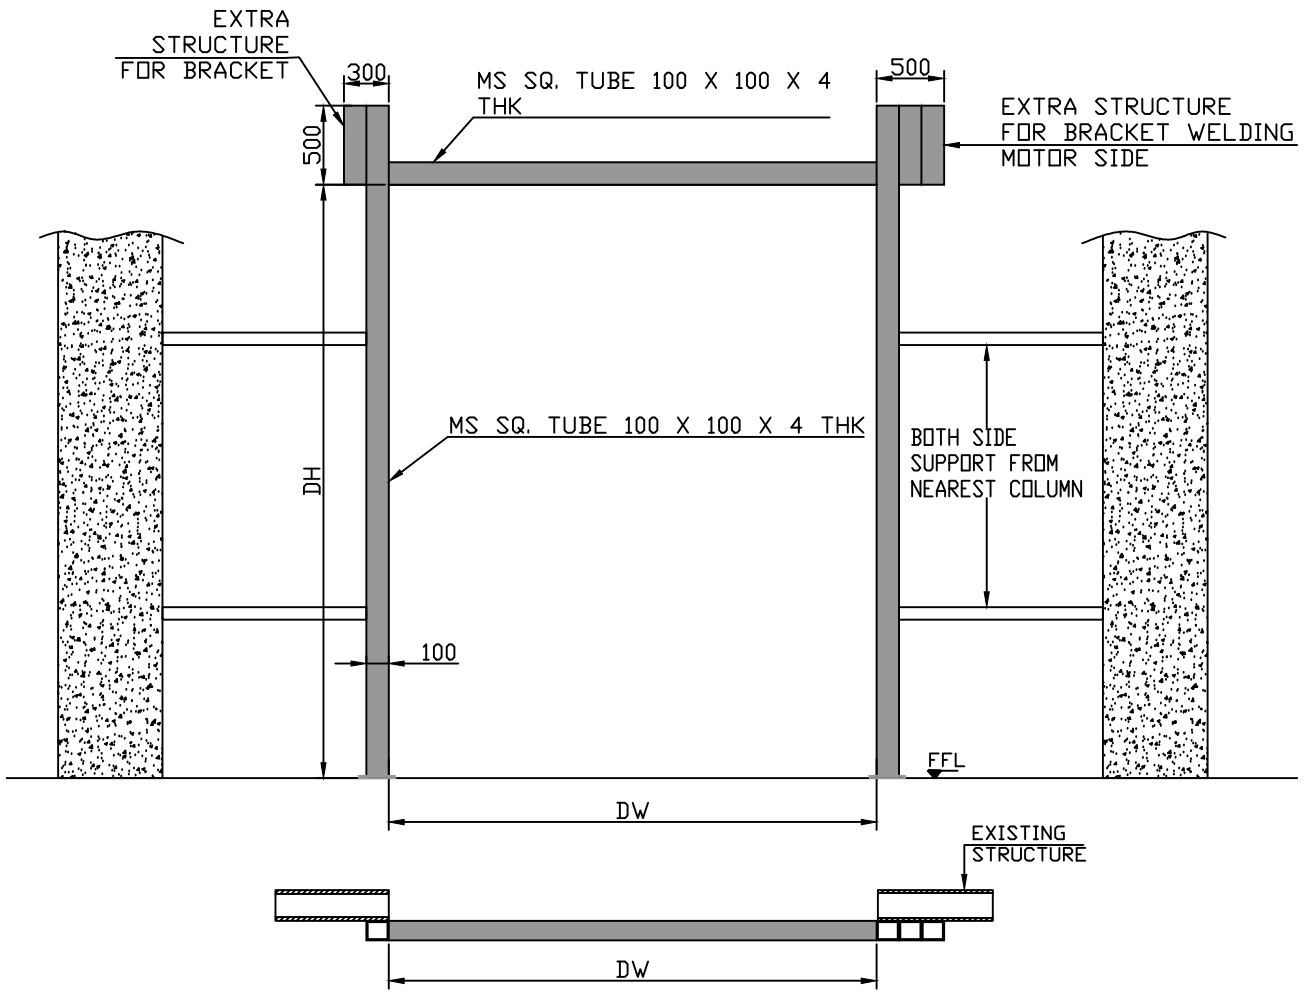


1	4500	4500	3
SR NO	DW	DH	QUANTITY
DOOR DIMENSION			

Tolerance ±3 mm (for all dimensions)

Dimensions in [ ] ==> clearance for installation

This drawing & design is the property of NIHVA TECHNOLOGIES. Not to be sold or copied to any other concern.

TITLE - RR300 PLUS ALU HSD STRUCTURE

NIHVA TECHNOLOGIES PVT. LTD.

NIHVA TECHNOLOGIES PVT. LTD. PUNE
Tel : 020 66304033
Email:- info@nihva.com
Website:- www.nihva.com

	NAME	SIGN	DATE
DRAWN	P.A		22.03.19
CHECK	V.T		22.03.19
APPROVED			

CLIENT - UNITED ARCHITECT

PROJECT - ESR

LOCATION - BHIWANDI

If any queries contact:sales@nihva.com

DWG. NO. -NIHVA/18-19/0302 REV- 0

ALL DIMENSION ARE IN mm

SCALE: NTS WT: SHEET:

NOTE-
1. ALL CIVIL WORK WILL BE CLIENT'S SCOPE.
2.STRUCTURE REQUIRED FOR SHUTTER IS IN CLIENT'S SCOPE.