
CONSTRUCTION NOTES:

1. ALL DIMENSIONS TO FACE OF MASONRY OR DRYWALL, U.N.O.
2. PROVIDE A CONTINUOUS 100W X 165H RC KERB TO THE PERIMETER OF ALL SLAB OPENINGS.
3. PROVIDE 250W X 1050H AFFL RC KERB DESIGNED TO WITHSTAND IMPACT FROM VEHICLES TO PERIMETER OF ALL RAMPS, AT ALL EXTERIOR WALL LOCATIONS AND AT THE EDGES OF ALL VOIDS. REFER TO ENGINEERS DRAWINGS FOR REINFORCEMENT DETAILS.
4. RC KERB HEIGHTS INDICATED ON THE DRAWINGS ARE MEASURED FROM ADJACENT SL.
5. THE PARTITION TYPE ABOVE DOORS IS TO MATCH THE ADJACENT PARTITION TO THE DOOR.
6. ALL SLAB PENETRATIONS WITHIN PLANT ROOMS TO BE FILLED WITH APPROVED FIRE STOPPING MATERIALS, AFTER THE INSTALLATION OF SERVICES.
7. THE FIRE RATING OF ALL FLOOR SLABS TO HAVE A MINIMUM FIRE RESISTANCE OF 2 HOURS. FLOOR CAVITY BARRIERS TO BE FIRE BARRIER ROCKWOOL SLAB WITH CLASS 0 FOIL "AIM" OR SIMILAR AS APPROVED BY THE ARCHITECT.
8. WHERE THE FIRE RATING OF WALLS IS NOTED ON THE DRAWING, THE FIRE RATING SHALL APPLY TO THE ENTIRE PERIMETER ENCLOSURE OF THE ROOM/SPACE AND FOR THE FULL HEIGHT OF THE AREAS BEING SEPARATED.
9. WHERE SERVICE ELEMENTS EG. PIPES, DUCTS, CONDUITS, CABLE TRAYS, ETC., PENETRATE FIRE RATED FLOOR SLABS AND WALLS, THE ELEMENTS SHALL BE INSTALLED IN A MANNER THAT PRESERVES THE INTEGRITY OF THE FIRE RATED ELEMENT BEING PENETRATED.
10. ALL WORK BY MC U.N.O.
11. FOR WALL TYPE SCHEDULE REFER TO A-610.
12. REFER TO MEP FOR PRESSURIZATION CUT-OUT SIZE REQUIRED FOR M-11. TOP OF CUT-OUT INSIDE STAIRCASE TO BE ALIGNED WITH TOP OF DOOR OPENING. REFER TO MEP FOR CUT-OUT HEIGHTS AT SERVICE VESTIBULE.

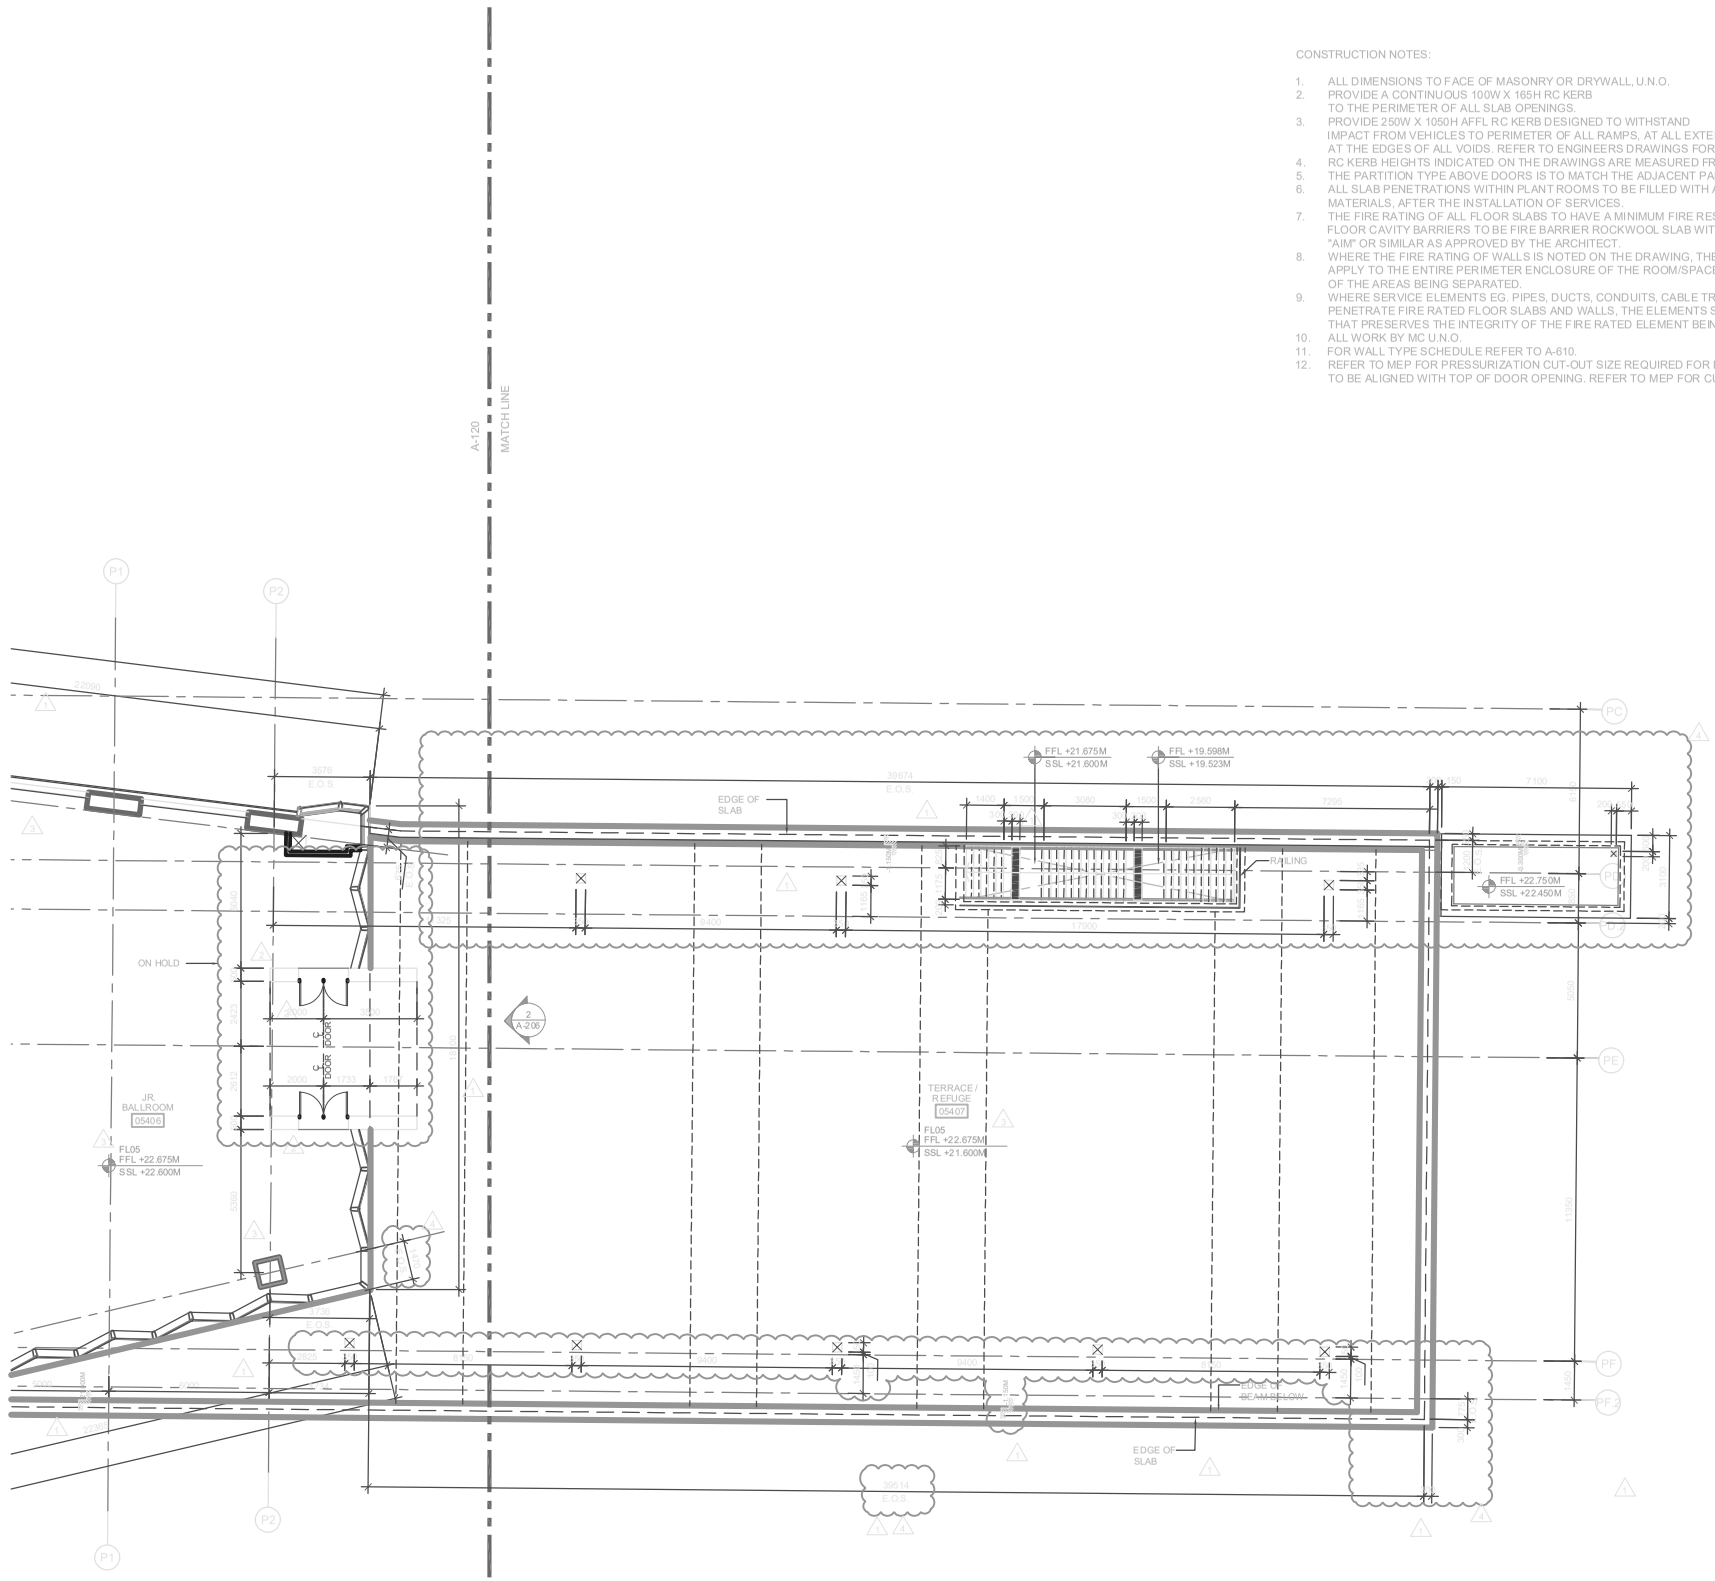

FLOOR	JR. BALLROOM SL	JR. BALLROOM FL	CORE SL	CORE FL
FLOOR 05	+22.600M	+22.675M	+22.600M	+22.675M

1 FLOOR 05
Scale: 1:100

WORLI
Mixed Use Project

Address
Dr. Annie Besant Rd.
Worli, Mumbai 400 030
India

Oasis Realty LH.jpg

Client and Architect of Record
Oberoi Realty Limited
Commerz, 3rd Floor, International Business Park,
Oberoi Garden City, Mumbai - 400 063 India
Tel: 91 22 6677 3333 Fax: 91 22 6677 3334

Design Architect
Kohn Pedersen Fox Associates PC
Architects & Planning Consultants
11 West 42nd Street
New York, NY 10036
Tel: 212.977.6500 Fax: 212.956.2526

Architectural Consultant
Aplusi Asia Pte Ltd
39 Robinson Road
#13-02/03 Robinson Point
Singapore 068911
Tel: +65.6538.2188 Fax: +65.6538.9188

Structural Engineers
Leslie E Robertson Associates
Consulting Engineers (India) PVT. LTD.
Ruby House, B Wing, 1st Floor
J.K. Sawant Marg
Dadar West, Mumbai - 400 028 India
Tel: 91 22 2437 6001 and 91 22 2437 6003

M/E/P Consultant
RED Engineering Middle East
Middle East, Office No. 1040-1404
Al Shafar Tower, Tecom C Area
PO Box 27793, Dubai, UAE
Tel.: +971(0)4.447.7281 Fax: +971.4.4477.253

Curtainwall Consultant
Meinhardt Facade Technology (S) Pte Ltd
168 Jalan Bukit Merah
#05-01 Surbana One
Singapore 150168
Tel: +65.6238.9730 Fax: +65.6736.1542

Parking Consultant
Walker Parking Consultants
20 Park Plaza, Suite 1202
New York, NY 10010
Tel: 518.441.9884 Fax: 212.288.2543

Vertical Transportation
Fortune Consultants, Ltd
82 West Ranch Trail
Morrison, CO 80465
Tel: 303.697.0382 Fax: 303.697.0382

Facade Maintenance
GMS Consultants
65 Bowes Avenue, Niddrie 3042
Melbourne, Australia
Tel: +61.3.8307.5351

4	COORDINATED ARCH DESIGN DEVT.	JUL.08.2011
3	COORDINATED ARCH DESIGN DEVT.	JUL.16.2011
2	COORDINATED ARCH DESIGN DEVT.	APR.11.2011
1	CW TENDER PACKAGE 1 & 4	FEB.28.2011
0	COORDINATED ARCH DESIGN DEVT.	FEB.17.2011
No.	Issue	Date

Key Plan

Date: JAN. 12, 2012
Scale: AS NOTED
Project No: 1848

TA - FL 05
MEETING ROOMS &
REFUGE PARTIAL PLAN

A-120.1

© 2010 KOHN PEDERSEN FOX ASSOCIATES PC All rights reserved.

Filename: D:\Vineet Lohana OneDrive Sync\OneDrive - Oberoi Realty Limited\Projects\Rbz-Hotel\Tower Allocoming\FL4 to 5 Staircase_from Dilip\OneDrive_2026-11-17\TA_FL05 STAIR TOP CAD FILE\A-120.1 TA-FL 05 MEETING ROOMS & REFUGE.dwg Plotted by: Vineet Lohana Plot Time: 1/22/2026 10:18 AM