



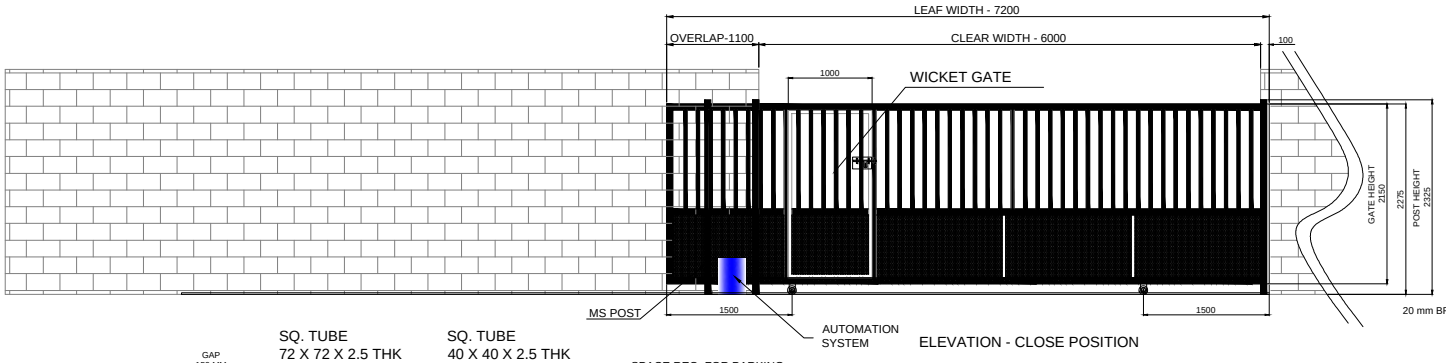


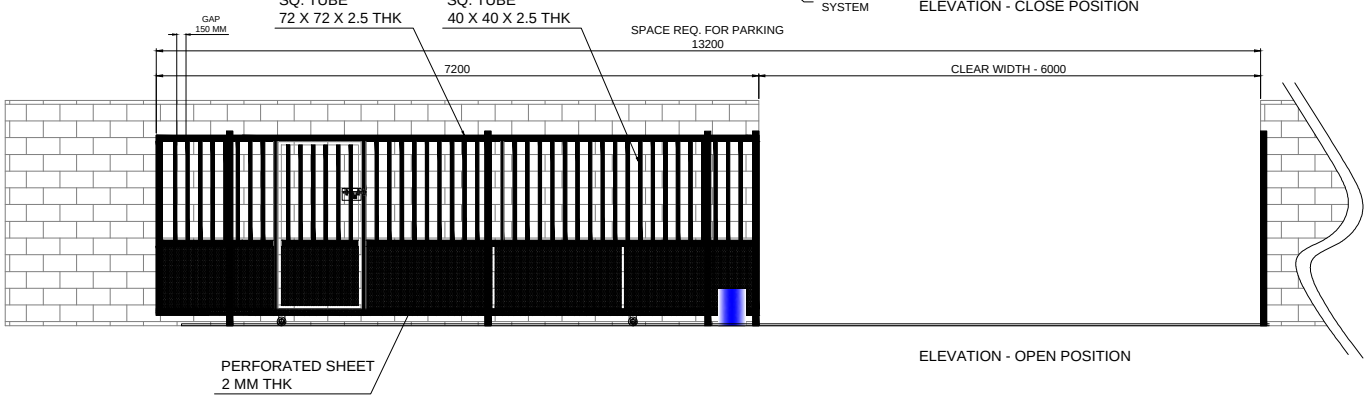

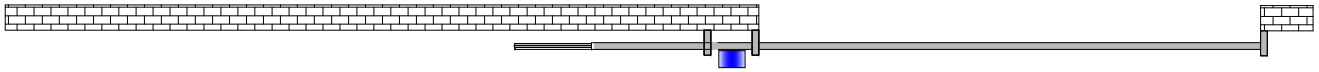

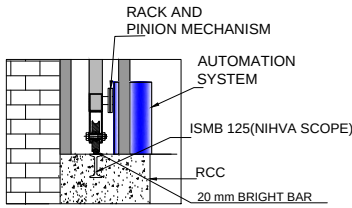

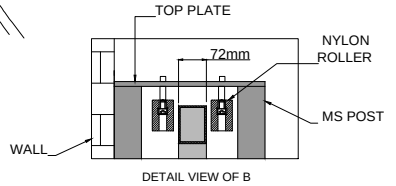

TOLERANCE - ±10mm

NOTE-
1. ALL REQUIRED CIVIL WORK WILL BE IN CLIENTS SCOPE.
2. ONE COAT OF RED OXIDE & TWO COAT OF APPROVED RAL SHADE WILL BE GIVEN TO THE GATE.
3. IF NECESSARY GATE LEAF WILL BE IN TWO PARTS FOR TRANSPORTATION & WILL BE WELD TOGETHER ON SITE.

SR.NO	RAL CODE	RAL COLOR
04	RAL 7035	LIGHT GREY
03	RAL 5002	ULTRAMARINE BLUE
02	RAL 9002	GREY WHITE
01	RAL 1004	GOLDEN YELLOW

This drawing & design is the property of NIHVA TECHNOLOGIES. Not to be sold or copied to any other concern.

TITLE: AUTOMATIC SINGLE LEAF SLIDING GATE

NIHVA TECHNOLOGIES PVT. LTD. PUNE
Tel : 020 66304033
Email:- info@nihva.com
Website:- www.nihva.com

	NAME	SIGN	DATE
DRAWN	P.V.A		16.02.19
CHECK	V.M.T		16.02.19
APPRD.			

CLIENT - CHEST RESEARCH FOUNDATION
PROJECT -
SITE LOCATION - KALYANI NAGAR, PUNE
If any queries contact : design@nihva.com
DWG. NO. : NIHVA/1 8-19/0275 REV- 0
ALL DIMENSION ARE IN mm
SCALE: NTS WT: SHEET: 01 OF 01