Abbrevation's:
WOW-Wall Opening Width
WOH-Wall Opening Height
CH- Clear Height
UC-Under Cut
FFL-Finished Floor Level

ASSESORIES DETALES

(a) HINGES: SS hinges 100x75x3mm


(b) LOCK : Panic Bar-Dorma single point latching PHA2000
Outer trim-Dorma for panic without cylinder PHT03

(c) DOOR CLOSER : TS68


(d) VISION PANEL- 5mm THK. FIRE GLASS SIZE- 200X300mm.


Shutter thickness : 47 mm
Frame Sheet thick : 1.20mm
Shutter sheet thick : 0.80mm
Fixing : On Soliid Brick plasterd wall with Anchors

NOTE:- *All Dimensions are in mm.
*Tolerance:-All Linear Dimensions ±3mm,Others ±0.5mm.
*The Drawing Is For Location of Hardware only. Drawing Does Not Represent The Hardware For More Clarity, Please Go Through Hardware Broucher.

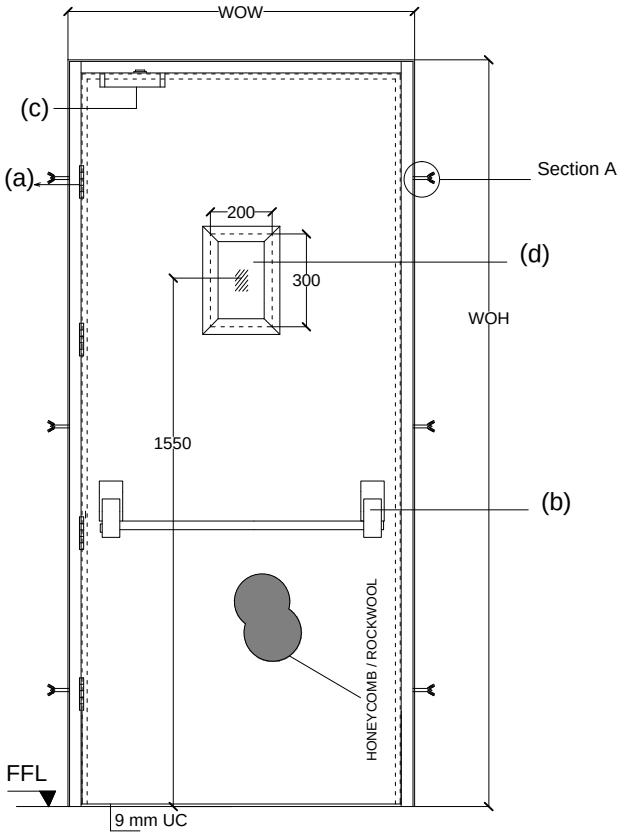

ELEVATION

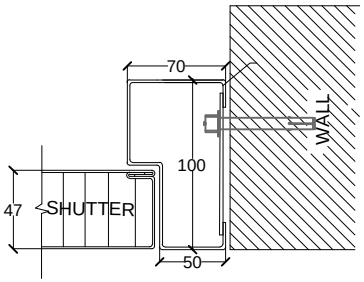

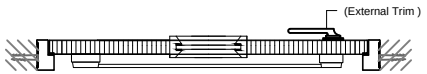

Top View

Fire door size						
WOW	WOH	TYPE 1	TYPE 2	TYPE 3	TYPE 4	QUANTITY
900	2100					2

NOTE- CLIENT SHOULD SELECT DOOR TYPE FROM DOOR HANDLING SHEET & COLOR OF DOOR.

This drawing & designing is the property of NIHVA TECHNOLOGIES. Not to be sold or copied to any other concern.

TITLE: SINGLE LEAF FIRE RATED DOORS

NIHVA TECHNOLOGIES PVT. LTD.
NIHVA TECHNOLOGIES PVT. LTD. PUNE
Tel : 020 66304033
Email:- info@nihva.com
Website:- www.nihva.com

	SIGN	DATE
DRAWN	SURAJ	15/10/17
CHECK	SHEKHAR	15/10/17
REV.	00	
APPROVAL	SHEKHAR	15/10/17

If any queries contact : projects@nihva.com

ALL DIMENSION ARE IN mm

CLIENT - FERRERO INDIA PVT. LTD
PROJECT -
SITE - BARAMATI.
DWG. NO. : NIHVA/17-18/0244
SCALE: NTS | WT: | SHEET: 01 OF 01