



Sr.No	Description	(Length) MM	Qty.
1.	MS Req. tube (40x80x3mm)	7060	02
2.	MS Req. tube (40x80x3mm)	5000	02
3.	MS Req. tube (40x80x3mm)	6980	02
4.	MS Req. tube (40x80x2mm)	1614	13
5.	Flat slat	1614	402
6.	Cladding sheet(7060x150x1.6mm)		01
7.	Bottom Wheel (Ø100)		03
8.	Handle		01
9.	Tower bolt		01

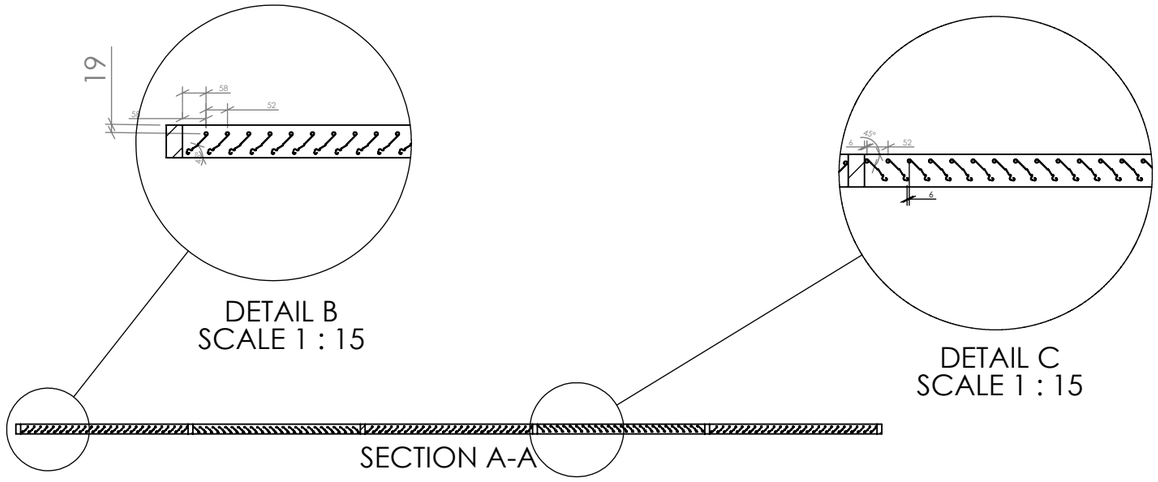

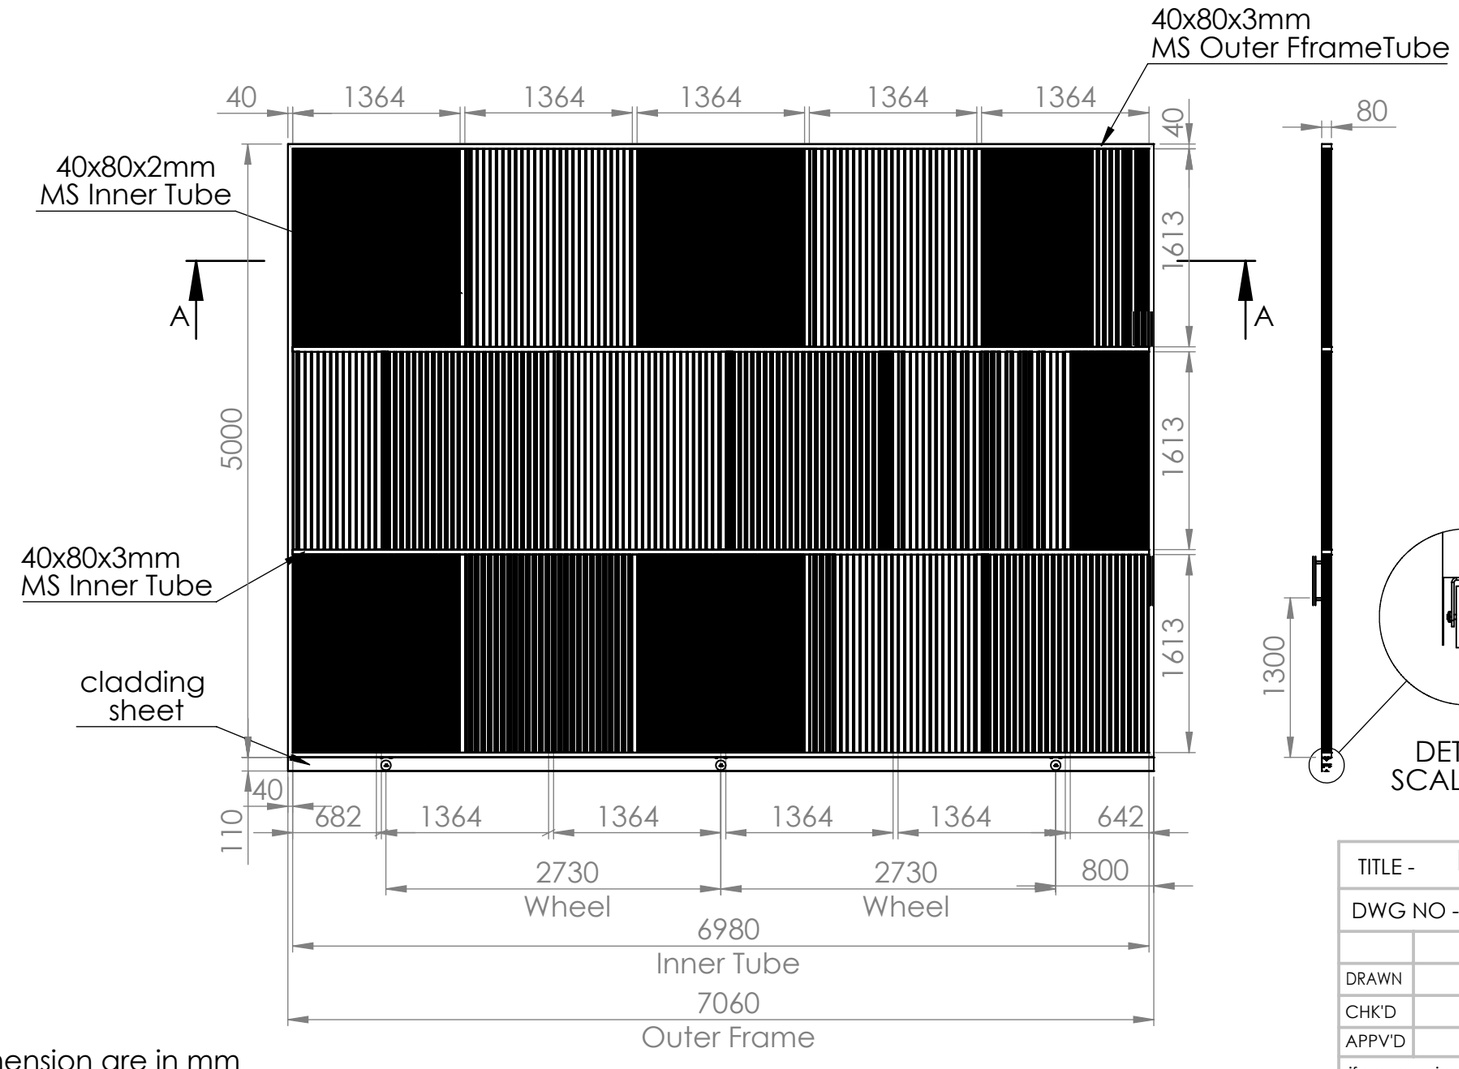

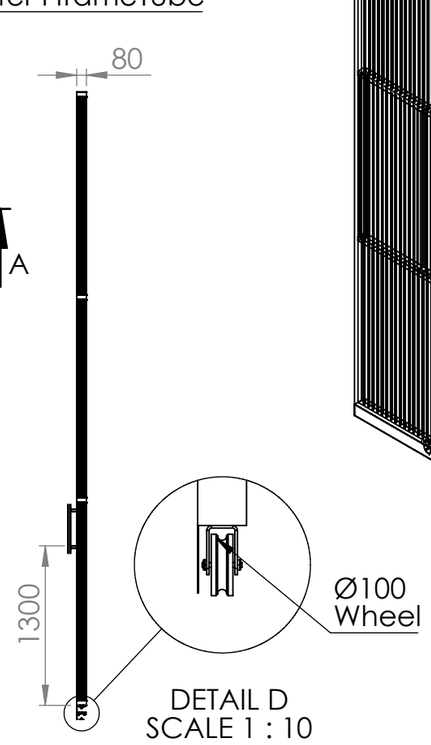

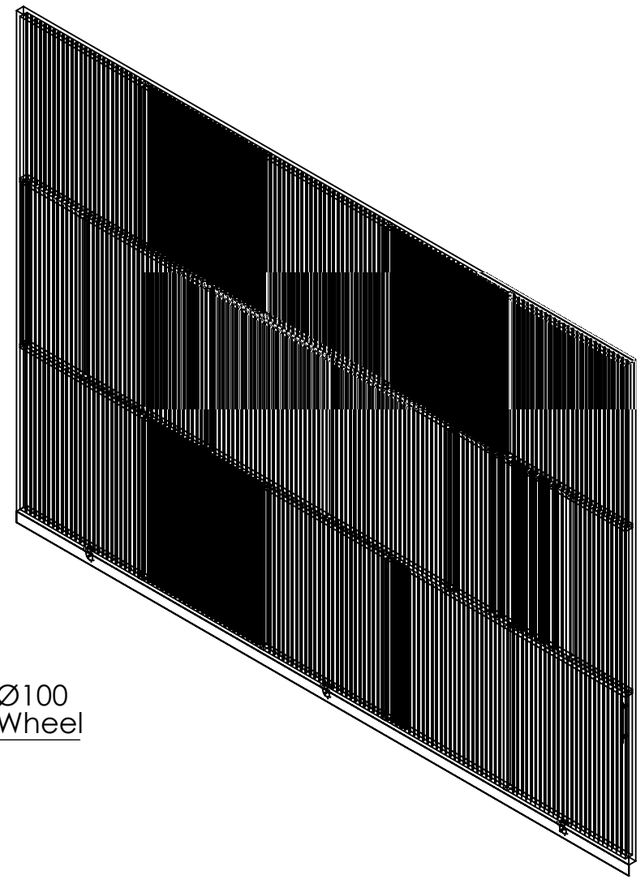

Note:-
1.All dimension are in mm
2.Slat direction purpose refer this drawing no (NIHVA_24-25_PCH_2409001)

TITLE - Fix screen leaf (7060)				NIHVA TECHNOLOGIES PVT.LTD.PUNE
DWG NO - PCH-240901001			QTY - 01	Website - www.nihva.com
	NAME	SIGNATURE	DATE	CLIENT - Panchshil
DRAWN	S.J		26.09.2024	PRODUCT - Fix screen leaf (7060)
CHK'D	B.B		27.09.2024	SITE LOCATION - Pune
APPV'D	V.T.		27.09.2024	
if any queries contact - service@nihva.com				REVISION -
ALL DIMENSION ARE IN mm			A3	SCALE - SHEET 1 OF 1