

2440.00
OVERLLAPPING DISTANCE

A

9640.00
LENGTH OF LEAF

B

C


SQ MS TUBE
40*40*4MM THK

7200.00
CLEAR OPENING

SLINDING DIRECTION


2440.00
HEIGHT OF LEAF

RECT MS TUBE
100*50*5MM THK

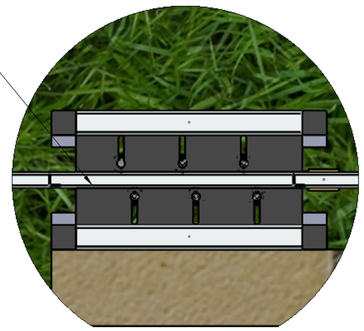


DETAIL B
SCALE 1 : 10

POST NO 2 &
NYLON BEARING ASM

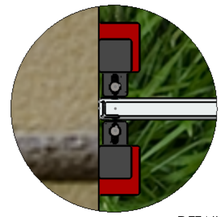


DETAIL A
SCALE 2 : 15

POST NO 1 &
NYLON BEARING ASM

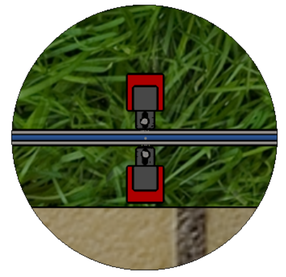

DETAIL C
SCALE 1 : 10

POST NO 3 &
NYLON BEARING ASM

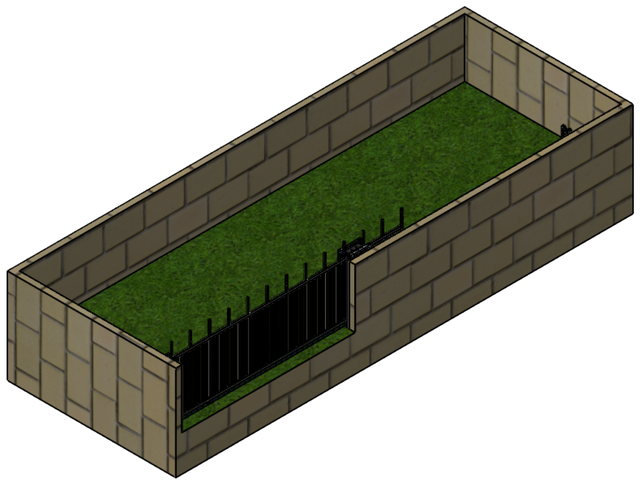

TYPE 05

SINGLE SLIDING GATE

UNLESS OTHERWISE SPECIFIED: DIMENSIONS ARE IN MILLIMETERS SURFACE FINISH: TOLERANCES: LINEAR: ANGULAR:		FINISH:		DEBURR AND BREAK SHARP EDGES		DO NOT SCALE DRAWING	REVISION
	NAME	SIGNATURE	DATE			TITLE:	
DRAWN							
CHK'D							
APPV'D							
MFG							
Q.A				MATERIAL:		DWG NO.	
						GA DRAWING TYPE 05	
				WEIGHT:		SCALE:1:100	SHEET 1 OF 1