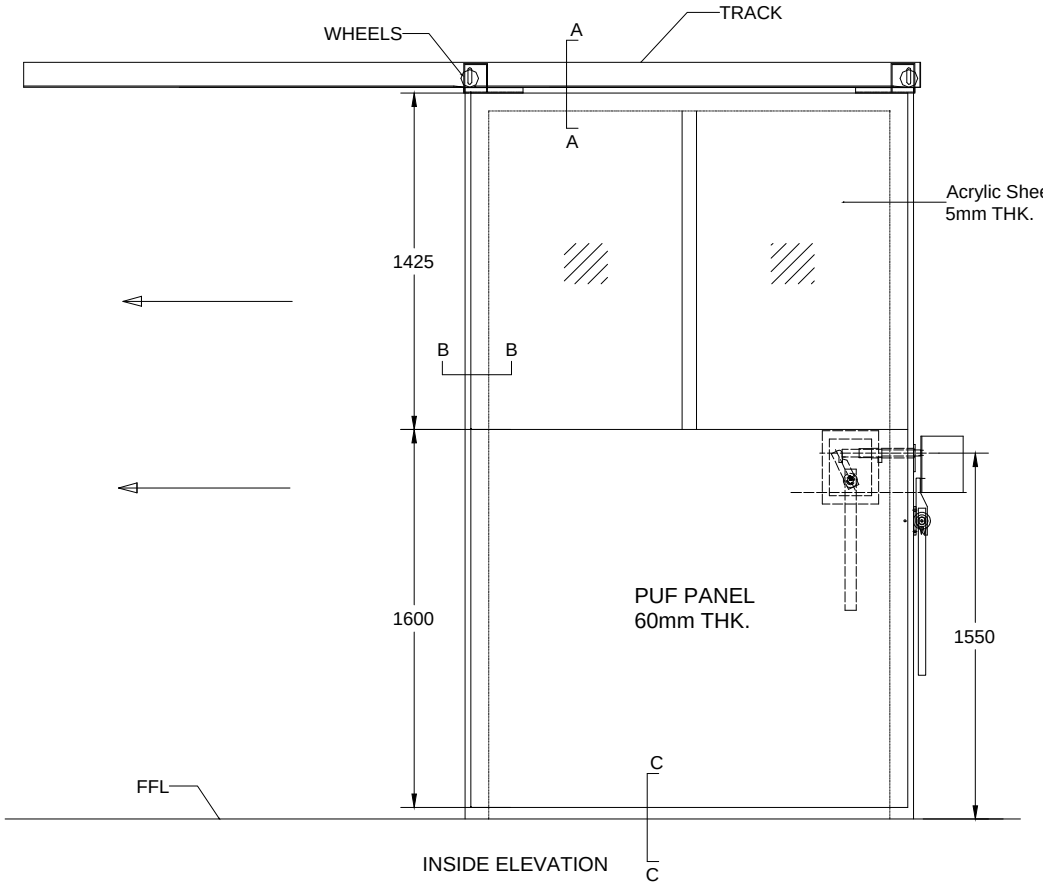

INSIDE ELEVATION

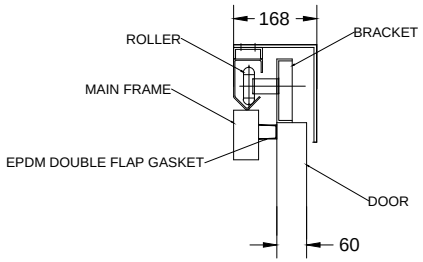

SECTION 'AA'

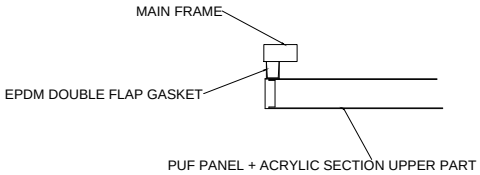

SECTION 'BB'

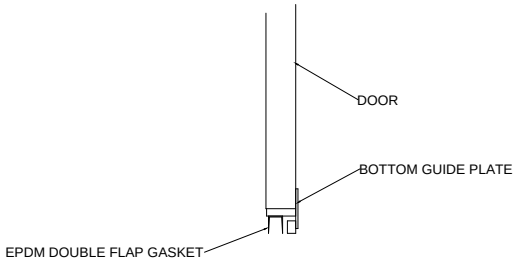

SECTION 'CC'

CLEAR WIDTH	CLEAR HEIGHT	QUANTITY
1700	3000	01

DOOR TYPE- L.H.S

REVISION 1- DETAILED SECTIONS DRAWN AS PER REQUEST.

COLOR OF DOOR - RAL 9002(GREY WHITE)

This drawing & design is the property of NIHVA TECHNOLOGIES. Not to be sold or copied to any other concern.

TITLE: SLIDING DOOR

NIHVA TECHNOLOGIES PVT. LTD.
NIHVA TECHNOLOGIES PVT. LTD. PUNE
Tel : 020 66304033
Email:- info@nihva.com
Website:- www.nihva.com

	SIGN	DATE
DRAWN	OMKAR	23/09/17
CHECK	SHEKHAR	23/09/17
REV.		
APPROVAL	SHEKHAR	23/09/17

If any queries contact : projects@nihva.com

ALL DIMENSION ARE IN mm

CLIENT -PACKTIME INNOVATION PVT.LTD.

PROJECT -

SITE - CHAKAN

DWG. NO. : NIHVA/17-18/0197/R01

SCALE: NTS | WT: | SHEET: 01 OF 01