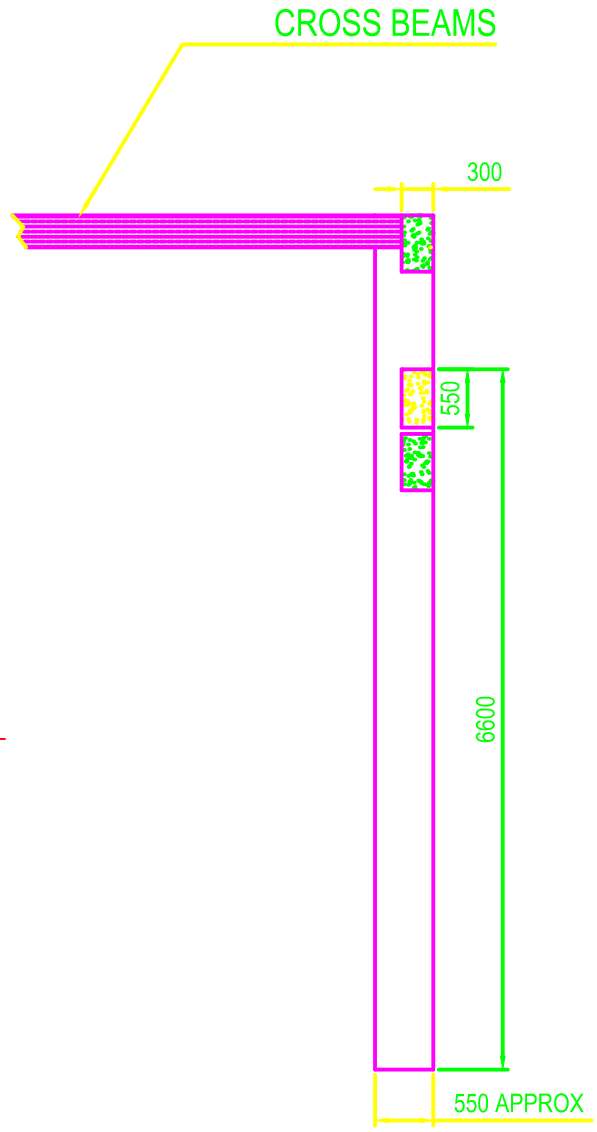
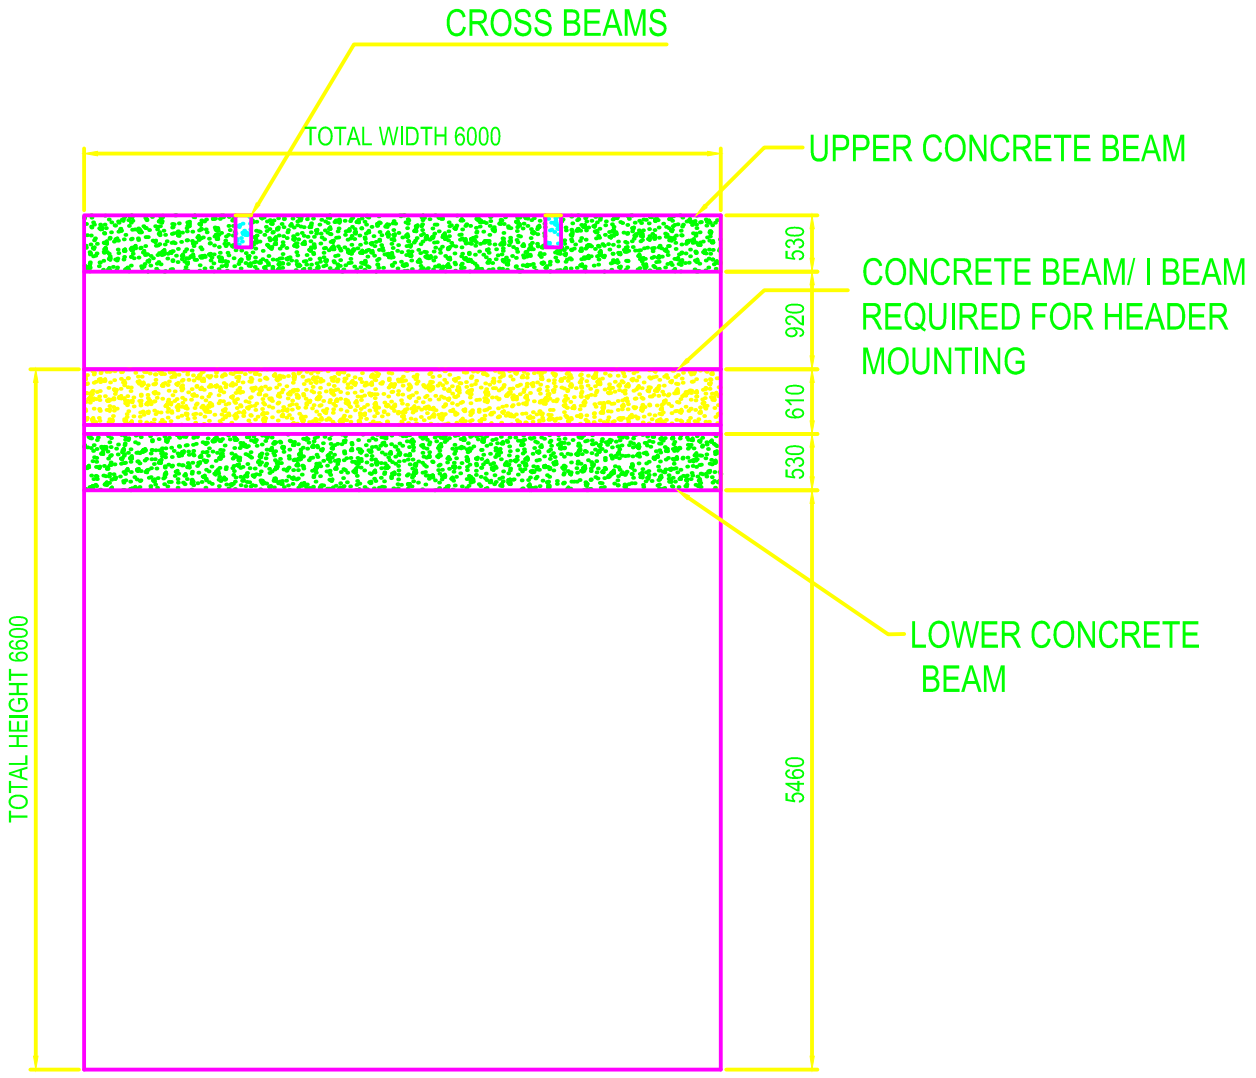



BEAM STRUCTURE AT SITE TERMINAL 4

OLD BUILDING : ARFF 4
CLEAR OPENING : 5400 X 6000
QTY : 4 NOS

R01 : BEAM POSITION CHANGED FROM 6900 TO 6600 MM.

This drawing & design is the property of NIHVA TFC-NOIDCIFS. Not to be sold or copied to any other person

| TITLE | | | | |
|---|---|---|---|---|
| MEGA DOOR 5400 X 6000 (ARFF4) | | | | NIHVA TECHNOLOGIES PVT. LTD. |
| | NAME | SIGN | DATE | |
| DRAWN | G.P. | | 21.08.2021 | CLIENT -DIAL- L&T |
| CHECK | A.K. | | 21.08.2021 | LOCATION - DELHI |
| APPRD. | V.T. | | 21.08.2021 | PRODUCT - MEGA DOOR - 5400 X 6000 |
| If any queries contact : design@nihva.com | | | | NIHVA\20-21\0216 / REV- 01 |
| ALL DIMENSION ARE IN mm | | | | SCALE: NTS / SHEET: 01 OF 02 |

NIHVA TECHNOLOGIES PVT. LTD. PUNE
Tel : 020 66304033
Email:- info@nihva.com
Website:- www.nihva.com

This document is the property of ASSA ABLOY Entrance Systems AB and shall not be reproduced or disclosed to any third party or used for any other unauthorized purpose.