



DRAWING


REV DESCRIPTION	DATE	REV NO
	05-06-2026	REV 00
1.		

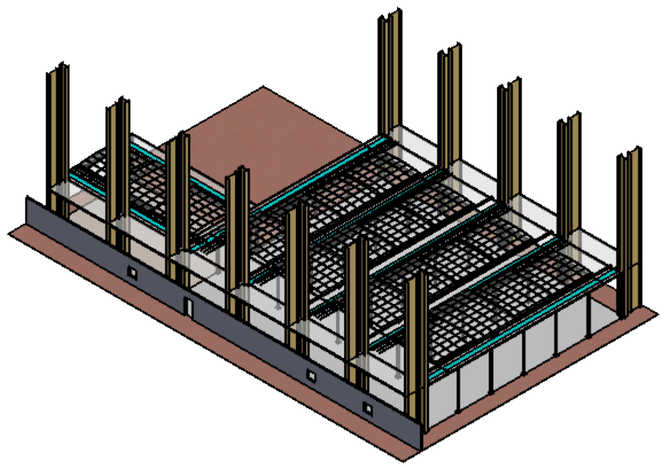


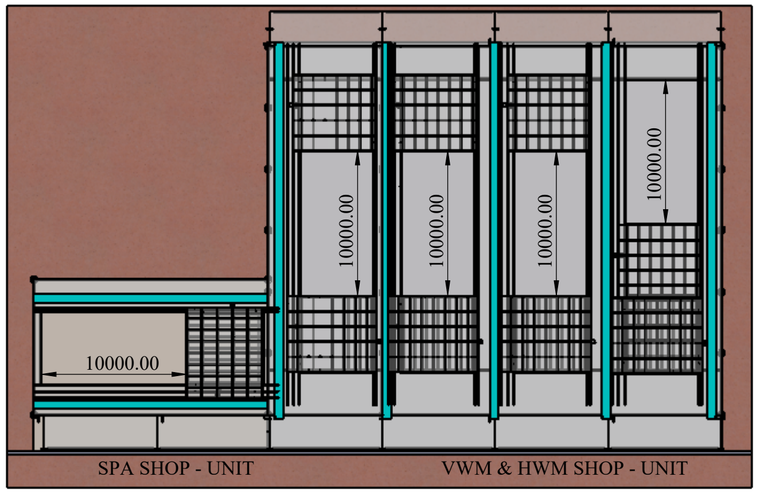


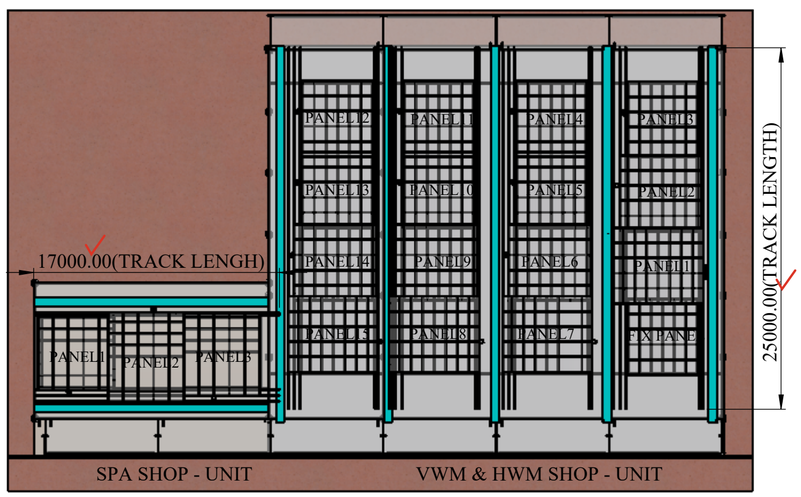

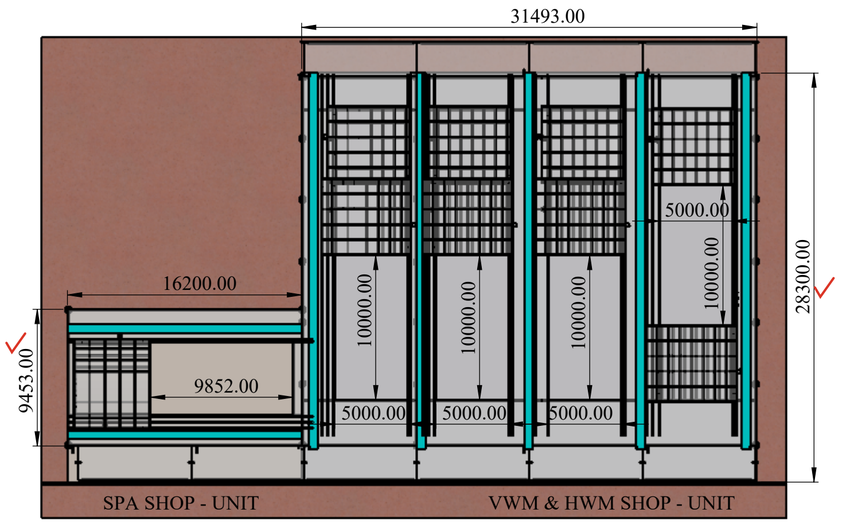

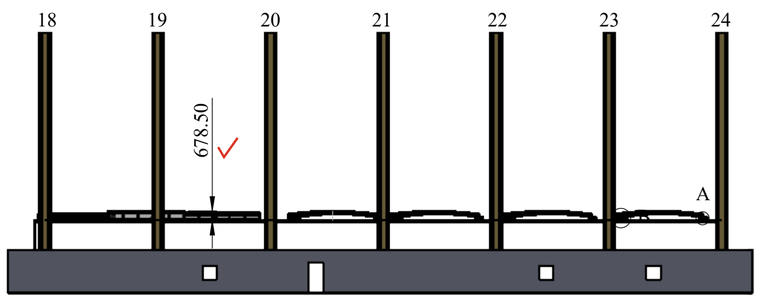

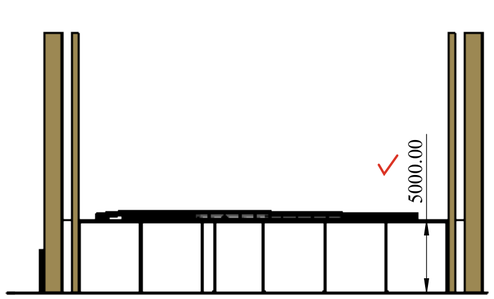

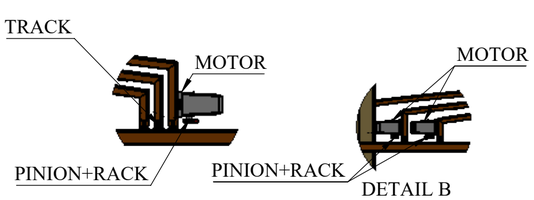

DETAIL A
SCALE 1 : 30

DETAIL B
SCALE 1 : 50

NOTE :


SPECIAL INSTRUCTION'S :

This drawing & design is the property of NIHVA TECHONOLOGIES PVT. LTD. Not to be sold or copied to any other concern

TITLE - ROOF AUTOMATION				NIHVA Technologies Pvt. Ltd.	NIHVA TECHNOLOGIES PVT.LTD.PUNE Website - www.nihva.com
DWG NO - NTPL-000-PM-001				PRODUCT - RETRACTABLE ROOF	
	NAME	SIGNATURE	DATE		
DRAWN	V.W.		05-06-2026	PROJECT NO - NTPL-000-PM	REVISION - 00
CHK'D	S.P.		06-06-2026	SITE LOCATION -	WEIGHT -
APPV'D	V.T.		06-06-2026	MATRIAL -	QTY - 1
If any queries contact - info@nihva.com				PROJECTION METHOD:	SCALE :
ALL DIMENSION ARE IN mm			A2		SHEET 1 OF 2

DRAWING

REV DESCRIPTION	DATE	REV NO
	05-06-2026	REV 00
1.		

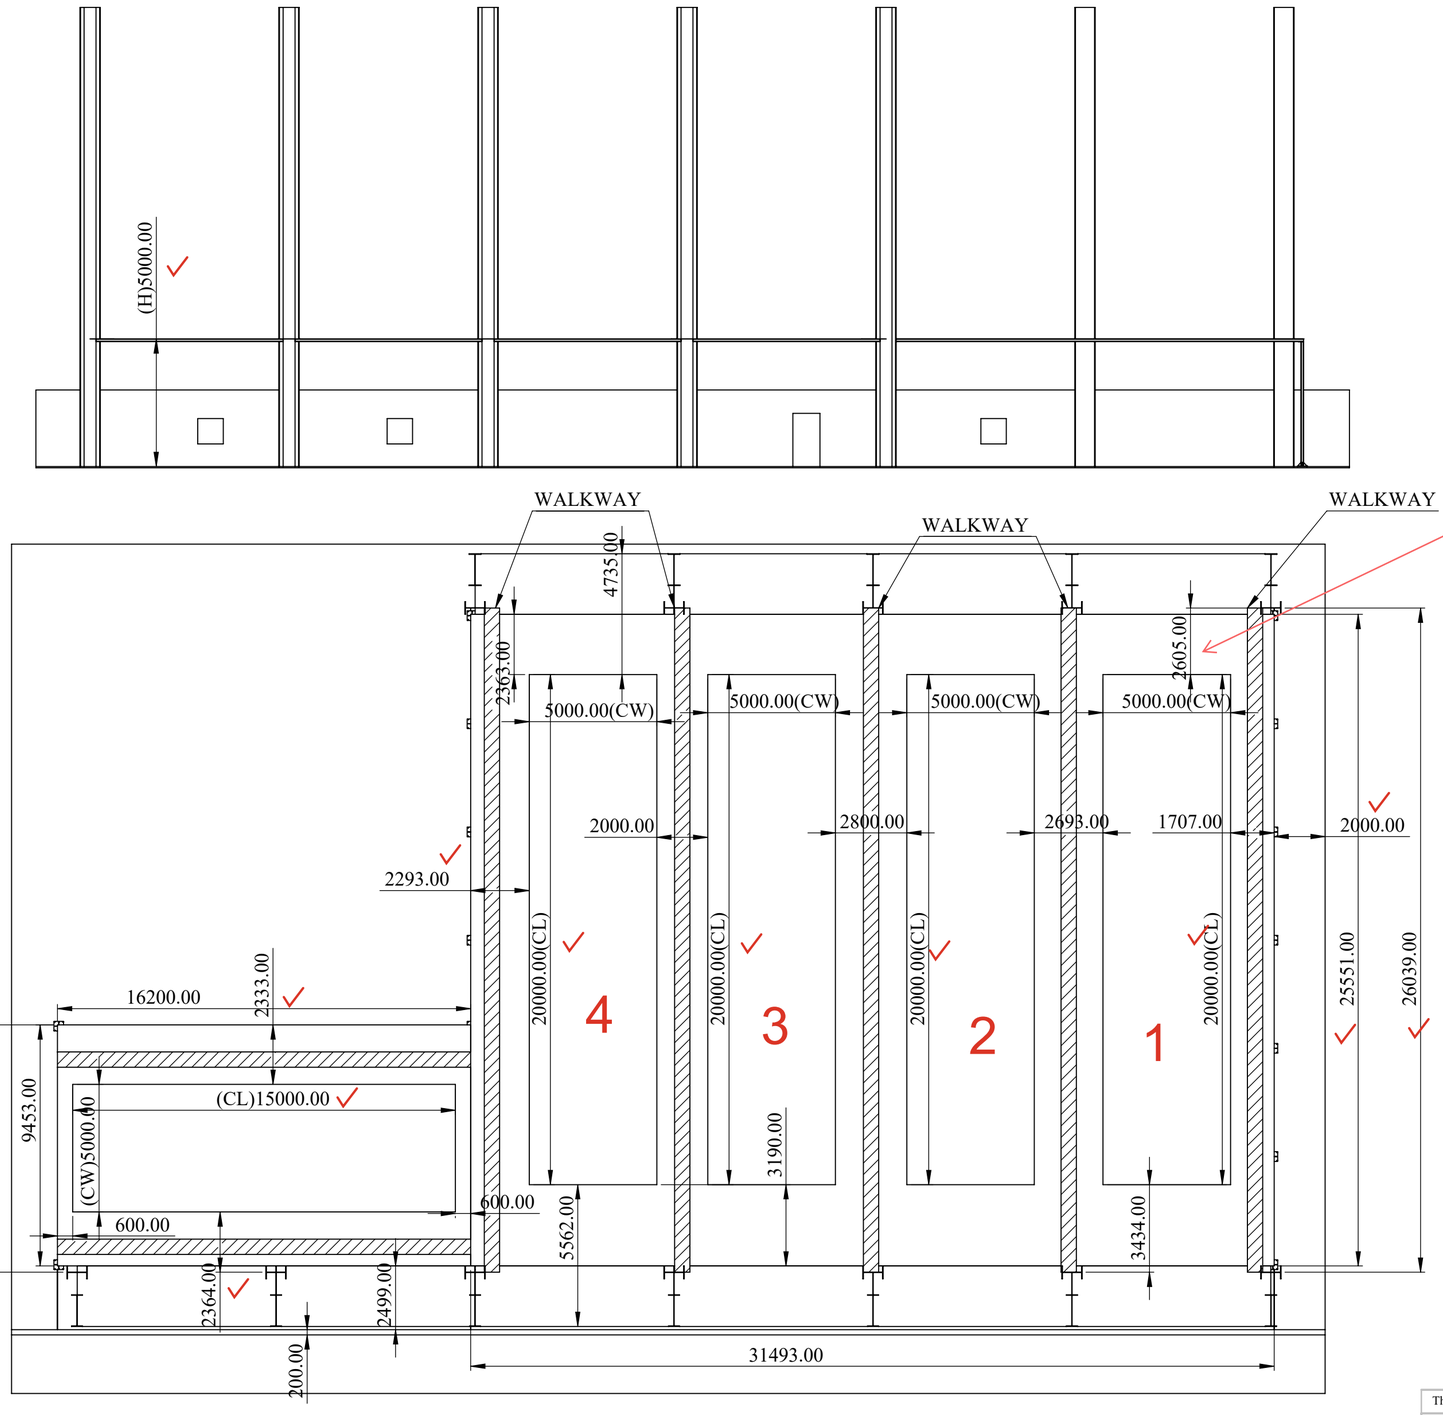

for row **1** area only this will be changed to improve the ground accessibility

NOTE :

BASE STRUCTURE IN CLIENT SCOPE

SPECIAL INSTRUCTION'S :

This drawing & design is the property of NIHVA TECHONOLOGIES PVT. LTD. Not to be sold or copied to any other concern

TITLE - ROOF AUTOMATION

DWG NO - NTPL-000-PM-001

NIHVA Technologies Pvt. Ltd.

NIHVA TECHNOLOGIES PVT.LTD.PUNE
Website - www.nihva.com

	NAME	SIGNATURE	DATE		
DRAWN	V.W.		05-06-2026	PRODUCT - RETRACTABLE ROOF	
CHK'D	S.P.		06-06-2026	PROJECT NO - NTPL-000-PM	REVISION - 00
APPV'D	V.T.		06-06-2026	SITE LOCATION -	WEIGHT -
				MATRIAL -	QTY - 1

If any queries contact - info@nihva.com

ALL DIMENSION ARE IN mm | A2

PROJECTION METHOD:

SCALE :