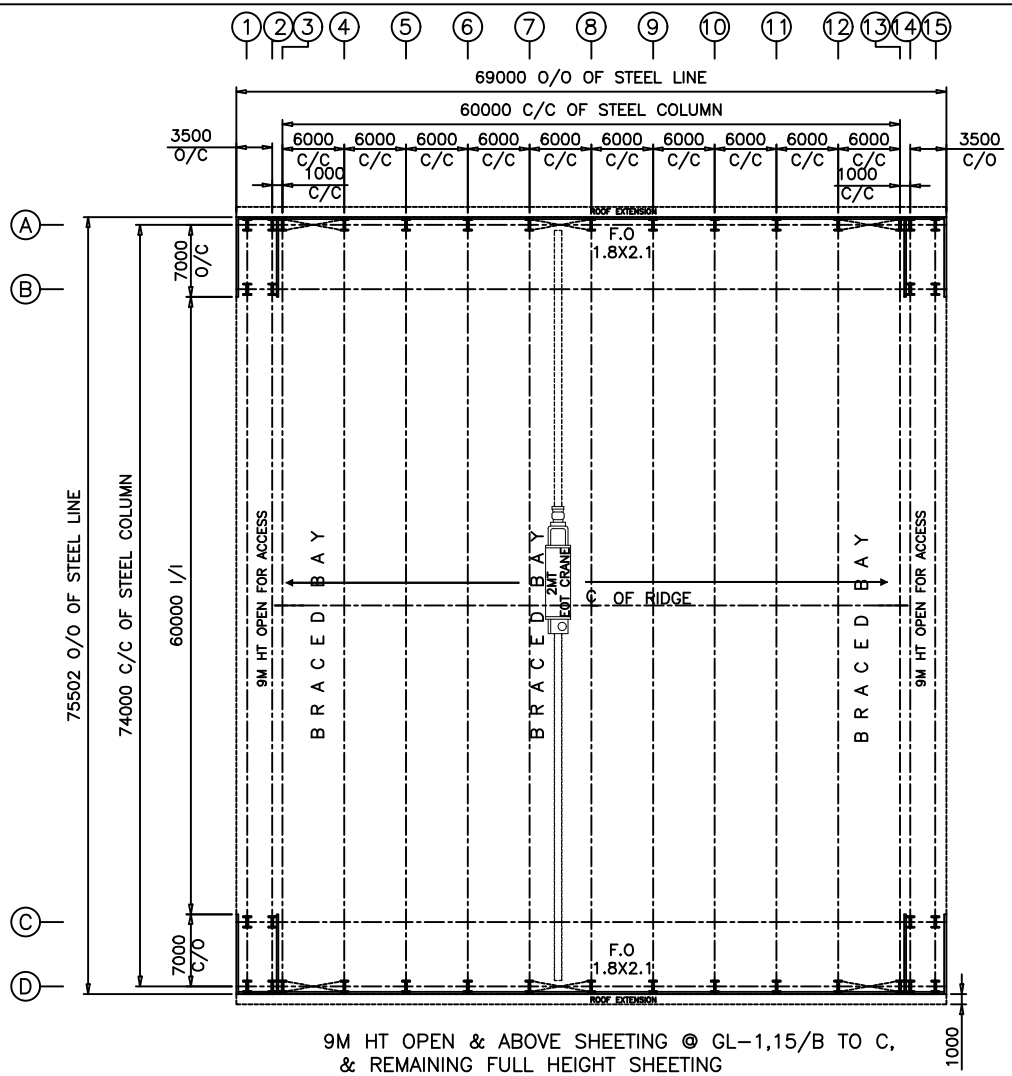




9M HT OPEN & ABOVE SHEETING @ GL–1,15/B TO C,
& REMAINING FULL HEIGHT SHEETING

## PROPOSED PLAN
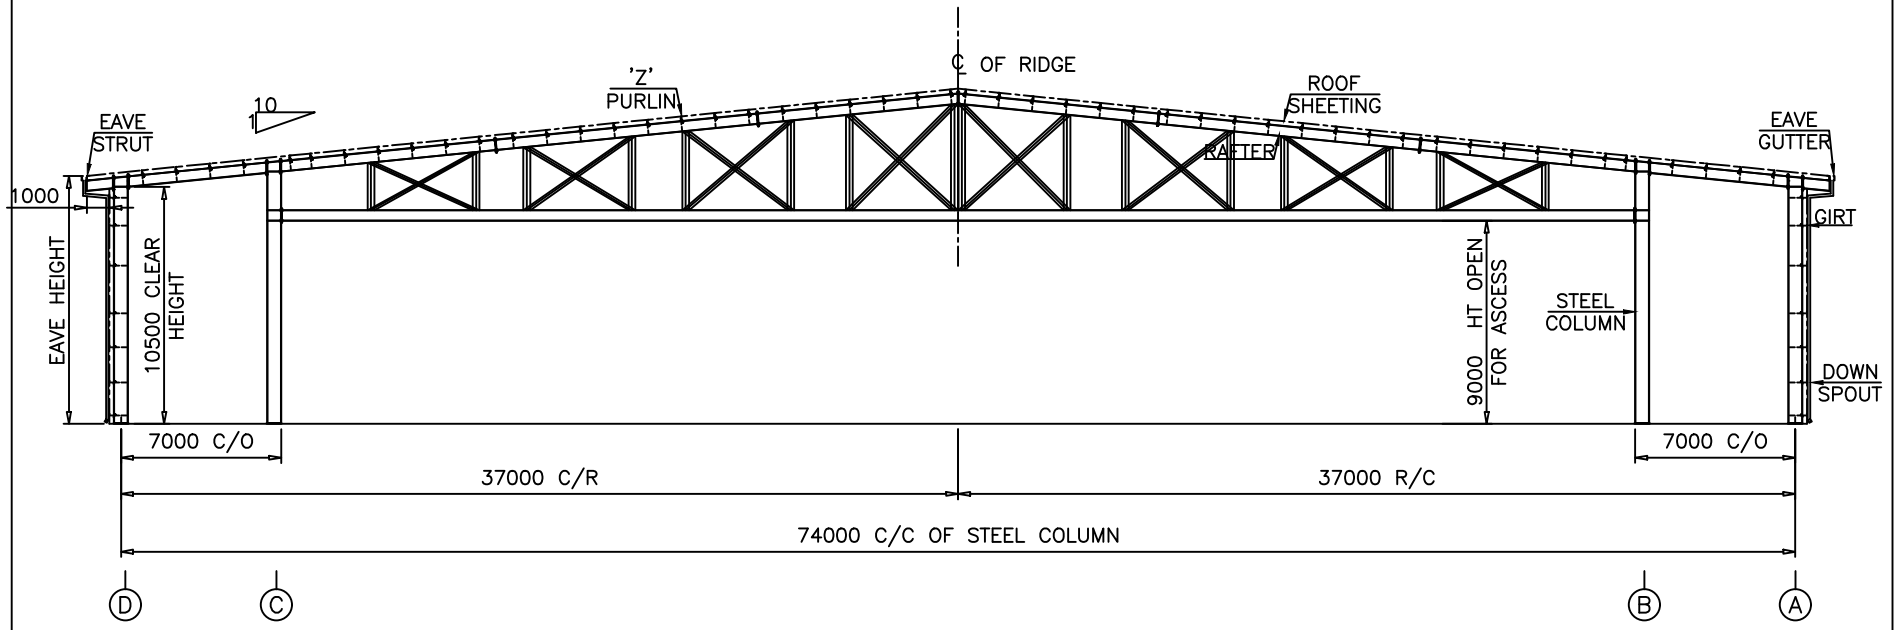
| | |
|---|---|
| WIND SPEED | 39 m/s |
| SEISMIC ZONE | III |
| ROOF LIVE LOAD | 0.75KN/m2 |
| MINIMUM THICKNESS<br>BUILTUP MEMBER<br>COLDFORM MEMBER | <br>6MM<br>2.5MM |
| DESIGN | IS:800–2007 |


PARAMOUNT STEEL

| | | | | | |
|---|---|---|---|---|---|
| CUSTOMER NAME | AIRCRAFT HANGAR | REVISION | 01 | TITLE | PROPOSED PLAN |
| | | DATE | --- | QUOTE NO | PSSL–24–020 |
| PROJECT NAME | ---- | JOB LOCATION | SULUR | DWG NO | PS–01 |





## CROSS SECTION @ GL – 1,2 & 14,15.
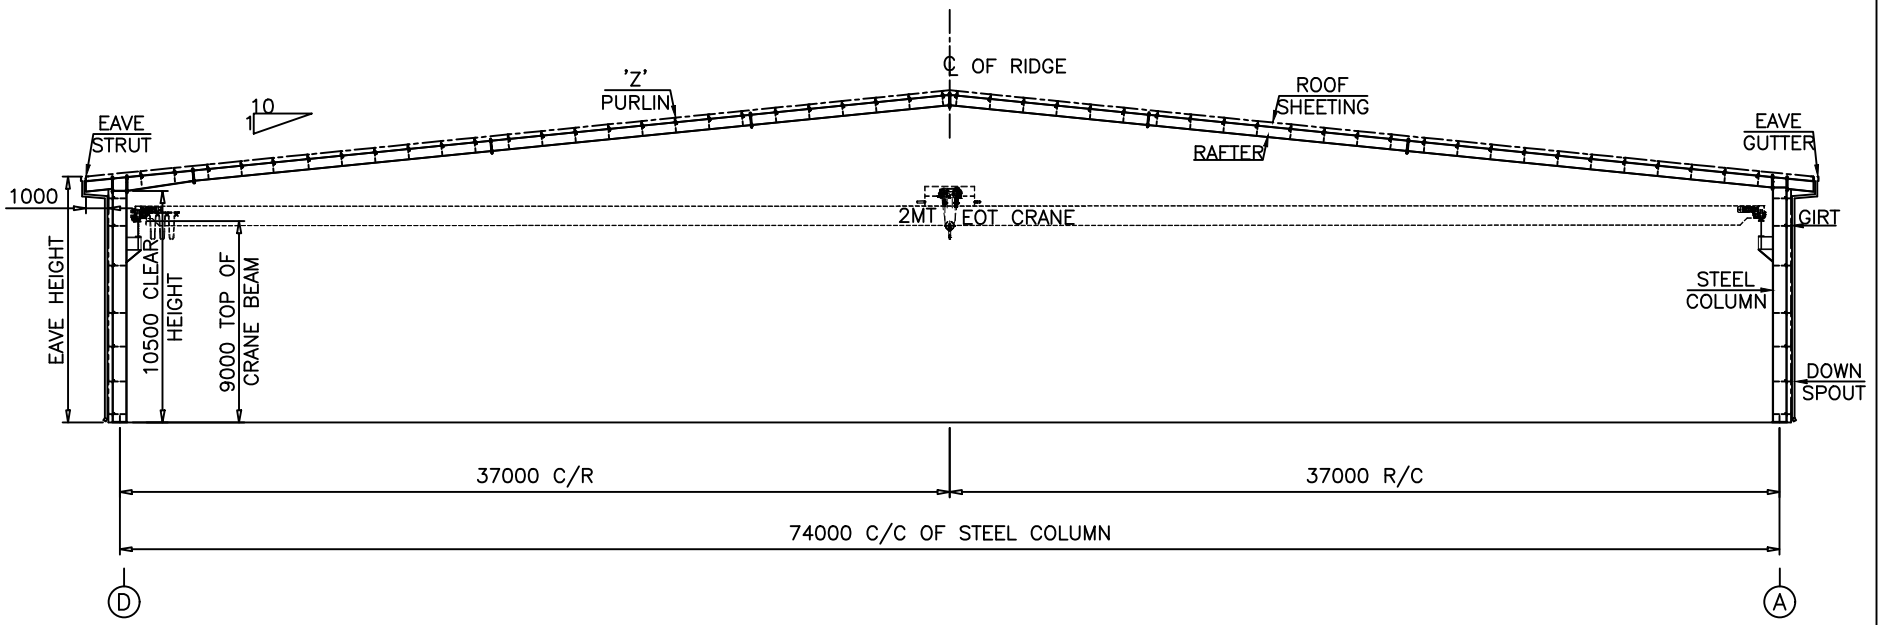
| | | | | | | |
|---|---|---|---|---|---|---|
| PARAMOUNT STEEL | CUSTOMER NAME | AIRCRAFT HANGAR | REVISION | 01 | TITLE | CROSS SECTION |
| | | | DATE | --- | QUOTE NO | PSSL–24–020 |
| | PROJECT NAME | ---- | JOB LOCATION | SULUR | DWG NO | PS–02 |





## CROSS SECTION @ GL – 3 TO 14.
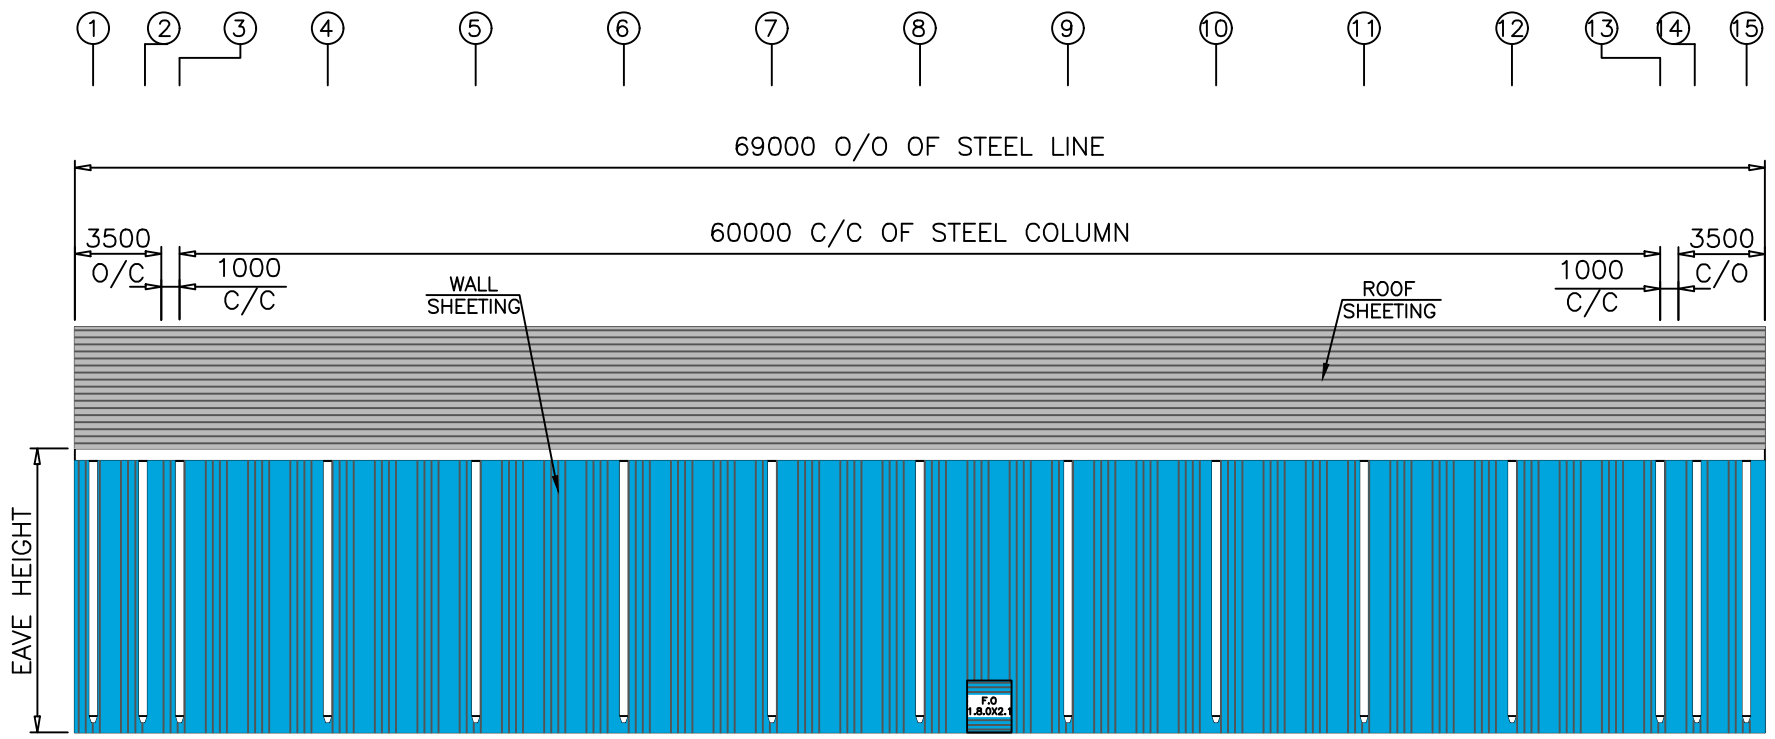
| | | | | | | |
|---|---|---|---|---|---|---|
| PARAMOUNT STEEL | CUSTOMER NAME | AIRCRAFT HANGAR | REVISION | 01 | TITLE | CROSS SECTION |
| | | | DATE | --- | QUOTE NO | PSSL–24–020 |
| | PROJECT NAME | ---- | JOB LOCATION | SULUR | DWG NO | PS–03 |





SIDEWALL ELEVATION @ GL – D & A(MIRROR).

| | | | | | | |
|---|---|---|---|---|---|---|
| PARAMOUNT STEEL | CUSTOMER NAME | AIRCRAFT HANGAR | REVISION | 01 | TITLE | SIDE WALL ELEVATION |
| | | | DATE | --- | QUOTE NO | PSSL–24–020 |
| | PROJECT NAME | ---- | JOB LOCATION | SULUR | DWG NO | PS–04 |

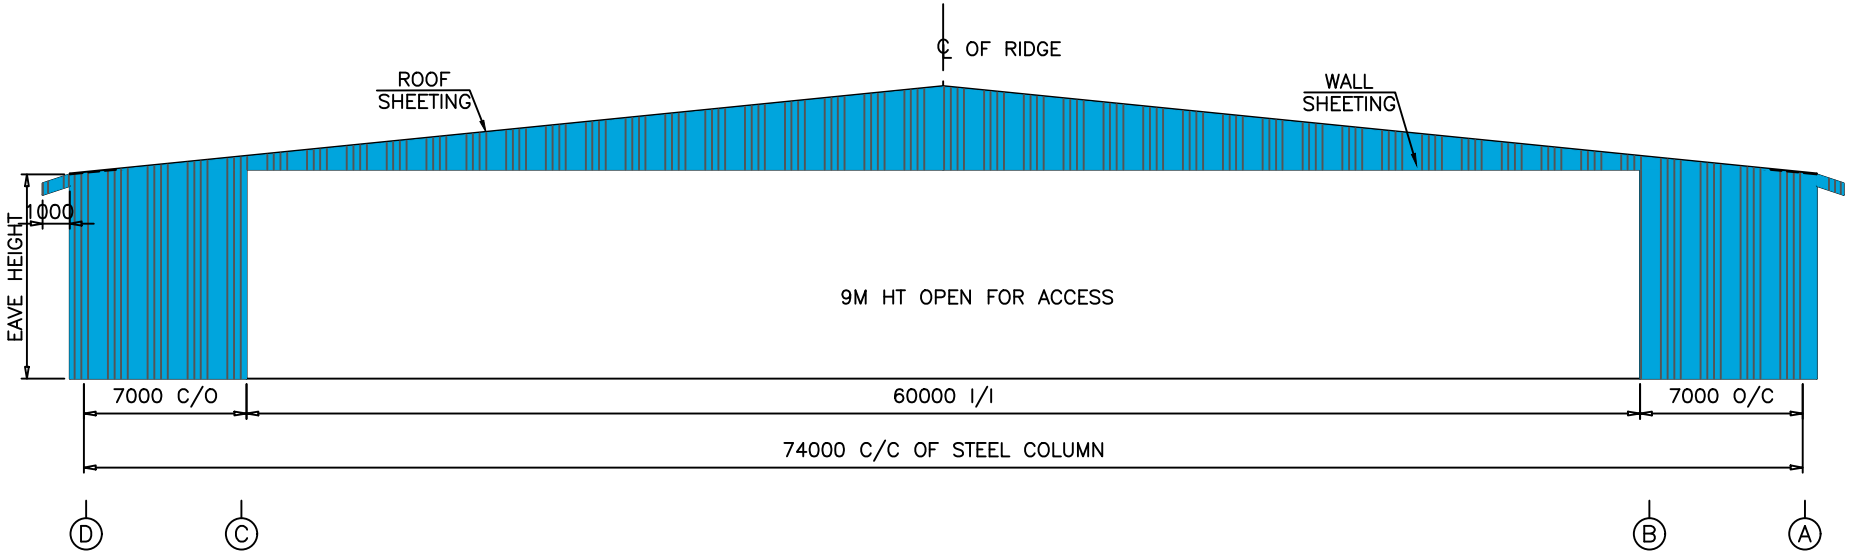


# ENDWALL ELEVATION @ GL – 15 & 1(MIRROR)
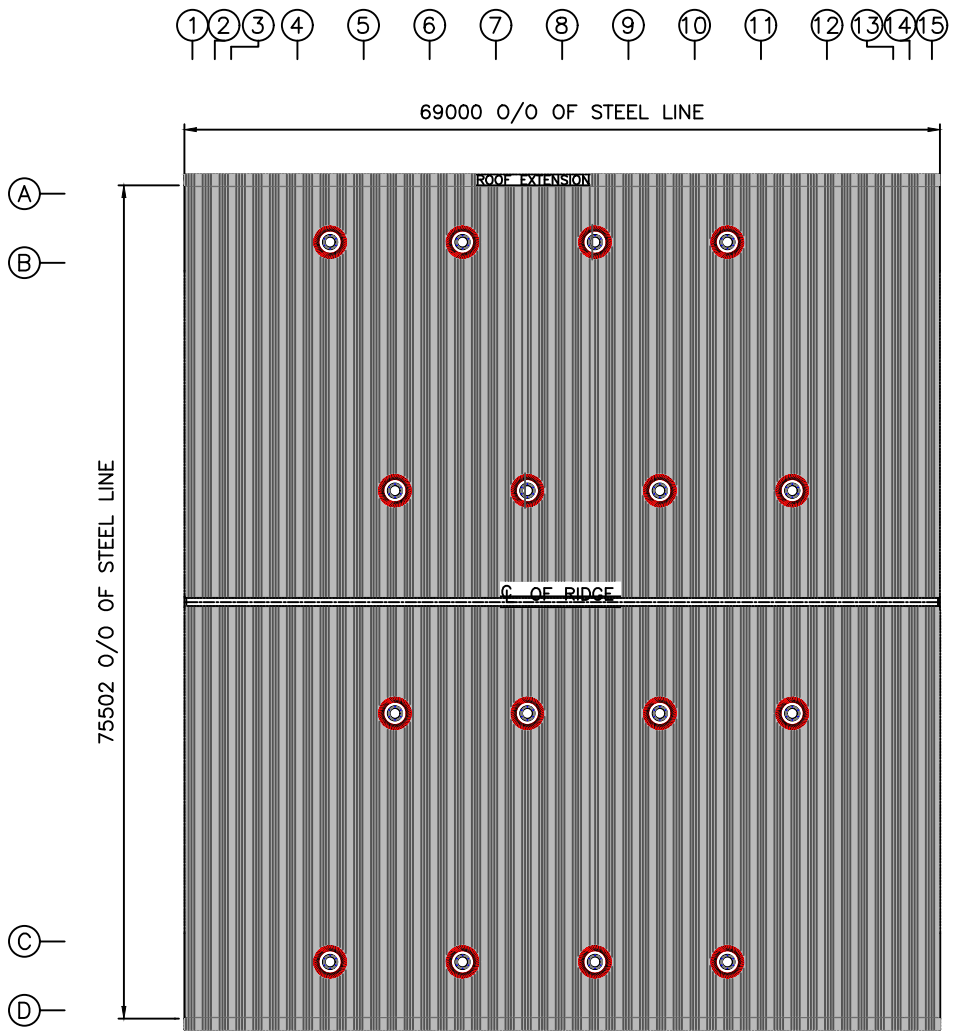
| | | | | | | |
|---|---|---|---|---|---|---|
| PARAMOUNT STEEL | CUSTOMER NAME | AIRCRAFT HANGAR | REVISION | 01 | TITLE | END WALL ELEVATION |
| | | | DATE | --- | QUOTE NO | PSSL–23–020 |
| | PROJECT NAME | ---- | JOB LOCATION | SULUR | DWG NO | PS–05 |




## ROOF PLAN

| | |
|---|---|
| TURBOVENTS | 16 NO'S |

PARAMOUNT STEEL

| | | | | | |
|---|---|---|---|---|---|
| CUSTOMER NAME | AIRCRAFT HANGER | REVISION | 01 | TITLE | ROOF PLAN |
| | | DATE | --- | QUOTE NO | PSSL-24-020 |
| PROJECT NAME | ---- | JOB LOCATION | SULUR | DWG NO | PS-06 |