

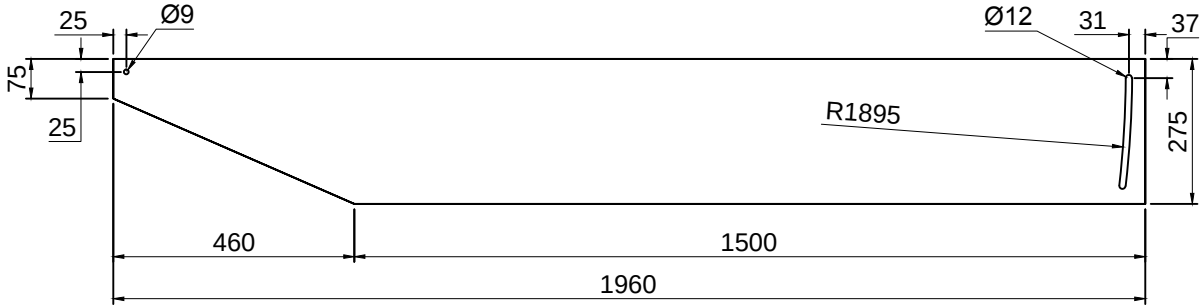



9

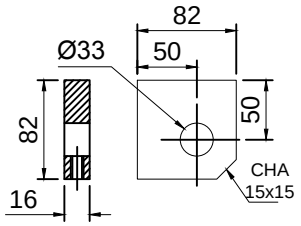

4

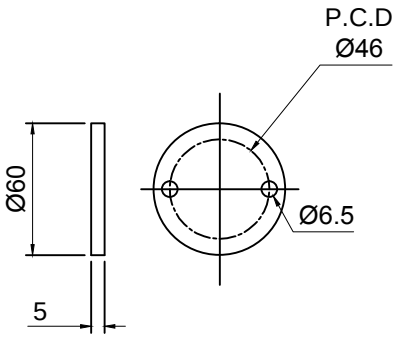

14

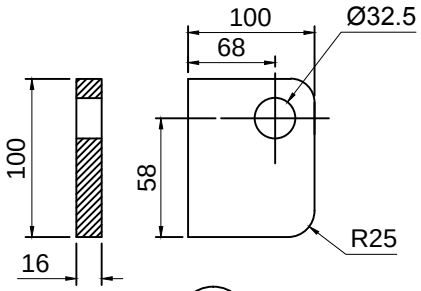

12

This drawing & design is the property of NIHVA TECHNOLOGIES. Not to be sold or copied to any other concern.

TITLE				
DECK DETAILS				NIHVA TECHNOLOGIES PVT. LTD. PUNE Tel : 020 66304033 Email:- info@nihva.com Website:- www.nihva.com
	NAME	SIGN	DATE	
DRAWN	P.V.A		20.06.2019	CLIENT -
CHECK	V.M.T		20.06.2019	PROJECT - NDL451
APPRD.				SITE LOCATION -
If any queries contact : design@nihva.com				DWG. NO. : NIHVA/19-20/VDR/075
ALL DIMENSION ARE IN mm				SCALE: NTS / WT: / REV- 00