Weitergabe sowie Vervielfältigung dieses Dokuments, Verwertung und Mitteilung seines Inhalts sind nur nach vorheriger ausdrücklicher schriftlicher Zustimmung von SMS Meer GmbH gestattet. Das Dokument ist vor unberechtigtem Zugriff Dritter zu schützen. Zuwiderhandlungen verpflichten zu Schadensersatz. Alle Rechte aus Patent-/Gebrauchsmuster-/Markenschutz vorbehalten.

GATE

GATE WITH MECH. LOCKING DEVICE

GATE WITH ELECT. LOCKING DEVICE

DOOR WITH MECH. LOCKING DEVICE

DOOR WITH ELECT. LOCKING DEVICE

DOOR

DOOR WITH MECH. LOCKING DEVICE

DOOR WITH ELECT. LOCKING DEVICE

▨ DANGER ZONE 1
No access while unit is in operation.

▨ DANGER ZONE 2
Access only to qualified and authorized persons possible
in defined operating states.
High Residual Risks
Note safety instructions in operating and maintenance manual.

▨ DANGER ZONE 3
Access only to qualified and authorized persons possible
in defined operating states.
Low Residual Risks
Note safety instructions in operating and maintenance manual.

▨ DANGER ZONE 4
Permanente working place:
Unrestricted access possible while unit is in operation.
Note general safety instructions.

▨ WORKING PLACE
Part of no access zone, that can be entered by trained operators
under particular conditions only
Note safety instructions in operating and maintenance manual.

REQUEST-/ ACKNOWLEDGEMENT BUTTON

EMERGENCY STOP

ACKNOWLEDGEMENT BUTTON

ESCAPE ROUTES

RAILING

REMOVABLE RAILING

FENCE

REMOVABLE FENCE

REMOVABLE CHAIN

LIGHT CURTAIN

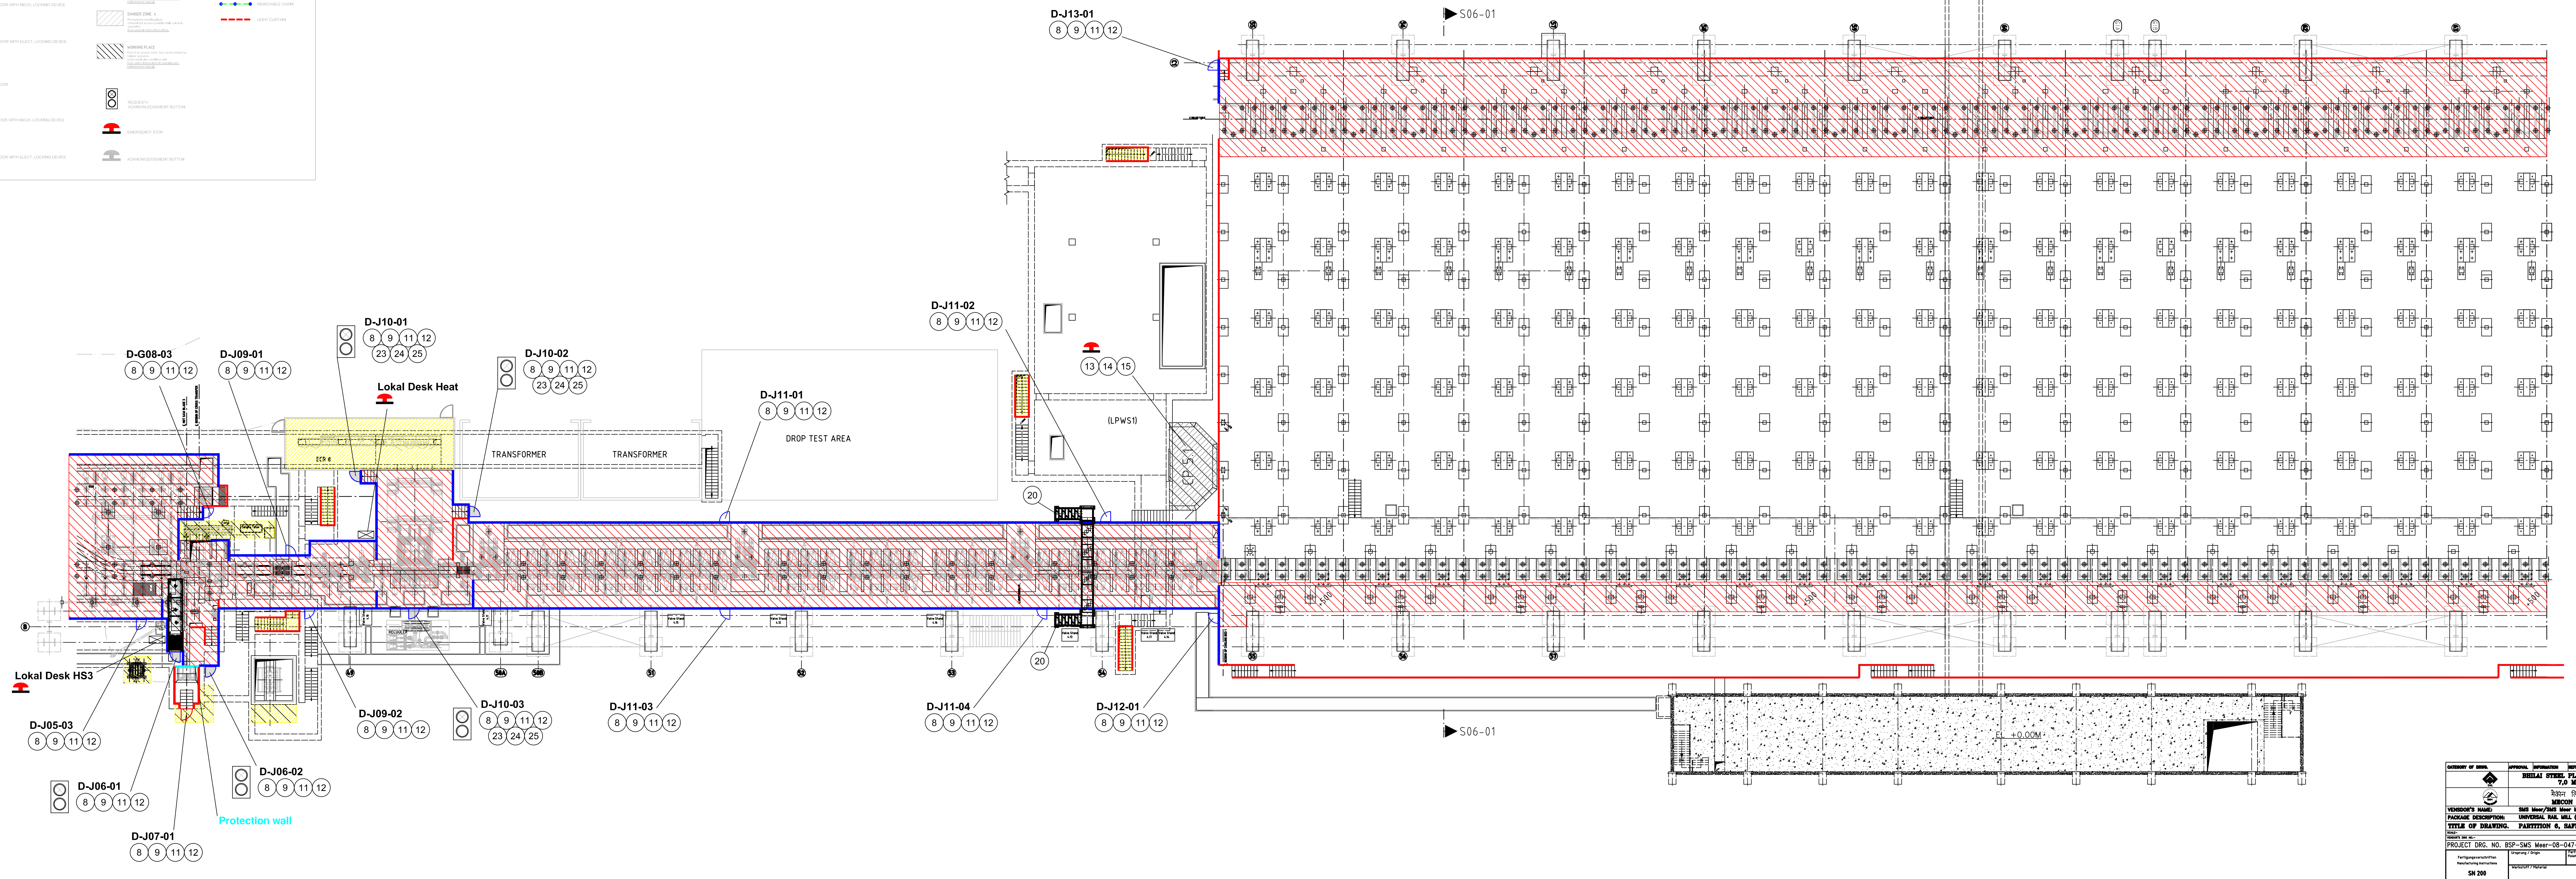
D-J13-01
8 9 11 12
S06-01
D-J11-02
8 9 11 12
13 14 15
(LPWS1)
D-J10-01
8 9 11 12
23 24 25
D-G08-03
8 9 11 12
D-J09-01
8 9 11 12
Lokal Desk Heat
D-J10-02
8 9 11 12
23 24 25
D-J11-01
8 9 11 12
DROP TEST AREA
TRANSFORMER
TRANSFORMER
20
20
Lokal Desk HS3
D-J05-03
8 9 11 12
D-J06-01
8 9 11 12
D-J07-01
8 9 11 12
Protection wall
D-J06-02
8 9 11 12
D-J09-02
8 9 11 12
D-J10-03
8 9 11 12
23 24 25
D-J11-03
8 9 11 12
D-J11-04
8 9 11 12
D-J12-01
8 9 11 12
S06-01
±0.00M

9463 0000 / RAILBHIL

CATEGORY OF DRWG.	APPROVAL	INFORMATION	REFERENCE	RECORD	CONSTRUCTION

BHILAI STEEL PLANT, BHILAI, CHATTISGARH
7,0 MTPA EXPANSION

मेकॉन लिमिटेड
MECON LIMITED

VENSDOR'S NAME: SMS Meer/SMS Meer India/ABB
PACKAGE DESCRIPTION: UNIVERSAL RAIL MILL (Pkg No-047)
TITLE OF DRAWING. PARTITION 6, SAFETY LAYOUT
SCALE-
VENDOR'S DRG NO.-
PROJECT DRG. NO. BSP-SMS Meer-08-047-21-130-35-BE-06654 REV. -

Fertigungsvorschriften
Manufacturing Instructions
SN 200

Ursprung / Origin
Fertiggewicht
Finished weight
kg
Werkstoff / Material
Modell-Nr.
Pattern-No.
Projektionsmethode 1
First angle projection method
ISO 128

	Datum Date	Name
Bearb. Drawn	27.09.11	Fryen
Geprüft Checked	27.11.09	Prätzel
Norm Stand		

Typ
Type Safety Layout
Benennung Teilbereich, 6
Title PARTITION 6
Maßstab
Scale 1:100
Sach-Nr. Drawing-No. 0100133-00.654
Blatt
Sheet 2
6 Blätter
Sheets
Ersatz für:/Supersedes:
Ersetzt durch:/Superseded by:

Aus- gabe Issue	Änderung Revision	Datum Date	Name

SMS MEER
SMS group

Diese Zeichnung und alle darauf enthaltenen Informationen sind vertraulich. This drawing and all information on it is confidential.

A0

The reproduction, distribution and utilization of this document as well as the disclosure of its content to others without prior explicit written consent of SMS Meer GmbH is prohibited. Holder has to protect this document against unauthorized withdrawal of third parties. Offenders will be held liable for the payment of damages. All rights reserved in case of patent/utility model/trademark protection.