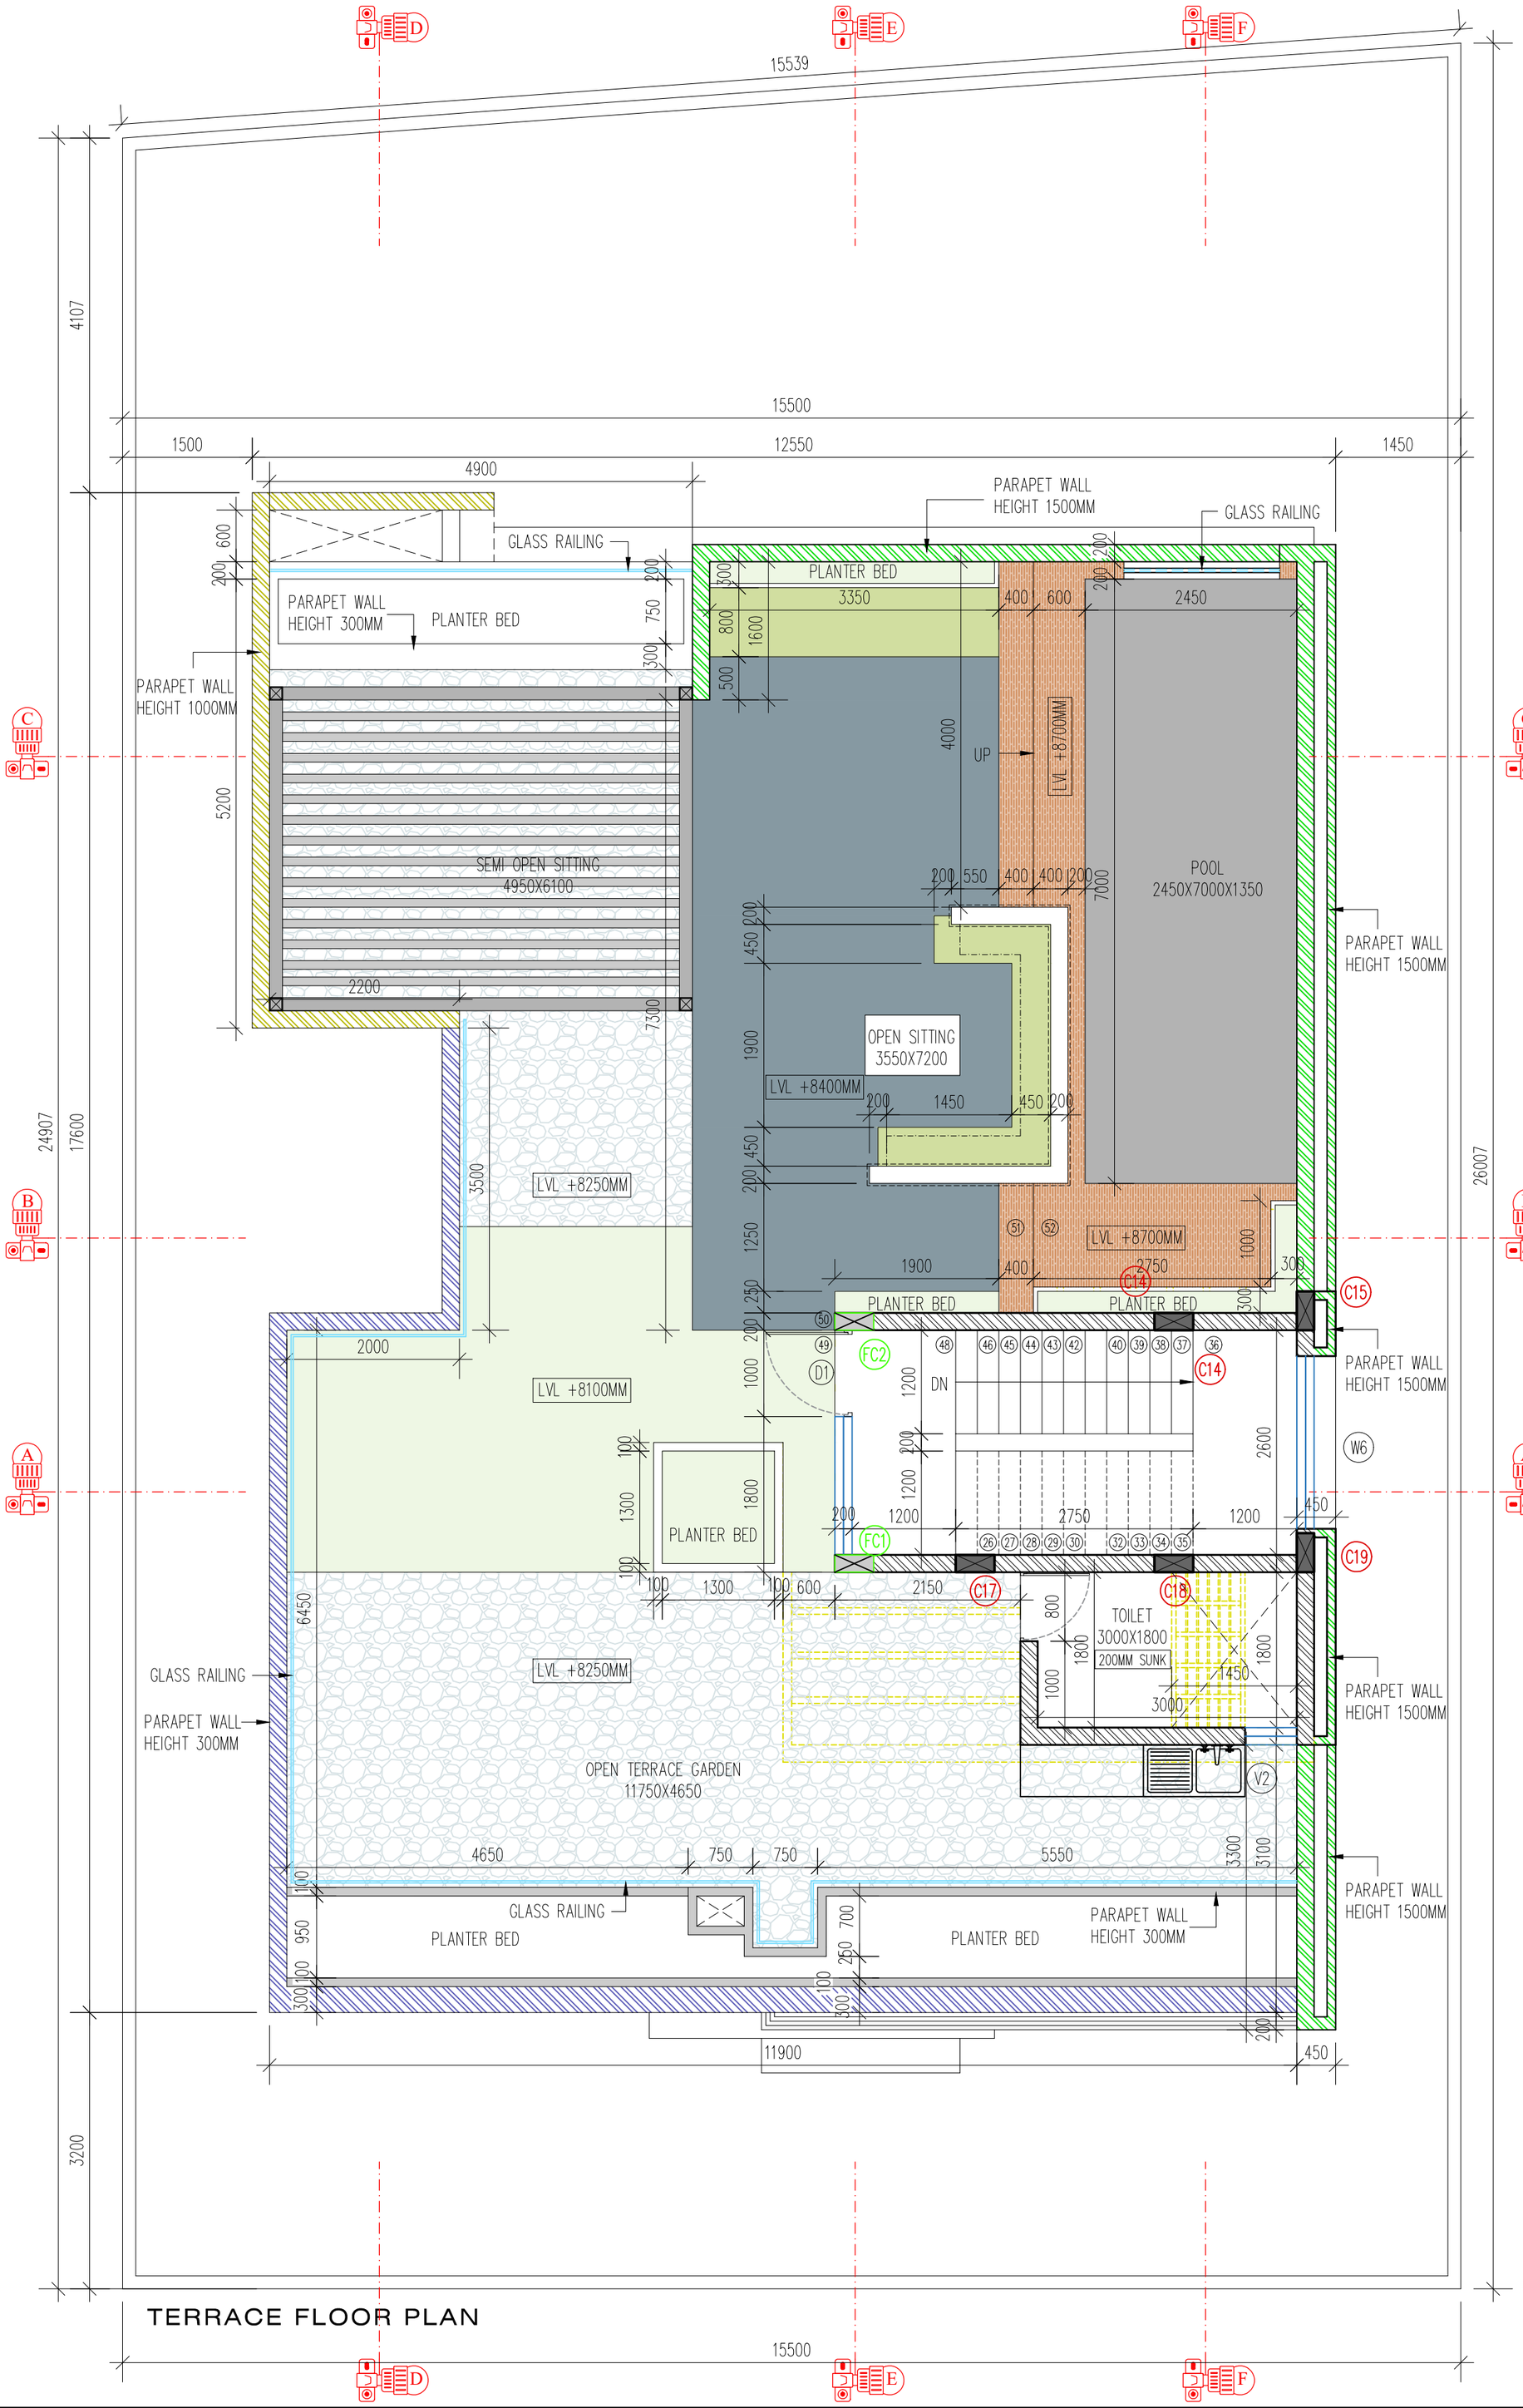


DRAWING NO:	*A- 05*
CLIENT : MR.ADITYA SATWE	
PROJECT: RESIDENTIAL	
SITE ADDRESS:	
46 BANYAN TREE,PLOT NO-904,CHANDKHED,MAVAL,PUNE	
PROJECT TYPE: RESIDENTIAL	
CONSULTANTS:	
RCC : SANKALPSIDDHI CONSULTANTS	LANDSCAPE: NA
ELECTRICAL: NA	FIRE FIGHTING : NA
PLUMBING : NA	HVAC : NA

LEGAL NOTE
*THIS DWG.IS BASED ON INFORMATION/DOC.PROVIDED BY OWNER
*THIS DWG.IS COPY RIGHT OF ARTEL STUDIOS.
*FOR ANY DISCREPANCY OR ERROR IN ARCHITECTURAL & RCC WORK, CONSULT ARCHITECT BEFORE COMMENCING THE CONSTRUCTION WORK
*ALL DIM. ARE IN MILLIMETERS & ONLY WRITTEN DIM. ARE TO BE FOLLOWED
*ALL SIZES OF DOORS & WINS.ARE INCL.OF FRAME.
*THIS DRG. IS TO BE READ IN CONJUNCTION WITH STRUCTURAL DRG.
*SUNK IN SLABS SHOWN AS SMUDGE. (UNLESS MENSIONED OTHERWISE]
TOILET SUNK 0.200M ,W.C. SUNK 0.450M , BATH - 0.200M & TERRACE -0.200M
*FINISHED FLR.LVL.OF TOILETS TO BE 0.050M SUNK.
*SITE INCHARGE SHOULD CHECK & VERIFY THIS DRG. IN CONJUCTION WITH RCC & ARCHITECTURAL DRG. PRIOR TO COMMENCEMENT OF WORK
*PLACEMENT OF BLDG./MARGINAL OPENSPACE TO BE MEASURD CHK.& VERIFI

REVISIONS

NO.	DATE	DESCRIPTION	Done By
01	00.00.0000	DRAWING ISSUED	SHEKHAR
02	00.00.0000	X X X X X X X X	

LEGENDS

SUNK HATCH SPECIFICATION	SUNK IN FLOOR PLAN W.C.& TOILET	SUNK 450 MM IN SECTION (W.C.)	
	SUNK IN FLOOR PLAN TERRACE	SUNK 200MM IN SECTION (BATH)	
BRICK HATCH SPECIFICATION	BRICK WALL 150MM THK PARAPET	CONCRETE IN SECTION	
	BRICK WALL 150MM THK	BRICK WALL 100MM THK	

PROJECT NO (JOB-NO)-	PR016
PHASE -	I
BUILDING -	A
SHEET NO -	05
DRAWING SET -	00/00
DWG ISSUE DATE -	00.00.000
NO.OF COPIES ISSUED -	01

SCHEDULE OF OPENINGS

DOORS

FD	3400X3150	SLIDING DOOR	D8	800X1350	PARKING
FD1	2650X3150	SLIDING DOOR			
D	1500X3000	MAIN ENTRANCE	OP	1000X2450	
D1	1000X2450	BEDROOM	OP1	1300X2450	
D2	800X2450	TOILET	OP2	1600X2450	
D3	800X2150	TOILET	OP3	1900X2450	
D4	900X2450	KITCHEN/UTILITY	OP4	2500X2450	

WINDOWS		SILL	LINTEL	
W	3900X2550	450	3000	BEDROOM - 02 / LIVING
W1	2400X2700	450	3150	FAMILY AREA
W2	2250X2700	450	3150	BEDROOM - 01
W3	1800X1800	650	2450	PARENT'S BEDROOM
W4	2550X1200	950	2150	KITCHEN
W5	800X6300	450	6750	LIVING
W6	2000X6200	1350	7550	(STAIRCASE)
W7	600X2700	450	3150	VESTIBULE
W8	1800X2700	450	3150	LIVING
W9	2900X2700	450	3150	DINING
W10	1200X1500	950	2450	UTILITY
W11	**750X800**	**950**	**1750**	**KITCHEN**
W12	750X1200	950	1750	UTILITY
V	1800X2700	450	3150	VENTILATOR
V1	1200X750	1700	2450	VENTILATOR
V2	600X750	1350	2100	VENTILATOR

Lay out

Drawing Title -	NORTH
TERRACE FLOOR PLAN	DWG SCALE - 1:75

NOTES :- STUDY COPY NOT FOR EXECUTION
A BUILDING SANCTIONED G+1 FLOOR

SIGN OFF	AUTHORITY NAME OF PERSON	SIGN & DATE
FOR STUDY COPY	X X X X X X	
FOR APPROVAL	X X X X X X	
CLIENT APPROVAL	BY MAIL / HARD COPY	
FOR EXECUTION	X X X X X X	

AUTHORITY	CHECKED BY	Sign & date
PROJECT OWNER	MR.ADITYA SATWE	
ENGINEER		
DRAWN BY	SHEKHAR	
ARCHITECT - ARTEL STUDIOS		

ARTEL STUDIOS PVT. LTD.
Plot No. 480, Sector No. 18,
Shivtejnagar, Chinchwad, Pune - 411019.
E-MAIL :- info@artelstudios.in
WEB :-www.artelstudios.in TEL :- +91 - 8484 00 6161