
SPOT LEVEL
FRL +573.50

--- ACCESS ROAD ---
AS PER CONTOUR SURVEY DWG

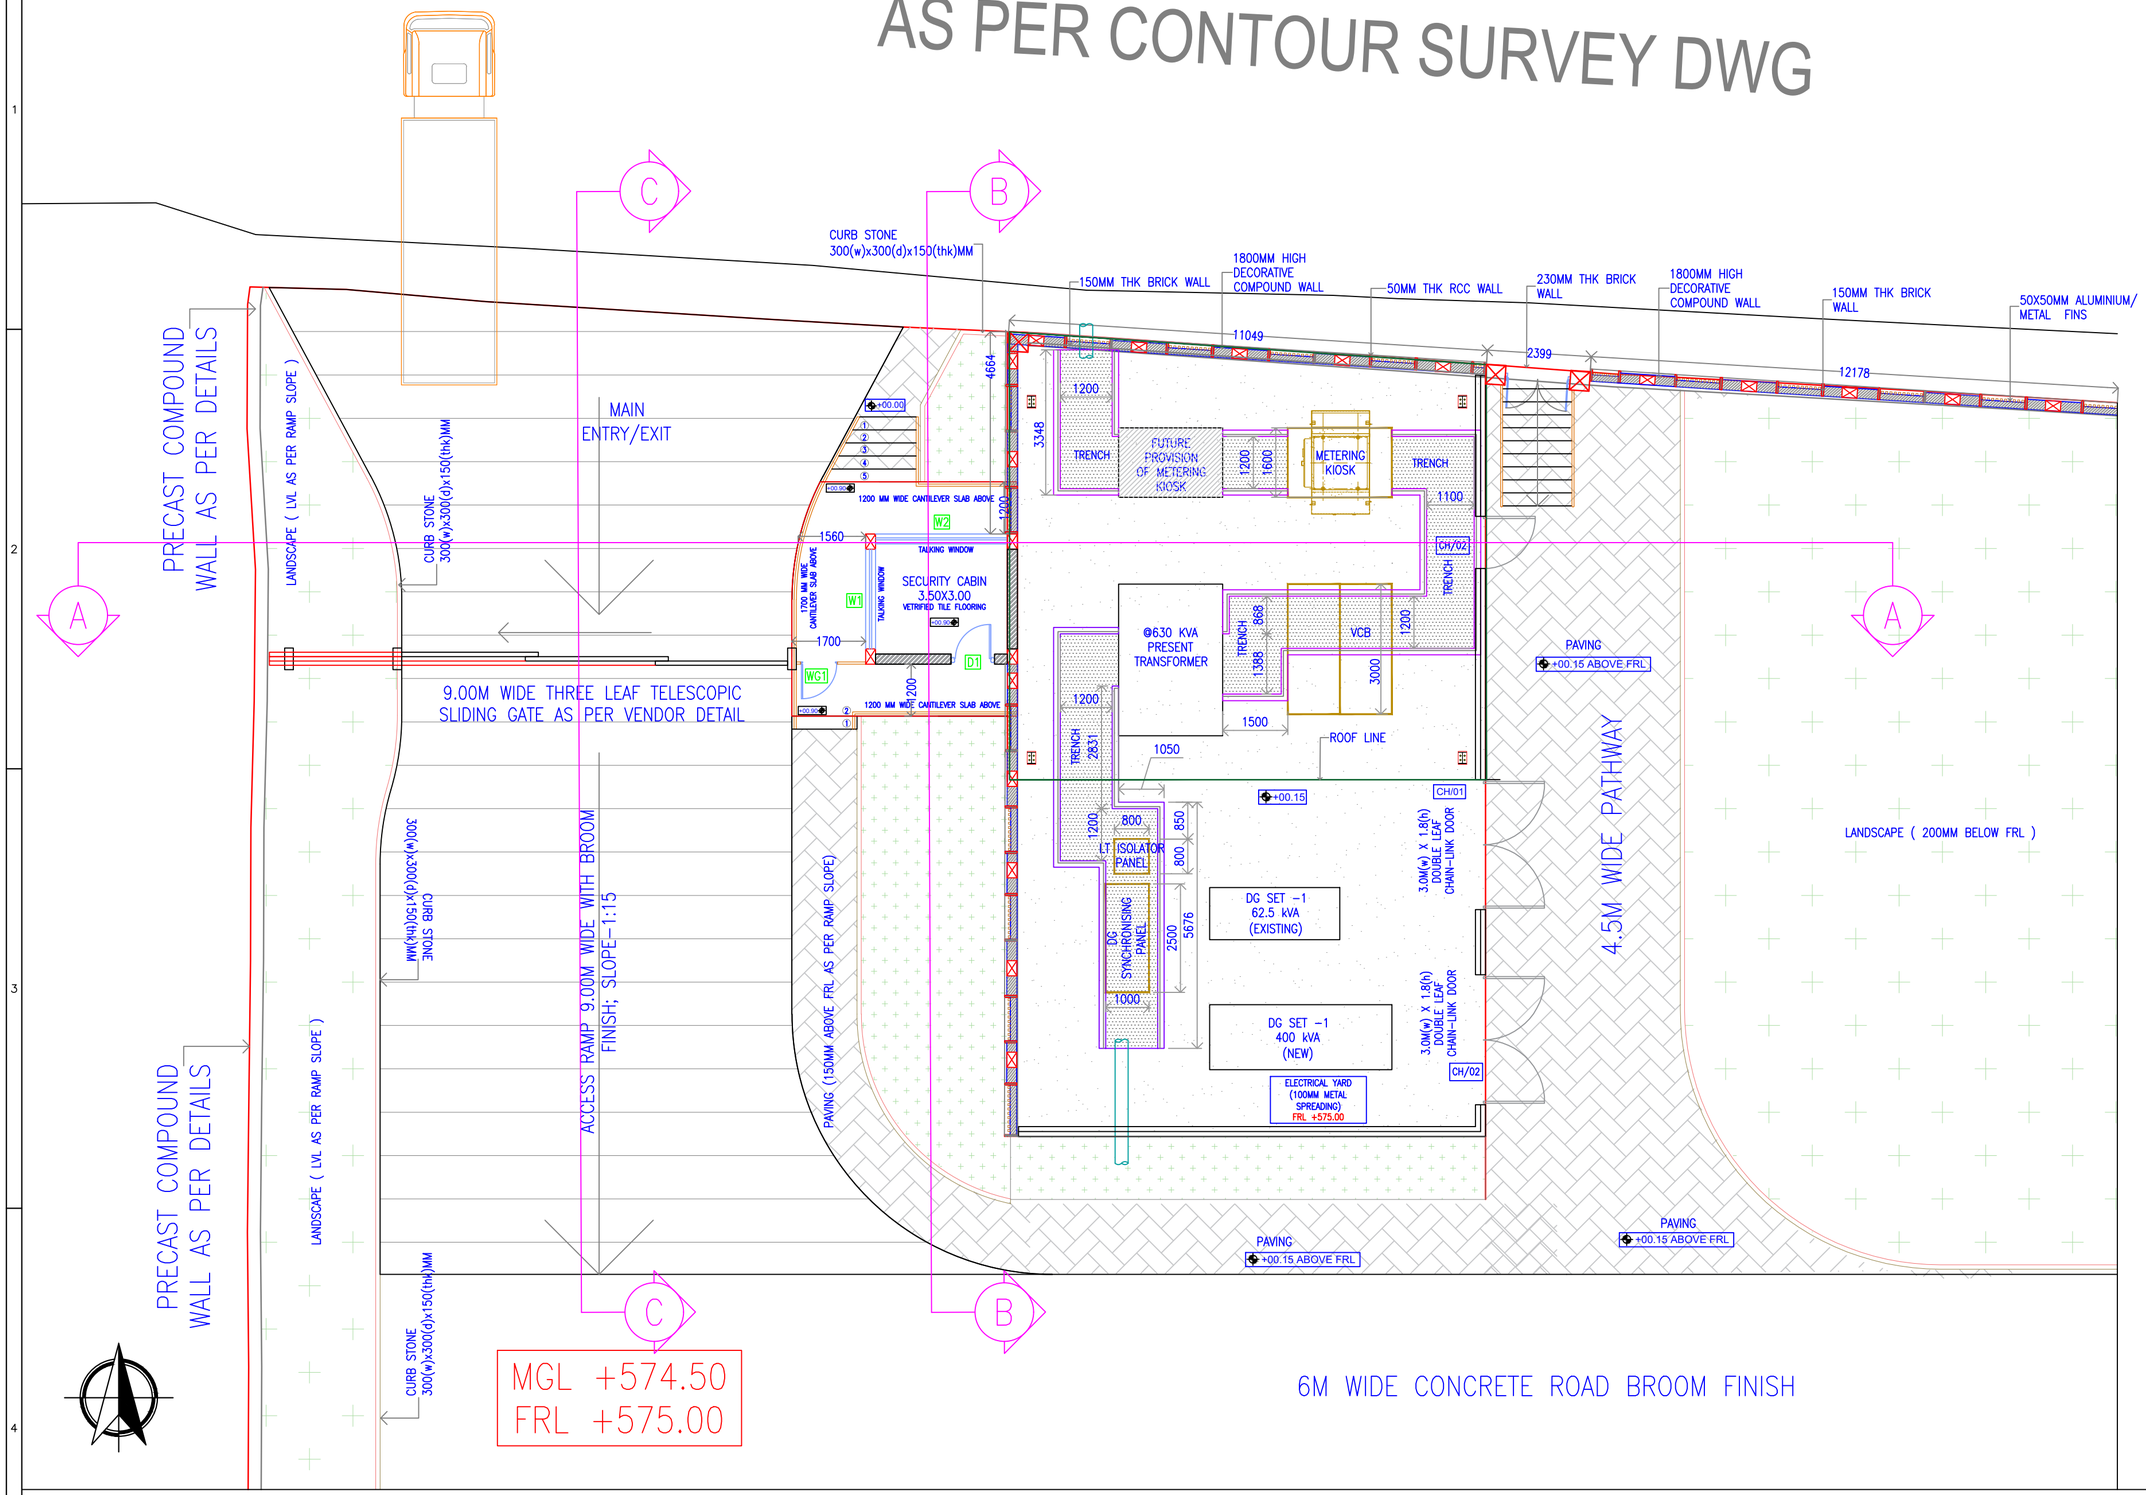

ENTRANCE CLUSTER PLAN
SCALE-1:100


THIS DRAWING IS THE PROPERTY OF ARCHIVISTA ENGINEERING PROJECTS PVT. LTD. IT IS ISSUED FOR PRELIMINARY ENGINEERING & APPROVAL. ANY MISUSE, DUPLICATION, ALTERATION OR REUSE FOR ANOTHER PURPOSE IS STRICTLY PROHIBITED & SHALL BE DEALT LEGALLY.ALL RIGHTS RESERVED WITH THE COMPANY.

PRINT DATE : 22.02.2023
DWG PATH : ~~~~

DWG.No.
NCI612_TD_ARCH_ALL-EC_00 R0

RELEASED FOR TENDER

KEY PLAN

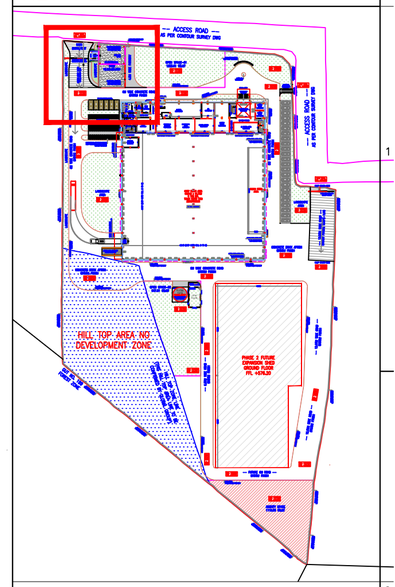

REVISIONS :

NO.	DATE	REMARKS
R0	08.11.24	RELEASED FOR TENDER

DEPT.HEAD SIGN

CLIENT SIGN

CLIENT:
NITTA CORPORATION INDIA PVT.LTD.

TITLE:
ENTRANCE CLUSTER DETAILS

DWG.No.
NCI612_TD_ARCH_ALL-EC_00 R0

JOB NO :	NCI612	DRAWN BY :	KASHYAP
SCALE :	1:100	CHECKED BY :	RAGHAV K.
DATE :	08.11.2024	APPROVED BY :	SRJ

ARCHIVISTA
ENGINEERING PROJECTS PVT.LTD.
Office No.201&202,Sai Empire, Baner,
PUNE-411045, MAHARASHTRA,INDIA.
PH.91-20-66294444,460
www.archivistaindia.com