

PRODUCED BY AN AUTODESK EDUCATIONAL PRODUCT

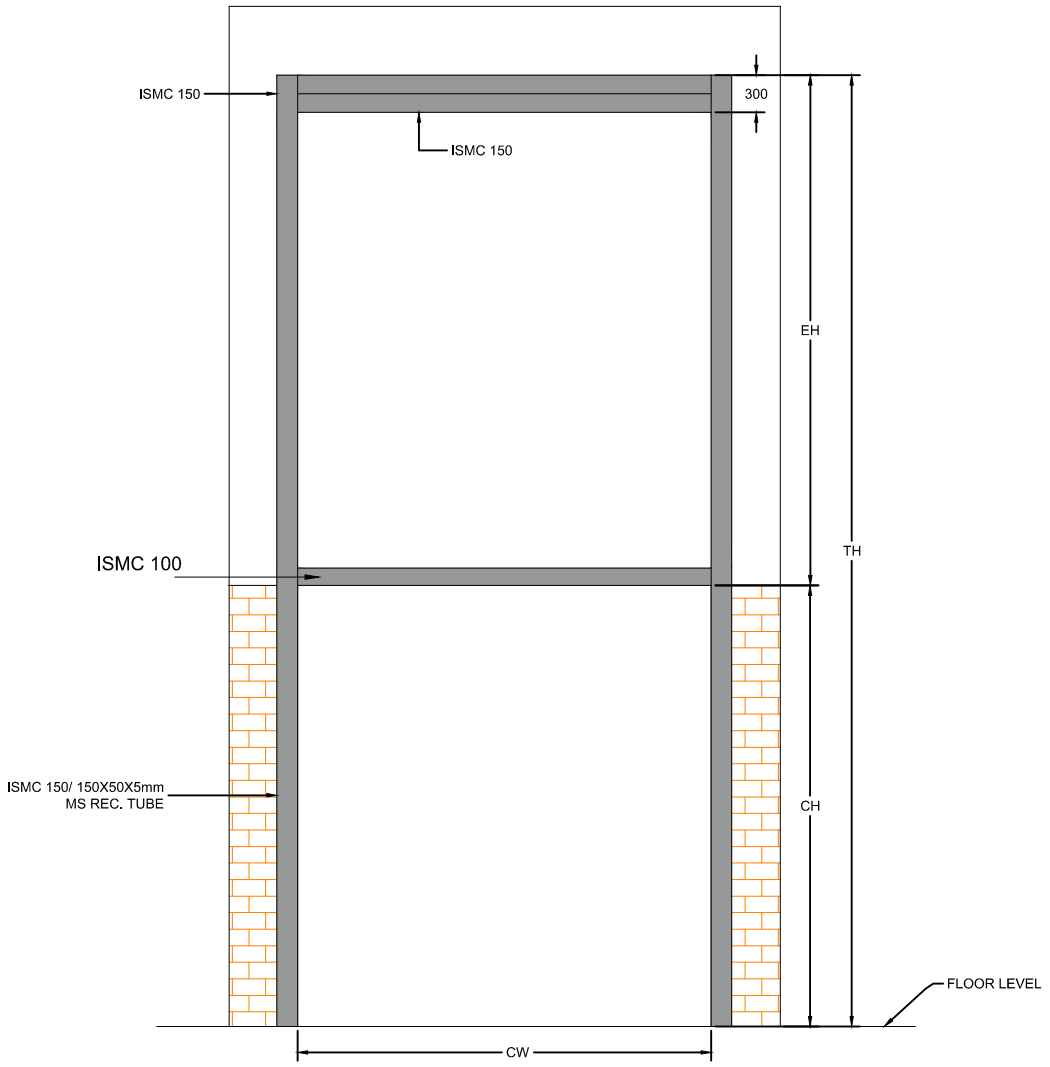

INSIDE ELEVATION

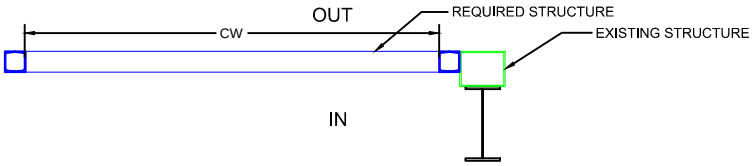

TOP VIEW

NOTE- STRUCTURE FOR SECTIONAL DOOR WILL BE IN CLIENTS SCOPE.

SR NO	CLEAR WIDTH	CLEAR HEIGHT	QTY	TH	EH	LOCATION (w.r.t PEB A01-R1)	MOTOR POSITION
1	3850mm	6000mm	1	12300	6300	1-A & A1'	LEFT

This drawing & design is the property of NIHVA TECHNOLOGIES. Not to be sold or copied to any other concern.

TITLE

STRUCTURE FOR SECTIONAL DOOR

CLIENT APPROVAL

ALL DIMENSION ARE IN mm

NIHVA TECHNOLOGIES PVT. LTD.

NIHVA TECHNOLOGIES PVT. LTD. PUNE
Tel : 020 66304033
Email:- info@nihva.com
Website:- www.nihva.com

	SIGN	DATE
DRAWN	OMKAR	12/05/17
CHECK	SAGAR P.	12/05/17
REV.		
APPRD.		
MFG		
Ref. No.		

CLIENT - TATA PROJECTS

PROJECT - MADHEPURA ELECTRIC LOCOMOTIVE PVT. LTD.

SITE - MADHEPURA,BIHAR

DWG. NO. - NIHVA/17-18/0040

SCALE: NTS | WT: | SHEET: 01 OF 01

If any queries contact : projects@nihva.com

PRODUCED BY AN AUTODESK EDUCATIONAL PRODUCT