


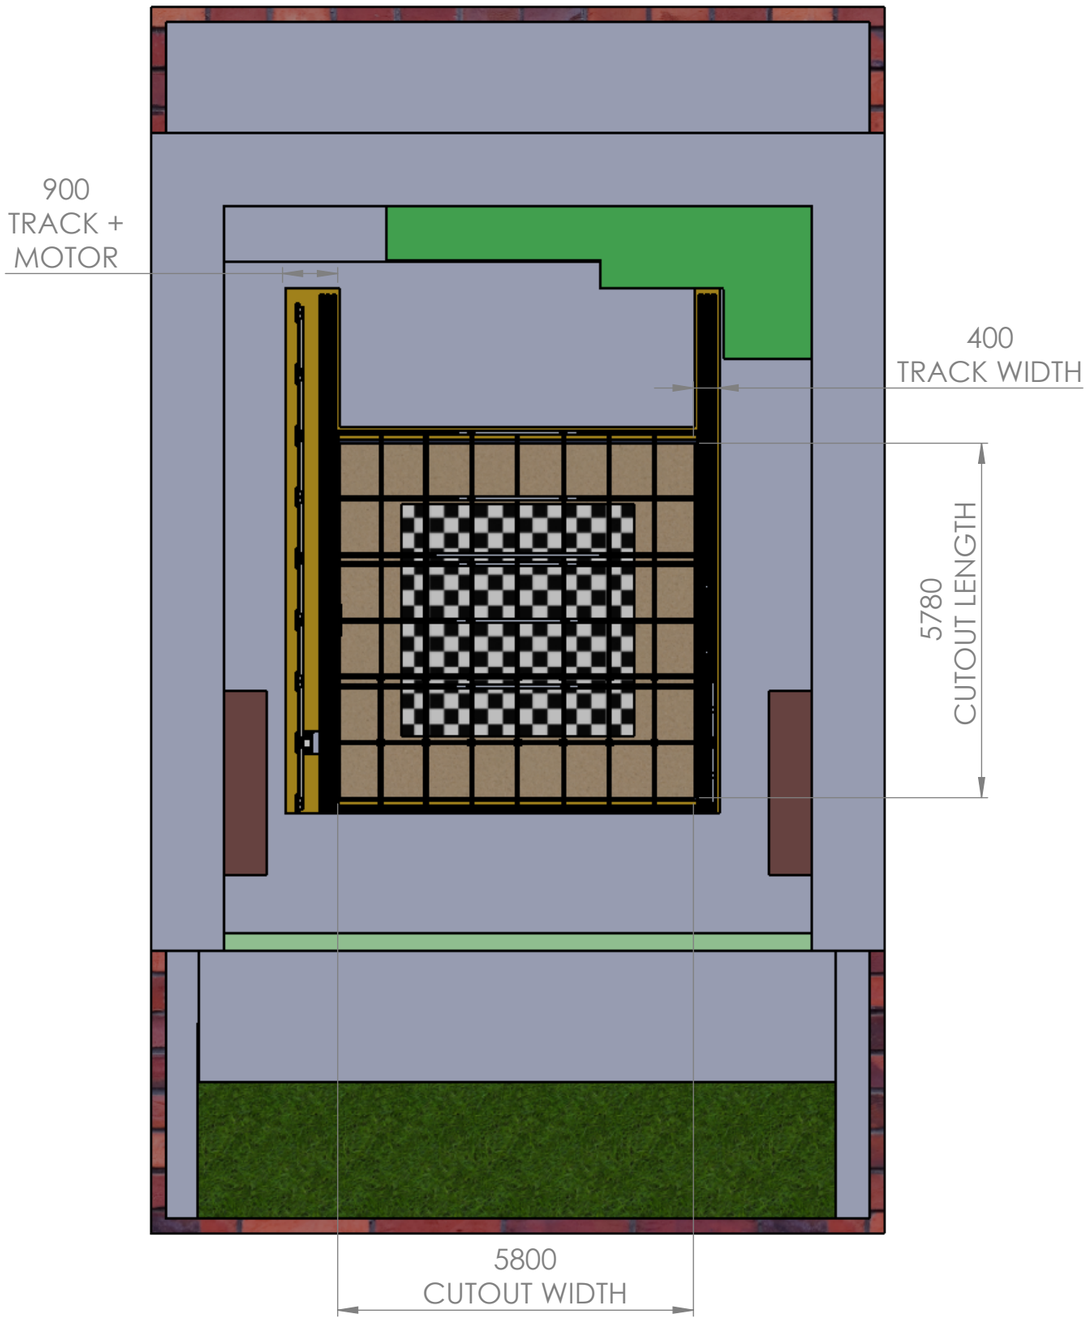



ITEM NO.	PART NUMBER	DESCRIPTION	QTY.
1	CIVIL BASE	CLIENT SCOP	1
2	GUIDE RAILS-T75-1B	STD (5 M LENGTH)	12
3	Anchor Bolt M10x75	STD	76
4	PANEL_01 ASM	INHOUSE	1
5	PANEL_02 ASM	INHOUSE	1
6	PANEL_03 ASM	INHOUSE	1
7	NICE MOTOR 1T	STD	1
8	Rack support_575	STD (LOOSE PART)	9
9	RACK	STD (M4 RACK, 30x8x1000 mm, ZINC COATED WITH SPACERS AND SCREWS.)	9
10	BUSBAR FLASHER	STD (LOOSE PART)	4

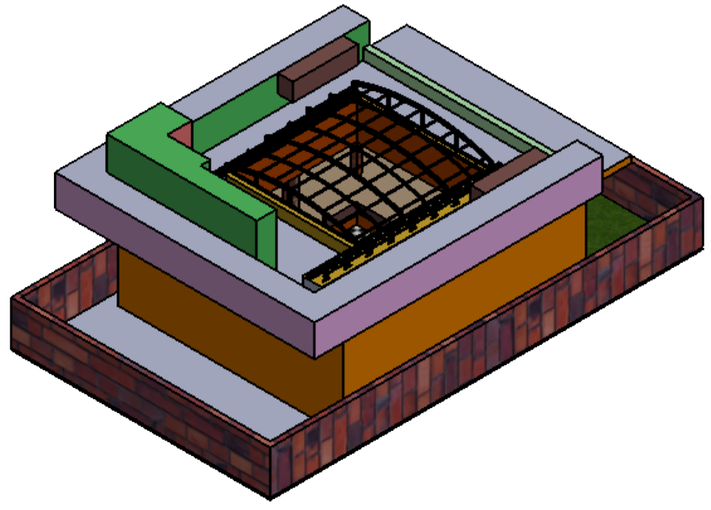

TITLE - RETRACTABLE ROOF				NIHVA TECHNOLOGIES PVT.LTD.PUNE
DWG NO - NTPL268-PM			QTY - 1	Website - www.nihva.com
	NAME	SIGNATURE	DATE	PROJECT NO - NTPL268-PM- AD
DRAWN	S.W		03-03-2025	PRODUCT - RETRACTABLE ROOF
CHK'D	P.M.		03-03-2025	SITE LOCATION - GUJARAT
APPV'D	V.T.		03-03-2025	
if any queries contact - supportautomation@nihva.com				REVISION -
ALL DIMENSION ARE IN mm			A3	SCALE - SHEET 1 OF 16

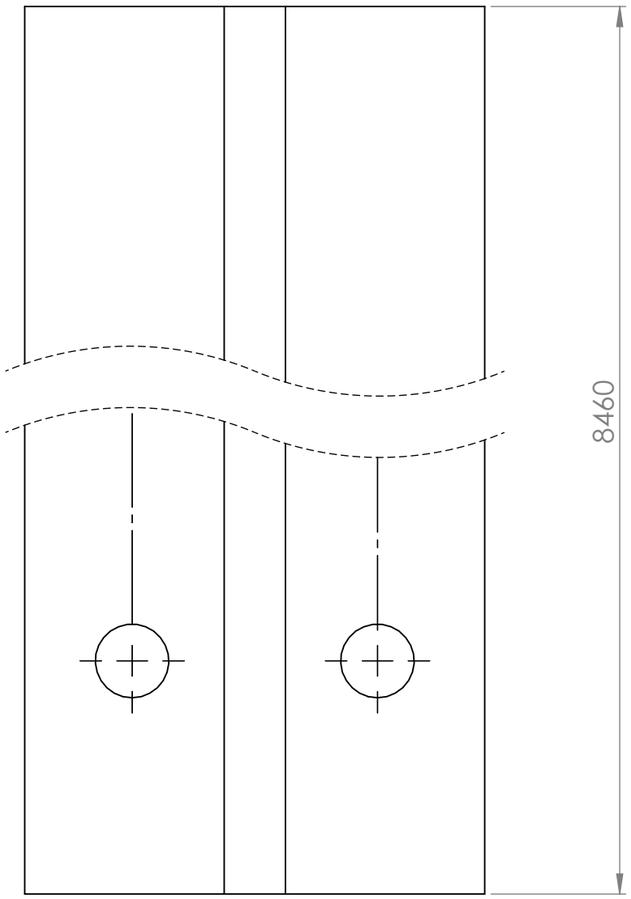

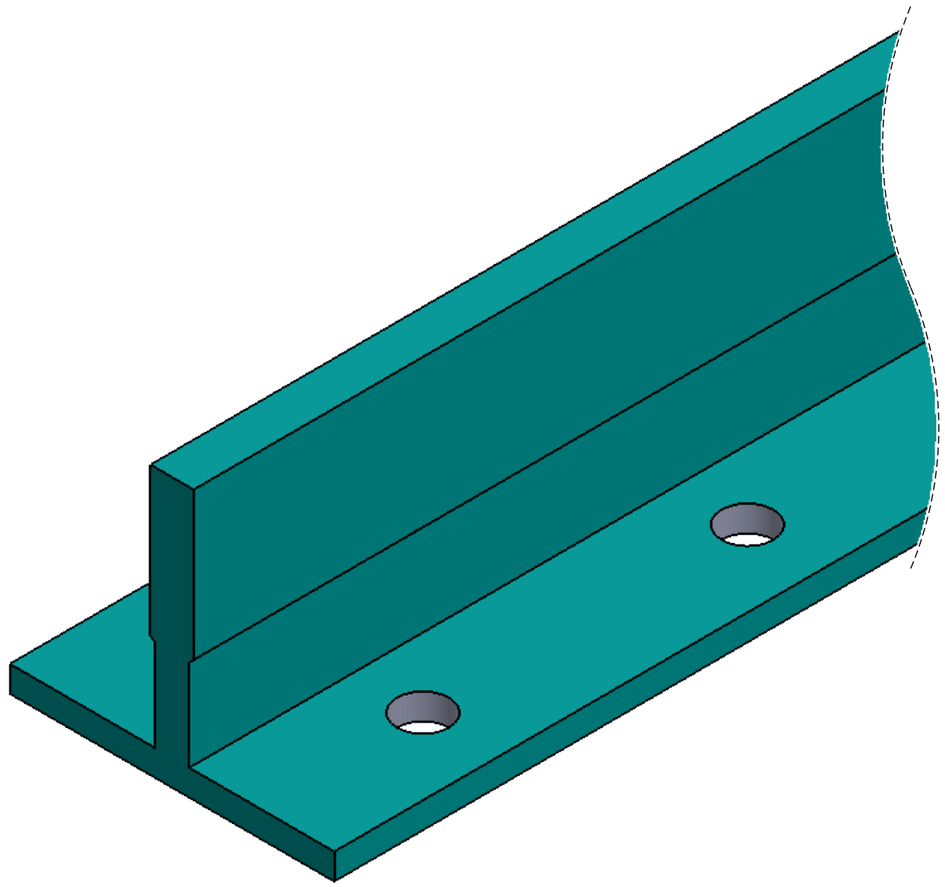


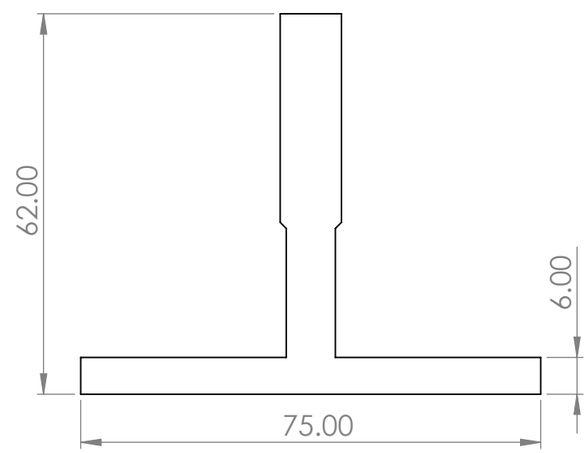



ITEM NO.	PART NUMBER	DESCRIPTION	QTY.
1	GUIDE RAILS-T75-1B	STD (5 M LENGTH)	12

TITLE - RETRACTABLE ROOF				NIHVA TECHNOLOGIES PVT.LTD.PUNE
DWG NO - NTPL268-PM			QTY - 1	Website - www.nihva.com
	NAME	SIGNATURE	DATE	PROJECT NO - NTPL268-PM- AD
DRAWN	S.W		03-03-2025	PRODUCT - RETRACTABLE ROOF
CHK'D	P.M.		03-03-2025	SITE LOCATION - GUJARAT
APPV'D	V.T.		03-03-2025	
if any queries contact - supportautomation@nihva.com				REVISION -
ALL DIMENSION ARE IN mm			A3	SCALE -

ITEM NO.	PART NUMBER	DESCRIPTION	QTY.
1	NTPL-268-PM-PANEL_01	PANEL_01 FRAME	1
2	AL Support tube SQ TUBE 40X40X1.5 MM L-734 MM	AL INTERMEDIAT SUPPORT TUBE	18
3	rivet_iso_15977_4_x_16_0	RIVET M4X16	80
4	T PLATE	JOINING PLATE	4
5	L PALTE	JOINING PLATE	8
6	L ANGLE PLATE	JOINING PLATE	8
7	PROFILE L ANGLE WELDING PLATE	JOINING PLATE	4
8	BEARING BLOCK ASM WITH SHOULDER BOLT	SLIDING BLOCK	4
9	ENCLOSURE NTPL-268-PM-PANEL_01	ENCLOSURE _01	1

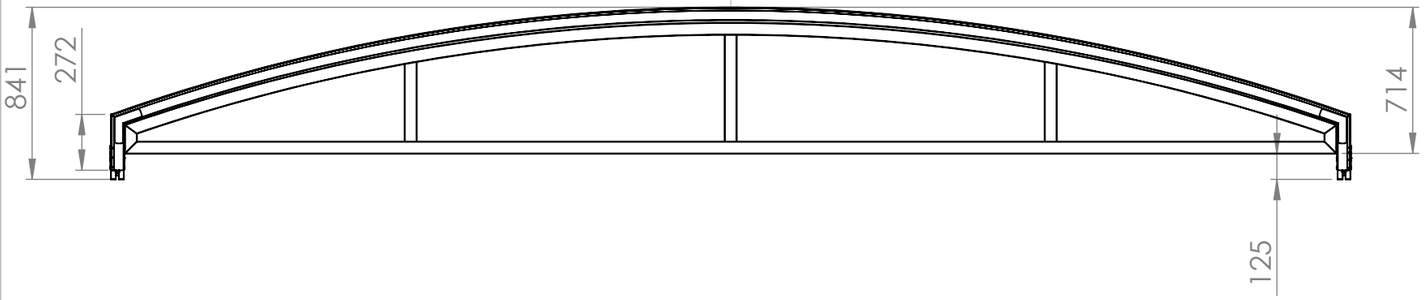

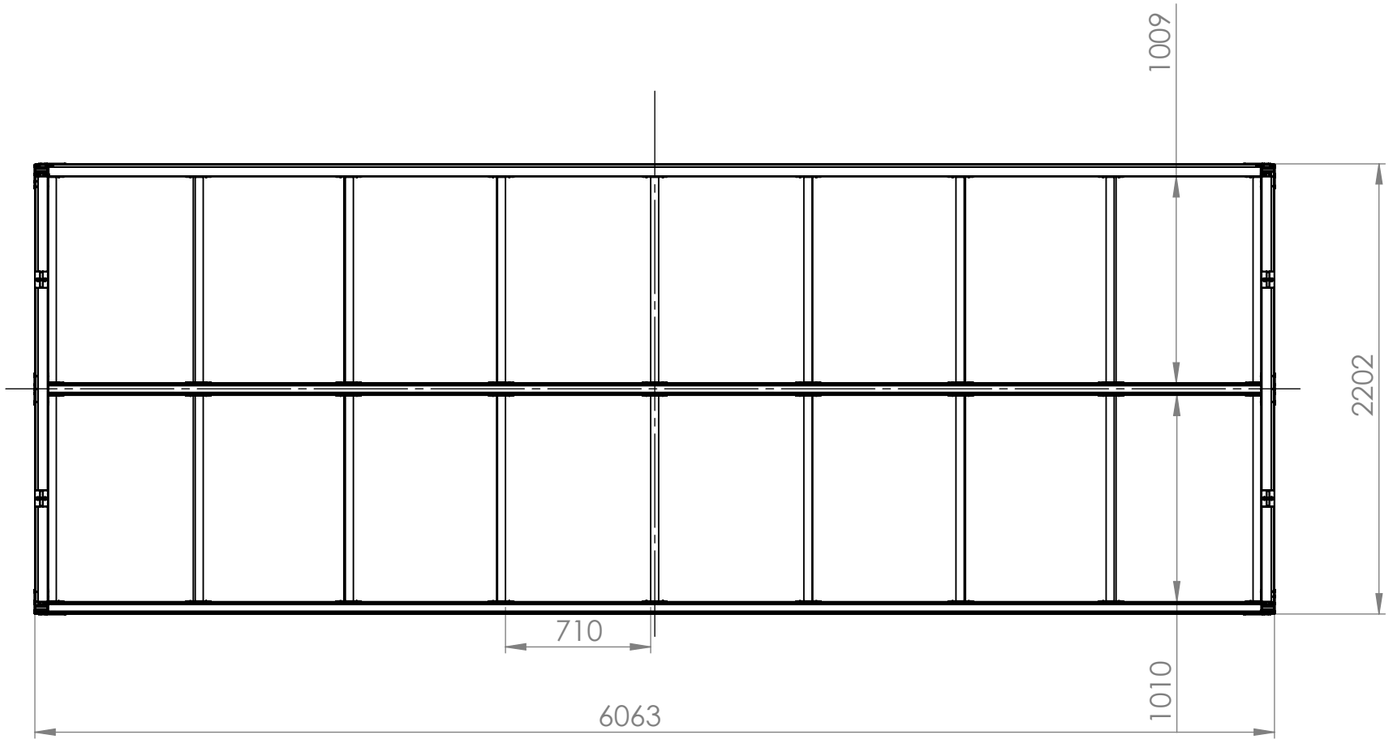


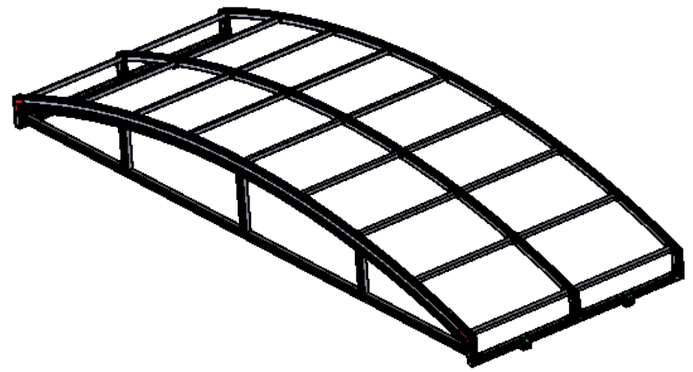


PANEL_01


TITLE - RETRACTABLE ROOF				NIHVA TECHNOLOGIES PVT.LTD.PUNE Website - www.nihva.com
DWG NO - NTPL268-PM			QTY - 1	
	NAME	SIGNATURE	DATE	PROJECT NO - NTPL268-PM- AD
DRAWN	S.W		03-03-2025	PRODUCT - RETRACTABLE ROOF
CHK'D	P.M.		03-03-2025	SITE LOCATION - GUJARAT
APPV'D	V.T.		03-03-2025	
if any queries contact - supportautomation@nihva.com				REVISION -
ALL DIMENSION ARE IN mm			A3	SCALE -


ITEM NO.	PART NUMBER	DESCRIPTION	QTY.
1	NTPL-268-PM-PANEL_01	PANEL_01 FRAME	1

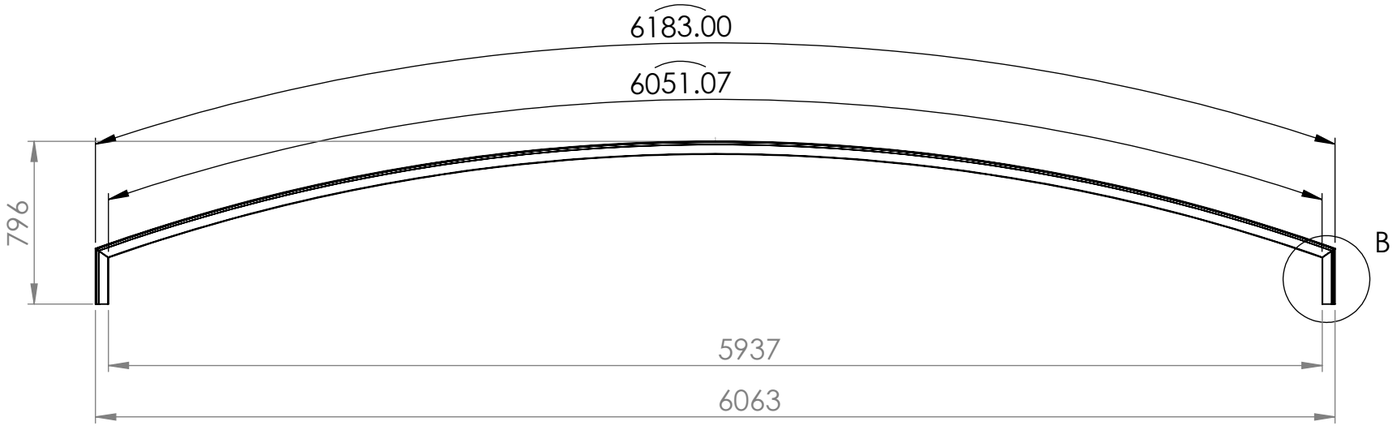

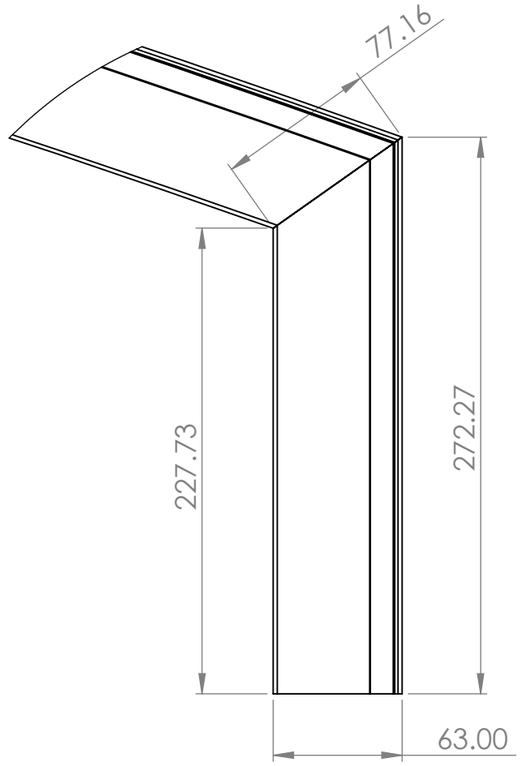


DETAIL B
SCALE 1 : 3

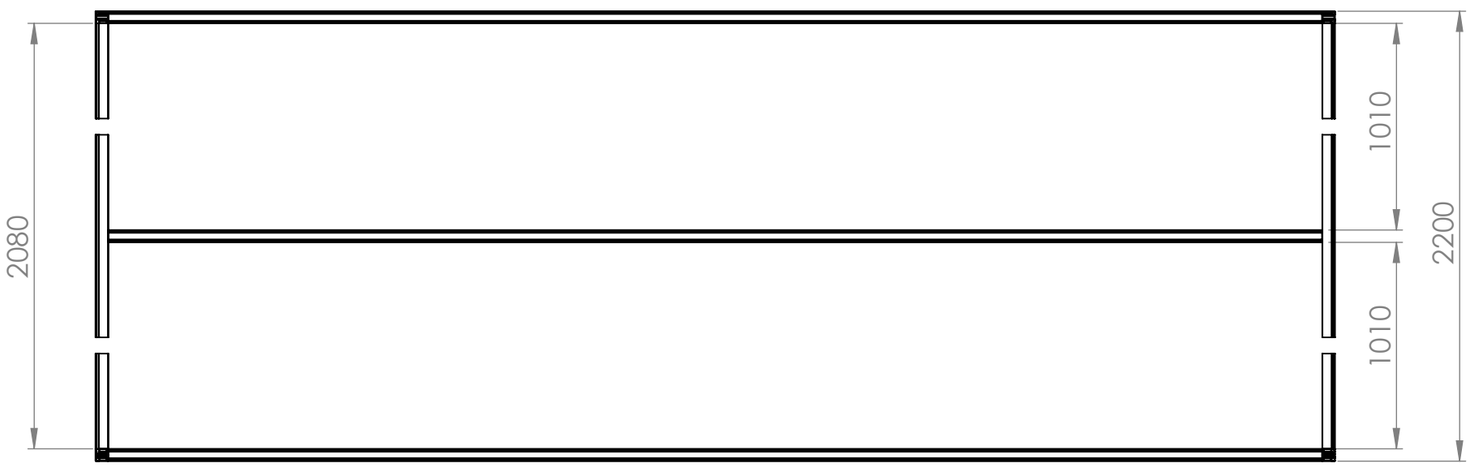


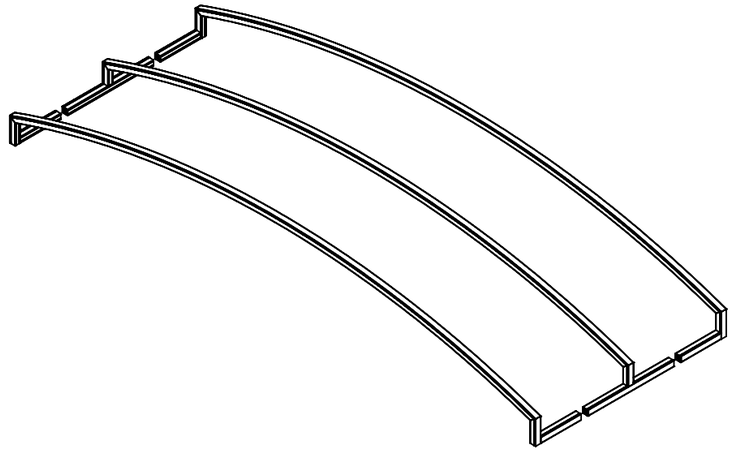

TITLE - RETRACTABLE ROOF				NIHVA TECHNOLOGIES PVT.LTD.PUNE
DWG NO - NTPL268-PM			QTY - 1	Website - www.nihva.com
	NAME	SIGNATURE	DATE	PROJECT NO - NTPL268-PM- AD
DRAWN	S.W		03-03-2025	PRODUCT - RETRACTABLE ROOF
CHK'D	P.M.		03-03-2025	SITE LOCATION - GUJARAT
APPV'D	V.T.		03-03-2025	
if any queries contact - supportautomation@nihva.com				REVISION -
ALL DIMENSION ARE IN mm			A3	SCALE - SHEET 4 OF 16

ITEM NO.	PART NUMBER	DESCRIPTION	QTY.
1	AL Support tube SQ TUBE 40X40X1.5 MM L-734 MM	AL INTERMEDIAT SUPPORT TUBE	62

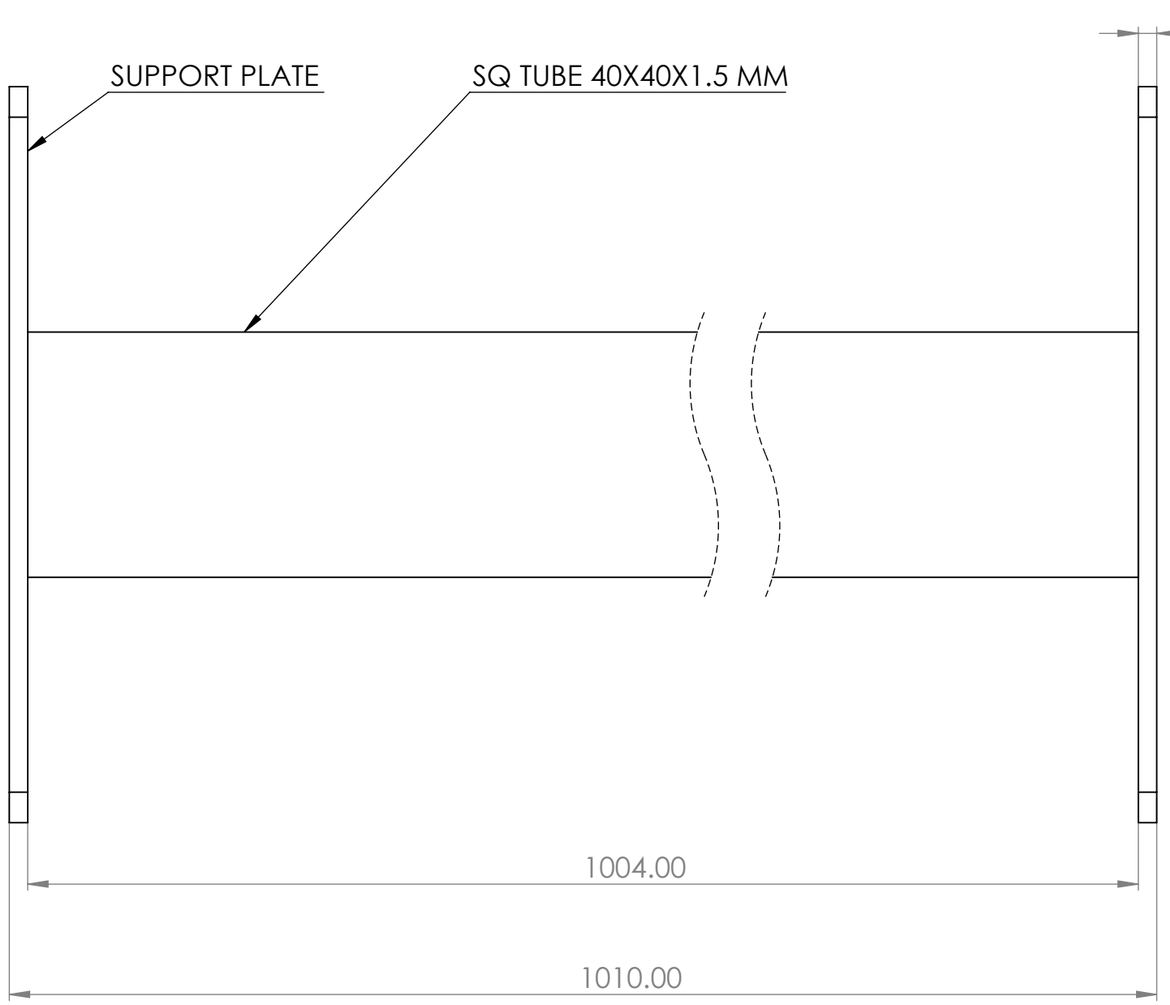

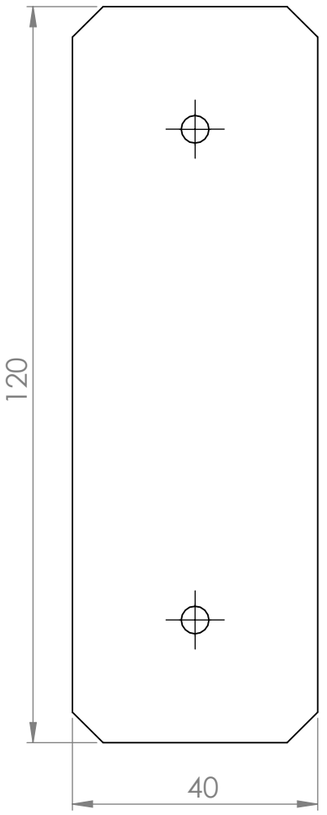


NOTE -


FOR ALL PANEL THIS INTERMEDIAT SUPPORT TUBE IS USED

TITLE - RETRACTABLE ROOF				NIHVA TECHNOLOGIES PVT.LTD.PUNE
DWG NO - NTPL268-PM			QTY - 1	Website - www.nihva.com
	NAME	SIGNATURE	DATE	PROJECT NO - NTPL268-PM- AD
DRAWN	S.W		03-03-2025	PRODUCT - RETRACTABLE ROOF
CHK'D	P.M.		03-03-2025	SITE LOCATION - GUJARAT
APPV'D	V.T.		03-03-2025	
if any queries contact - supportautomation@nihva.com				REVISION -
ALL DIMENSION ARE IN mm			A3	SCALE - SHEET 5 OF 16

ITEM NO.	PART NUMBER	DESCRIPTION	QTY.
1	T PLATE	SS304 -117.5X156X3 MM THK	15

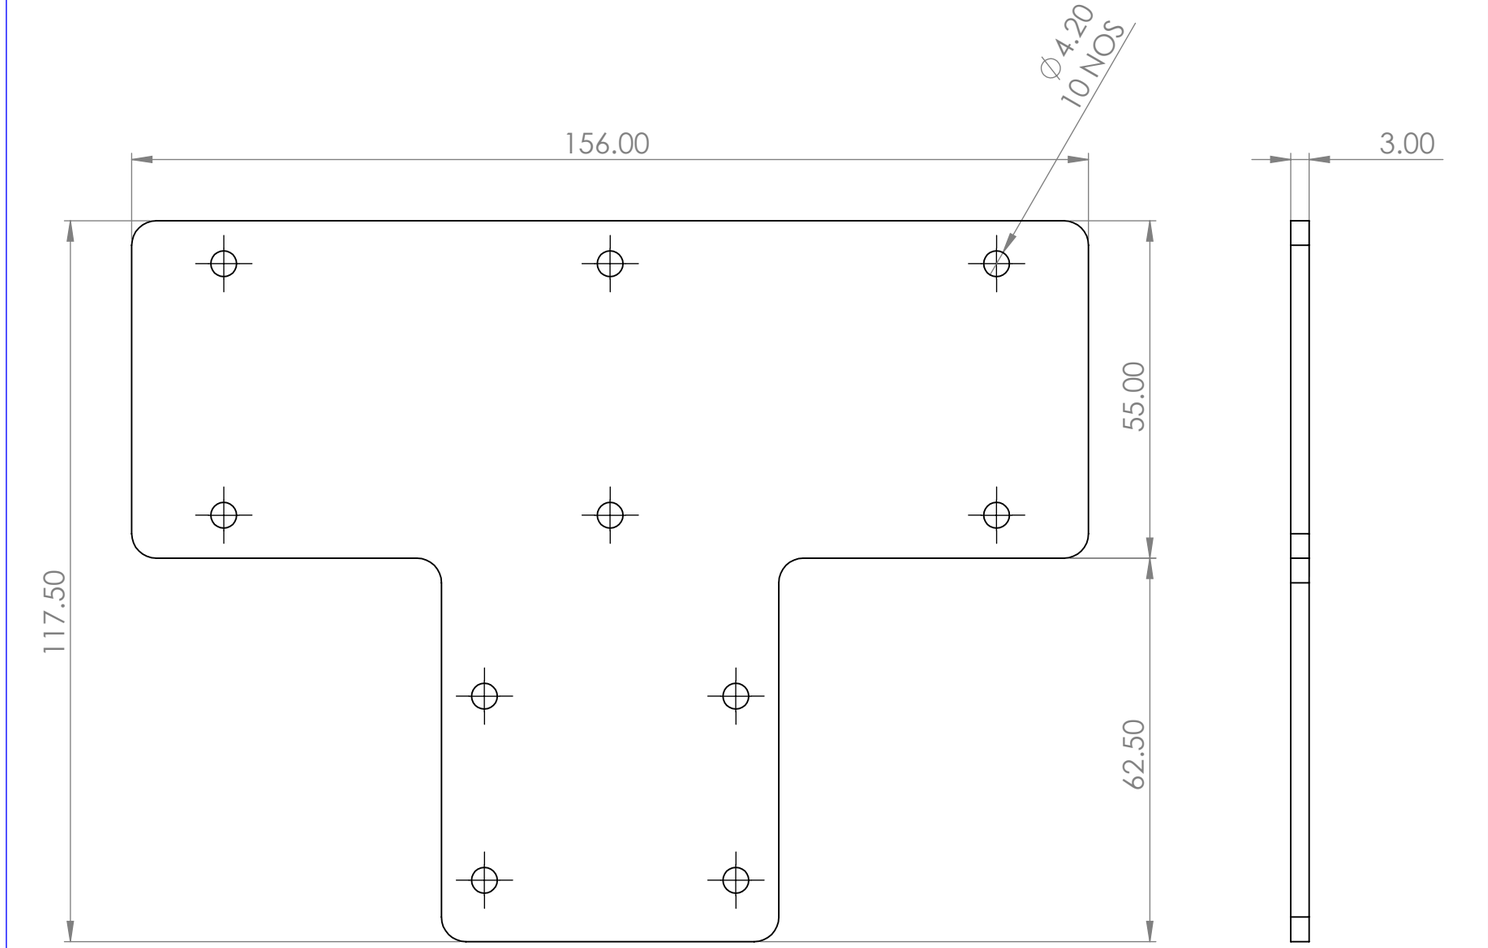

DEVELOPMENT VIEW

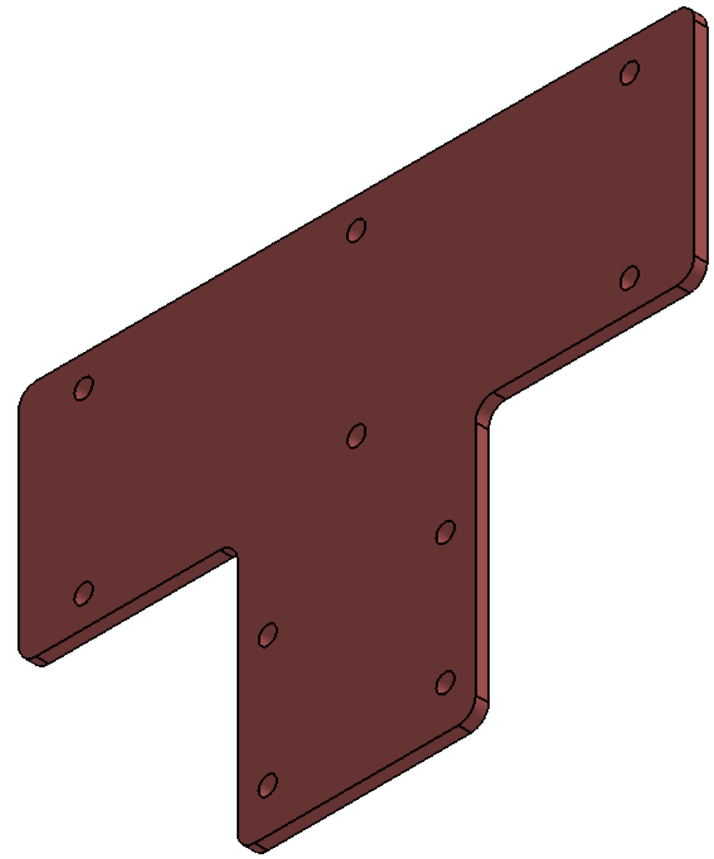


NOTE -

FOR ALL PANEL THIS T PLATE IS USED


LASER CUTTING

TITLE - RETRACTABLE ROOF				NIHVA TECHNOLOGIES PVT.LTD.PUNE
DWG NO - NTPL268-PM			QTY - 1	Website - www.nihva.com
	NAME	SIGNATURE	DATE	PROJECT NO - NTPL268-PM- AD
DRAWN	S.W		03-03-2025	PRODUCT - RETRACTABLE ROOF
CHK'D	P.M.		03-03-2025	SITE LOCATION - GUJARAT
APPV'D	V.T.		03-03-2025	
if any queries contact - supportautomation@nihva.com				REVISION -
ALL DIMENSION ARE IN mm			A3	SCALE - SHEET 6 OF 16

ITEM NO.	PART NUMBER	DESCRIPTION	QTY.
1	L PLATE	SS304- 91X106X3 MM THK	28

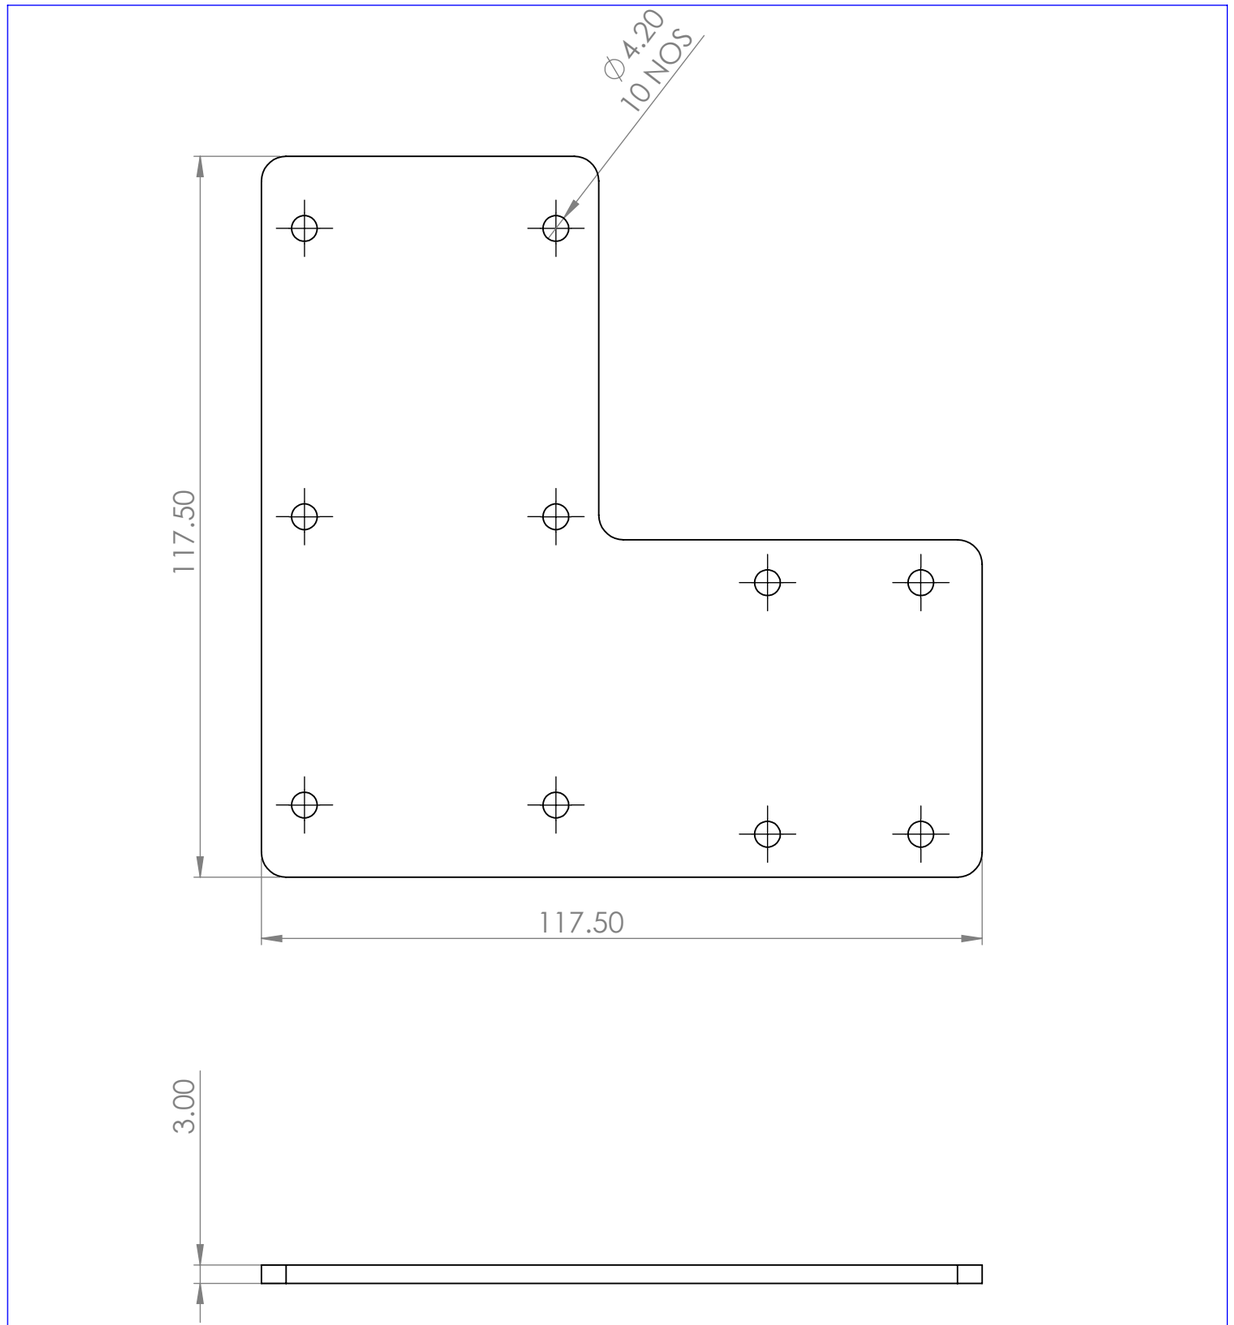

DEVELOPMENT VIEW

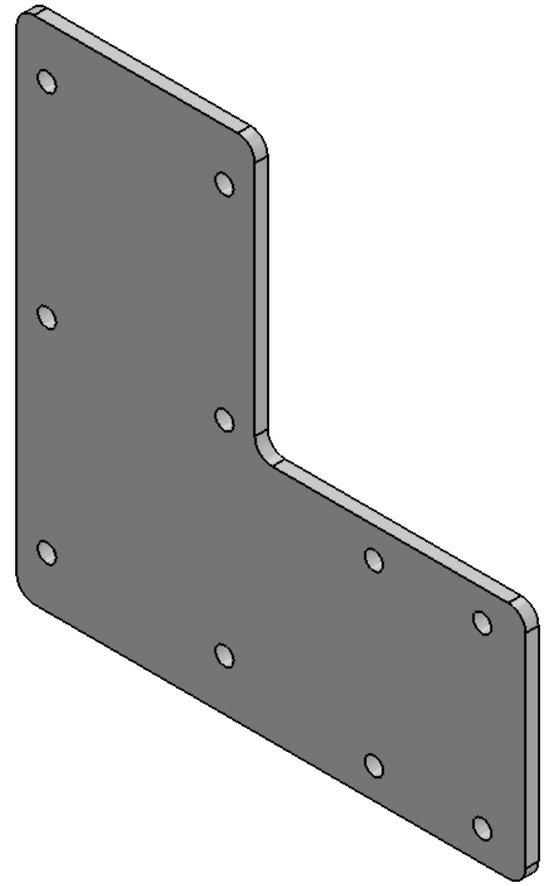


NOTE -


FOR ALL PANEL THIS L PLATE IS USED


LASER CUTTING

TITLE - RETRACTABLE ROOF				NIHVA TECHNOLOGIES PVT.LTD.PUNE Website - www.nihva.com
DWG NO - NTPL268-PM			QTY - 1	
	NAME	SIGNATURE	DATE	PROJECT NO - NTPL268-PM- AD
DRAWN	S.W		03-03-2025	PRODUCT - RETRACTABLE ROOF
CHK'D	P.M.		03-03-2025	SITE LOCATION - GUJARAT
APPV'D	V.T.		03-03-2025	
if any queries contact - supportautomation@nihva.com				REVISION -
ALL DIMENSION ARE IN mm			A3	SCALE - SHEET 7 OF 16

ITEM NO.	PART NUMBER	DESCRIPTION	QTY.
1	L ANGLE PLATE	SS304 - 60X60X3 MM	28

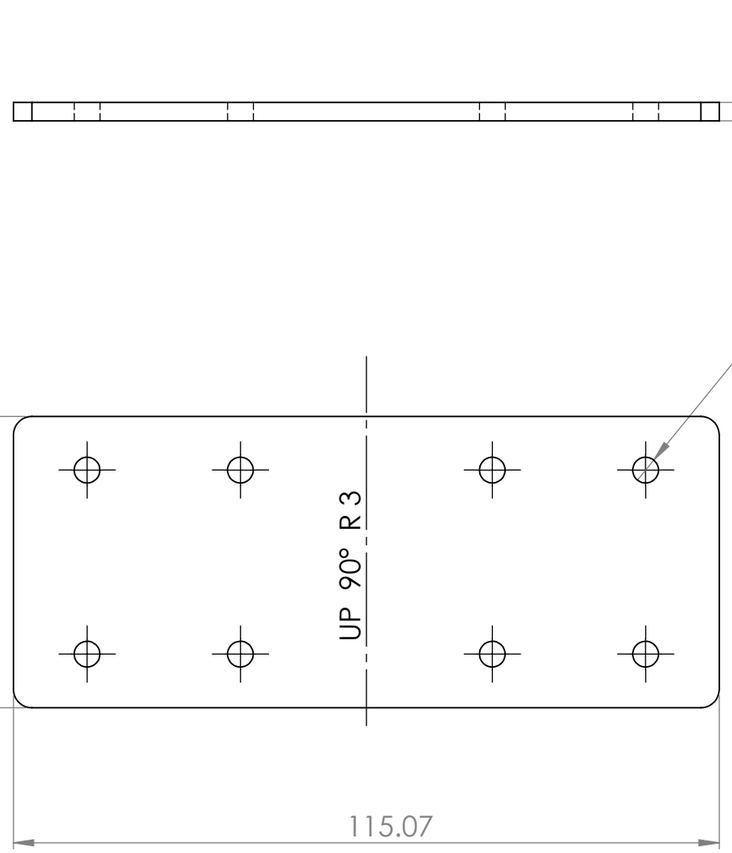

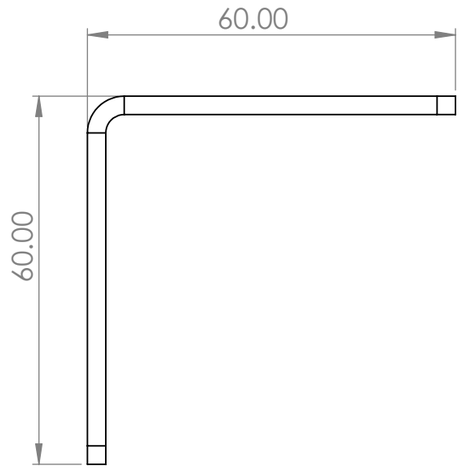

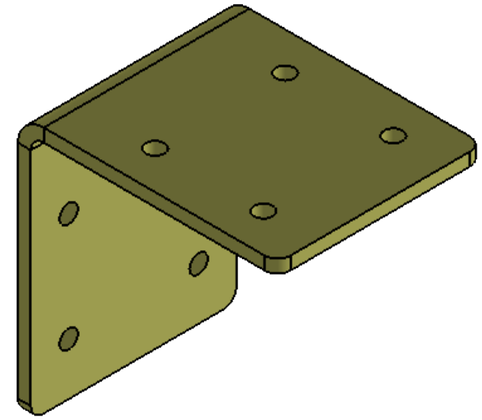

NOTE -


FOR ALL PANEL THIS L ANGLE PLATE IS USED

LASER CUTTING


DEVELOPMENT VIEW

TITLE - RETRACTABLE ROOF				NIHVA TECHNOLOGIES PVT.LTD.PUNE
DWG NO - NTPL268-PM			QTY - 1	Website - www.nihva.com
	NAME	SIGNATURE	DATE	PROJECT NO - NTPL268-PM- AD
DRAWN	S.W		03-03-2025	PRODUCT - RETRACTABLE ROOF
CHK'D	P.M.		03-03-2025	SITE LOCATION - GUJARAT
APPV'D	V.T.		03-03-2025	
if any queries contact - supportautomation@nihva.com				REVISION -
ALL DIMENSION ARE IN mm			A3	SCALE -

ITEM NO.	PART NUMBER	DESCRIPTION	QTY.
1	PROFILE L ANGLE WELDING PLATE	L ANGULAR 3 MM THK	12

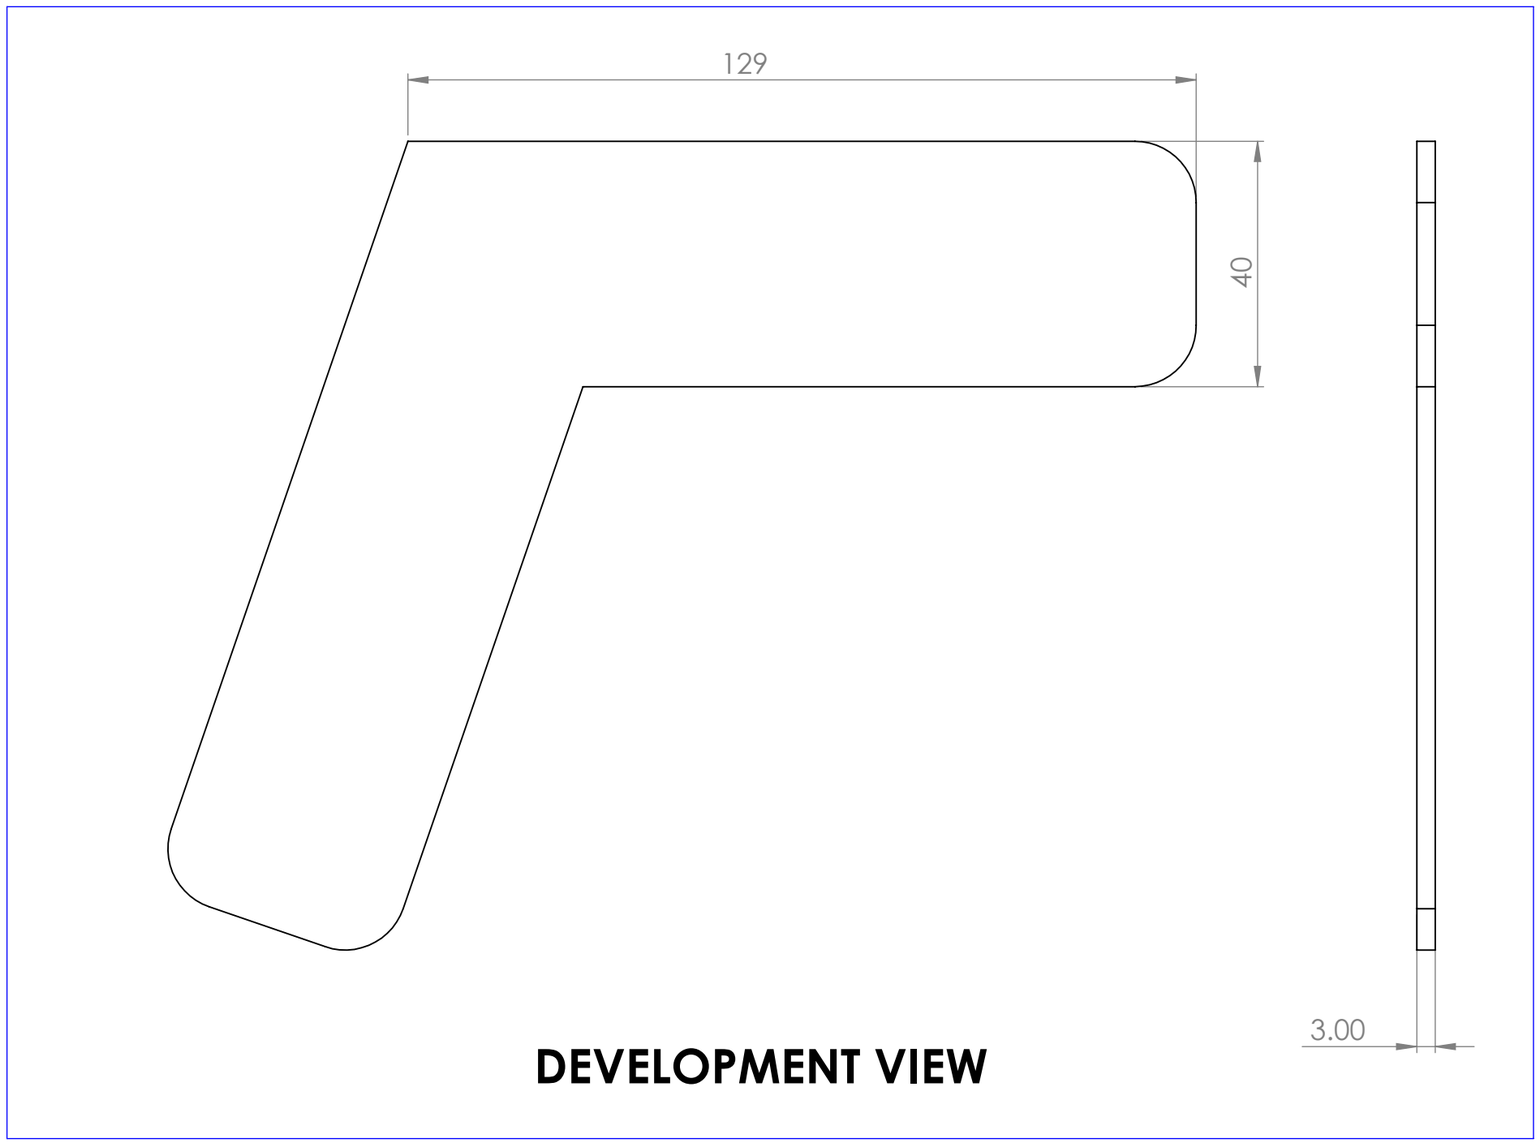

DEVELOPMENT VIEW

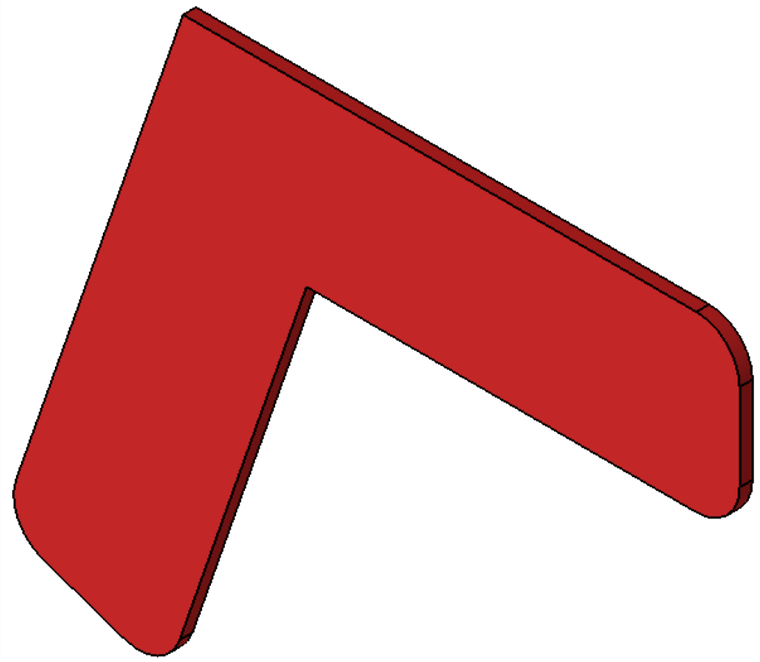


NOTE -


FOR ALL PANEL THIS L ANGULAR PLATE IS USED


LASER CUTTING


TITLE - RETRACTABLE ROOF				NIHVA TECHNOLOGIES PVT.LTD.PUNE
DWG NO - NTPL268-PM			QTY - 1	Website - www.nihva.com
	NAME	SIGNATURE	DATE	PROJECT NO - NTPL268-PM- AD
DRAWN	S.W		03-03-2025	PRODUCT - RETRACTABLE ROOF
CHK'D	P.M.		03-03-2025	SITE LOCATION - GUJARAT
APPV'D	V.T.		03-03-2025	
if any queries contact - supportautomation@nihva.com				REVISION -
ALL DIMENSION ARE IN mm			A3	SCALE -

ITEM NO.	PART NUMBER	DESCRIPTION	QTY.
1	BEARING BLOCK (T75-1B)	80X105X63 MM (VMC PART)	12

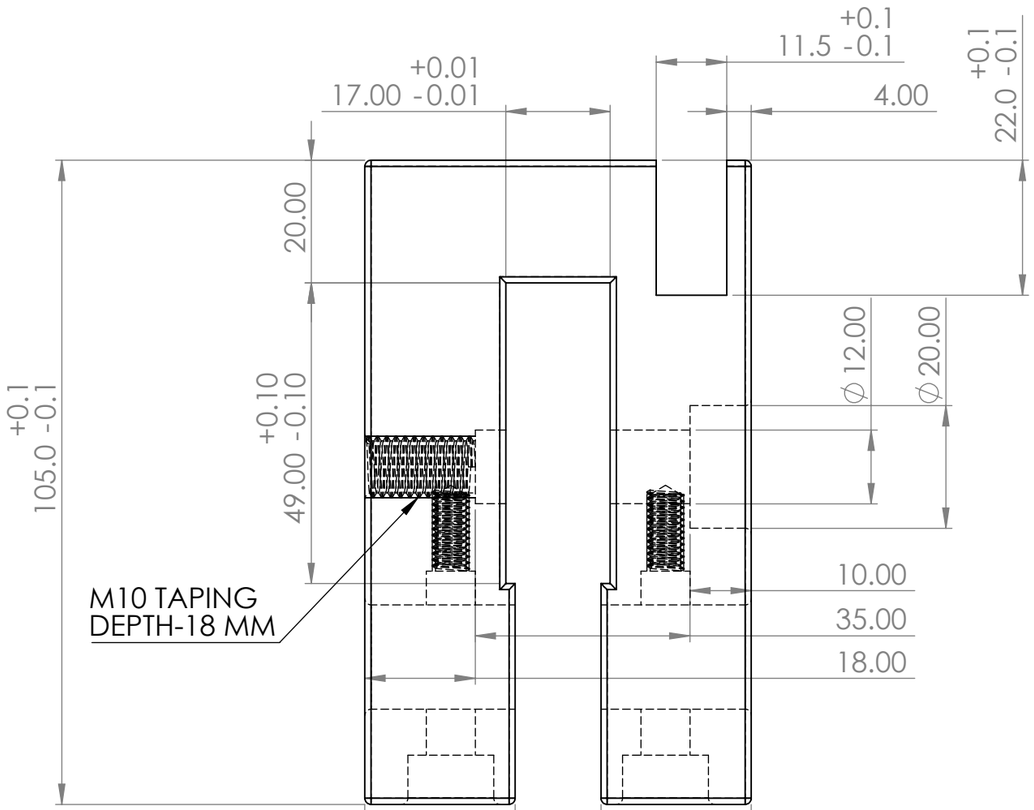

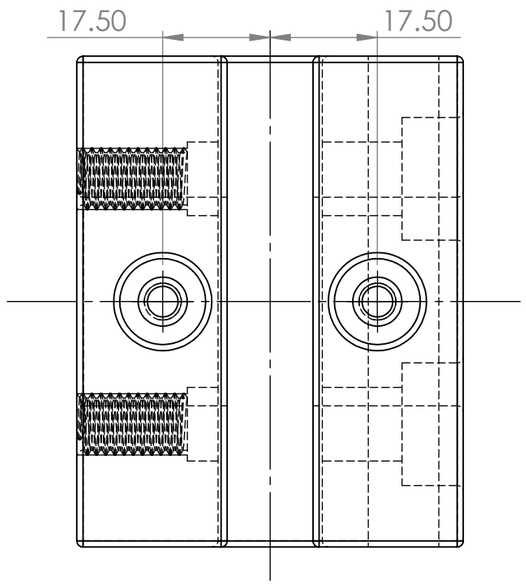

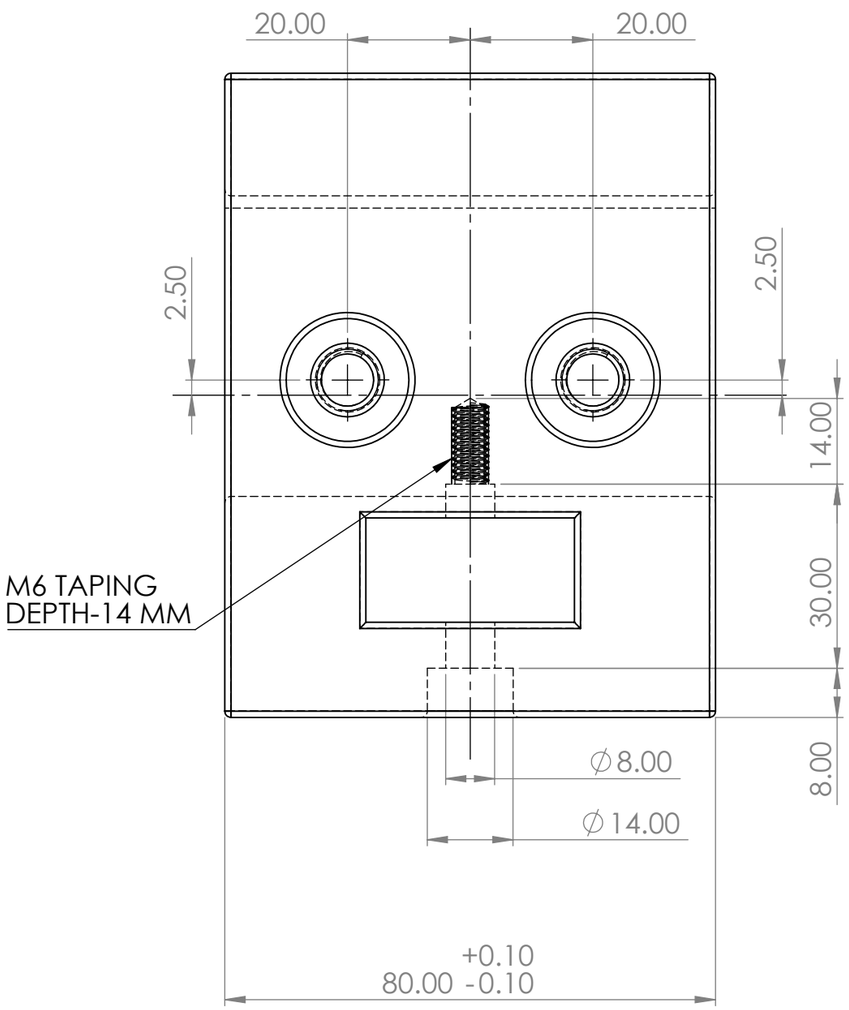

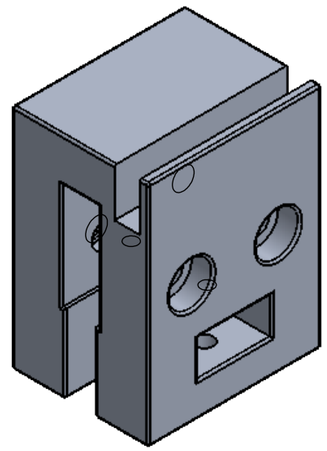


NOTE -


FOR ALL PANEL THIS BEARING BLOCK IS USED


VMC MACHINING

TITLE - RETRACTABLE ROOF				NIHVA TECHNOLOGIES PVT.LTD.PUNE
DWG NO - NTPL268-PM			QTY - 1	Website - www.nihva.com
	NAME	SIGNATURE	DATE	PROJECT NO - NTPL268-PM- AD
DRAWN	S.W		03-03-2025	PRODUCT - RETRACTABLE ROOF
CHK'D	P.M.		03-03-2025	SITE LOCATION - GUJARAT
APPV'D	V.T.		03-03-2025	
if any queries contact - supportautomation@nihva.com				REVISION -
ALL DIMENSION ARE IN mm		A3		SCALE -

ITEM NO.	PART NUMBER	DESCRIPTION	QTY.
1	ENCLOSURE NTPL-268-PM-PANEL_01	ENCLOSURE _01	1

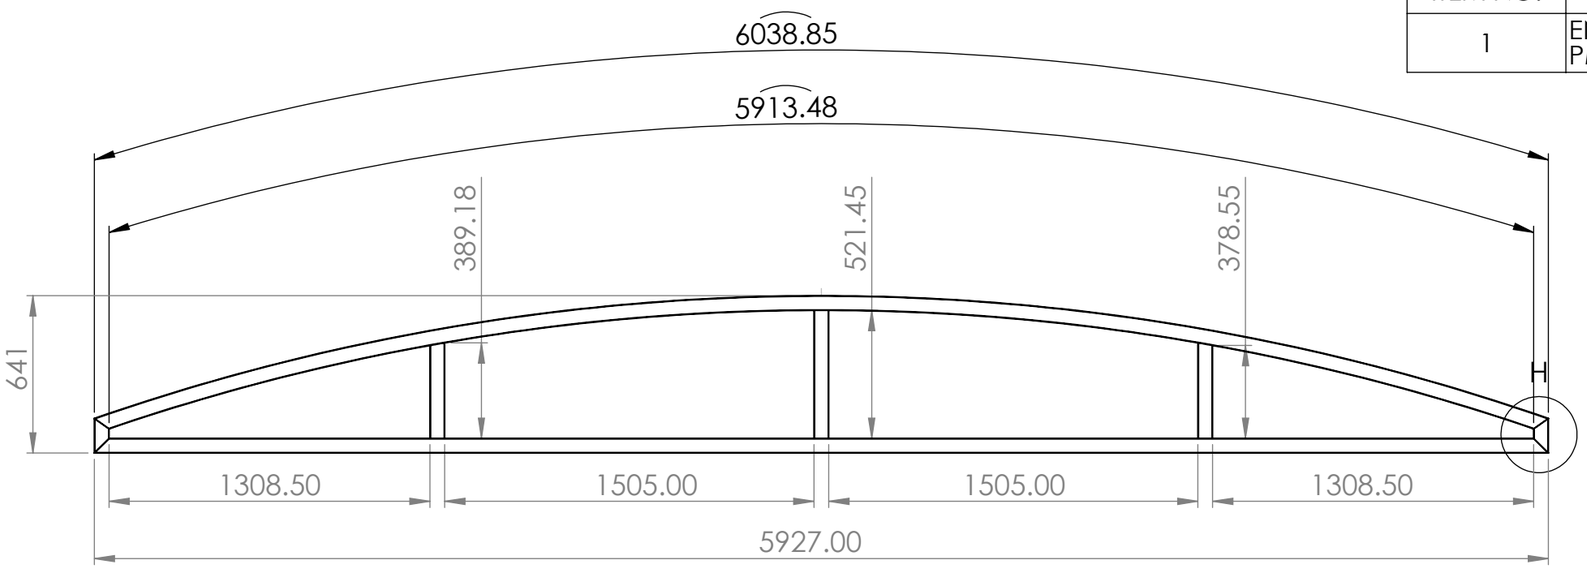

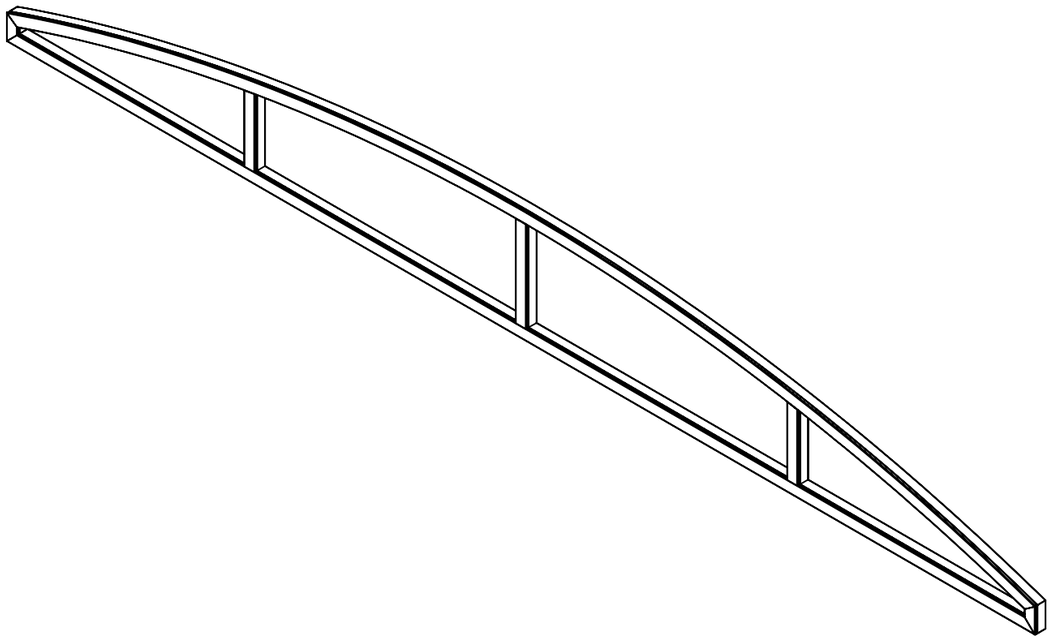

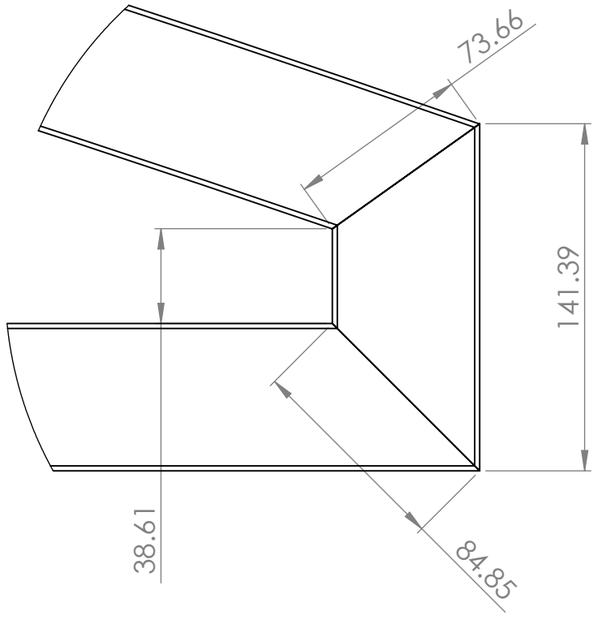


DETAIL H
SCALE 2 : 5

TITLE - RETRACTABLE ROOF				NIHVA TECHNOLOGIES PVT.LTD.PUNE Website - www.nihva.com
DWG NO - NTPL268-PM			QTY - 1	
	NAME	SIGNATURE	DATE	PROJECT NO - NTPL268-PM- AD
DRAWN	S.W		03-03-2025	PRODUCT - RETRACTABLE ROOF
CHK'D	P.M.		03-03-2025	SITE LOCATION - GUJARAT
APPV'D	V.T.		03-03-2025	
if any queries contact - supportautomation@nihva.com				REVISION -
ALL DIMENSION ARE IN mm			A3	SCALE -





ITEM NO.	PART NUMBER	DESCRIPTION	QTY.
1	NTPL-268-PM-PANEL_02	PANEL_02 FRAME	1
2	AL Support tube SQ TUBE 40X40X1.5 MM L-734 MM	AL INTERMEDIAT SUPPORT TUBE	18
3	rivet_iso_15977_4_x_16_0	RIVET M4X16	79
4	T PLATE	JOINING PLATE	4
5	L PALTE	JOINING PLATE	8
6	L ANGLE PLATE	JOINING PLATE	8
7	PROFILE L ANGLE WELDING PLATE	JOINING PLATE	4
8	BEARING BLOCK ASM WITH SHOULDER BOLT	SLIDING BLOCK	4

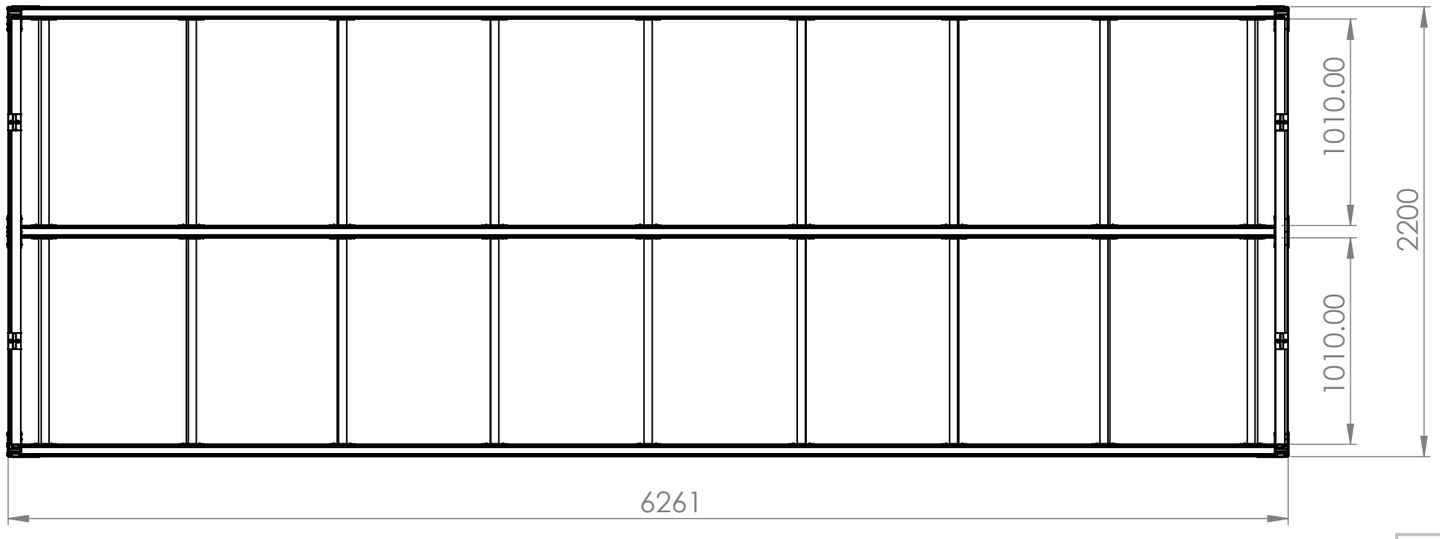


TITLE - RETRACTABLE ROOF				NIHVA TECHNOLOGIES PVT.LTD.PUNE Website - www.nihva.com
DWG NO - NTPL268-PM			QTY - 1	
	NAME	SIGNATURE	DATE	PROJECT NO - NTPL268-PM- AD
DRAWN	S.W		03-03-2025	PRODUCT - RETRACTABLE ROOF
CHK'D	P.M.		03-03-2025	SITE LOCATION - GUJARAT
APPV'D	V.T.		03-03-2025	
if any queries contact - supportautomation@nihva.com				REVISION -
ALL DIMENSION ARE IN mm			A3	SCALE - SHEET 12 OF 16


ITEM NO.	PART NUMBER	DESCRIPTION	QTY.
1	NTPL-268-PM-PANEL_02	PANEL_02 FRAME	1

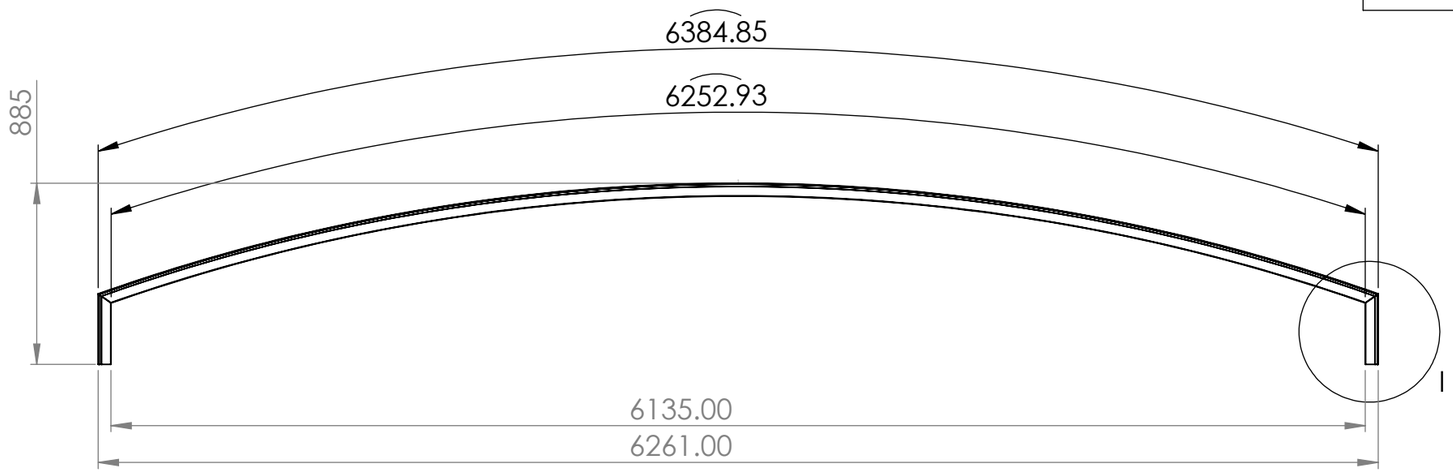

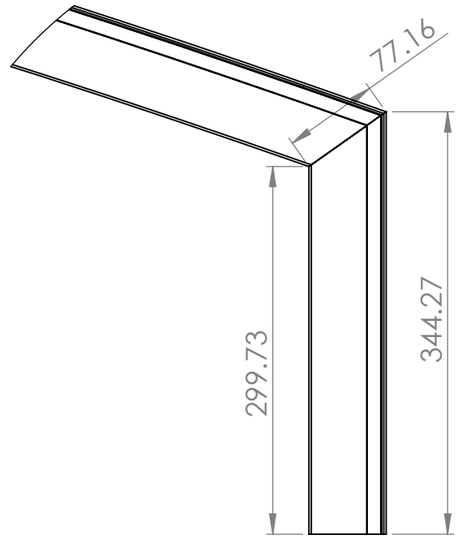

DETAIL I
SCALE 1 : 5

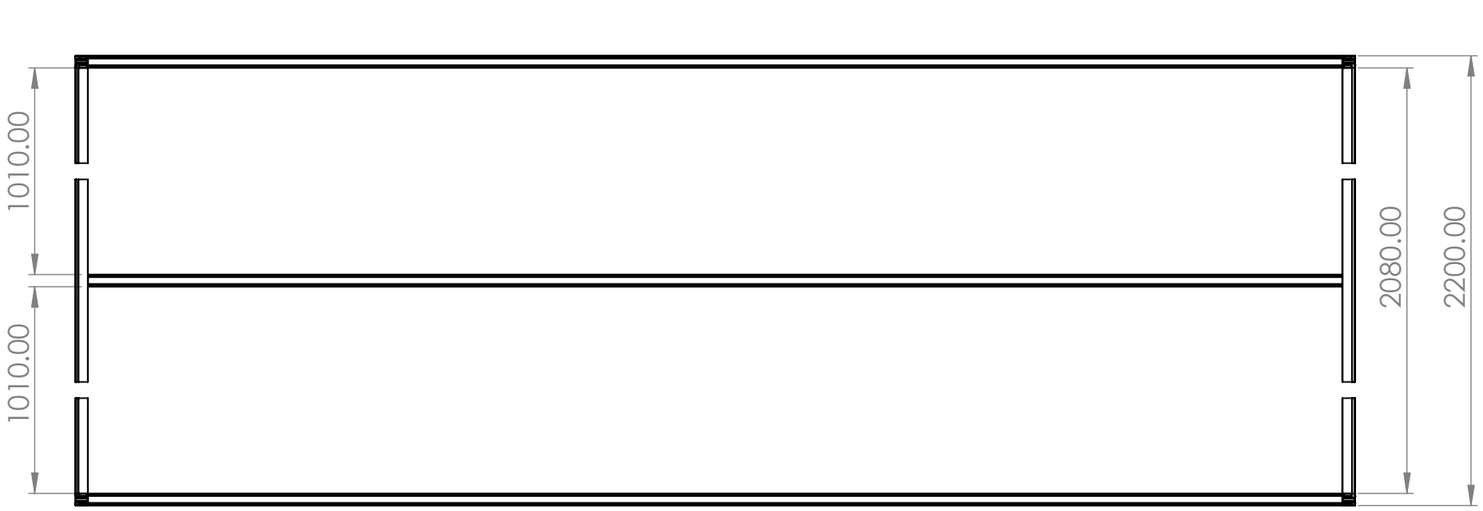


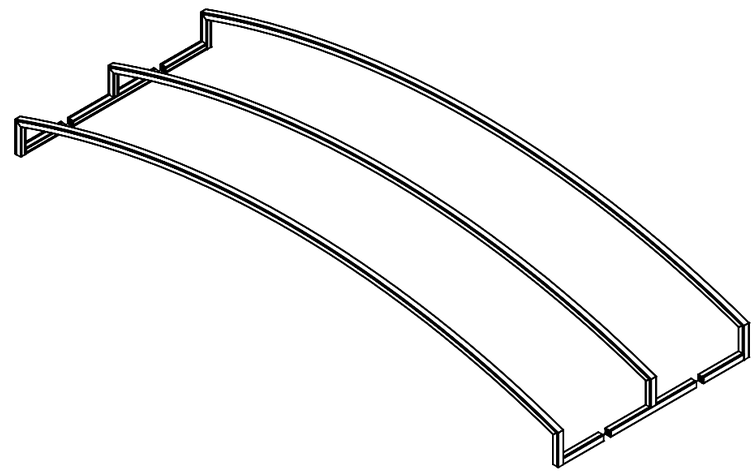



PANEL_02

TITLE - RETRACTABLE ROOF				NIHVA TECHNOLOGIES PVT.LTD.PUNE Website - www.nihva.com
DWG NO - NTPL268-PM			QTY - 1	
	NAME	SIGNATURE	DATE	PROJECT NO - NTPL268-PM- AD
DRAWN	S.W		03-03-2025	PRODUCT - RETRACTABLE ROOF
CHK'D	P.M.		03-03-2025	SITE LOCATION - GUJARAT
APPV'D	V.T.		03-03-2025	
if any queries contact - supportautomation@nihva.com				REVISION -
ALL DIMENSION ARE IN mm			A3	SCALE - SHEET 13 OF 16

ITEM NO.	PART NUMBER	DESCRIPTION	QTY.
1	NTPL-268-PM-PANEL_03	PANEL_03 FRAME	1
2	AL Support tube SQ TUBE 40X40X1.5 MM L-734 MM	AL INTERMEDIAT SUPPORT TUBE	18
3	rivet_iso_15977_4_x_16_0	RIVET M4X16	79
4	T PLATE	JOINING PLATE	4
5	L PALTE	JOINING PLATE	8
6	L ANGLE PLATE	JOINING PLATE	8
7	PROFILE L ANGLE WELDING PLATE	JOINING PLATE	4
8	BEARING BLOCK ASM WITH SHOULDER BOLT	SLIDING BLOCK	4
9	ENCLOSURE NTPL-268-PM-PANEL_03	ENCLOSURE _03	1

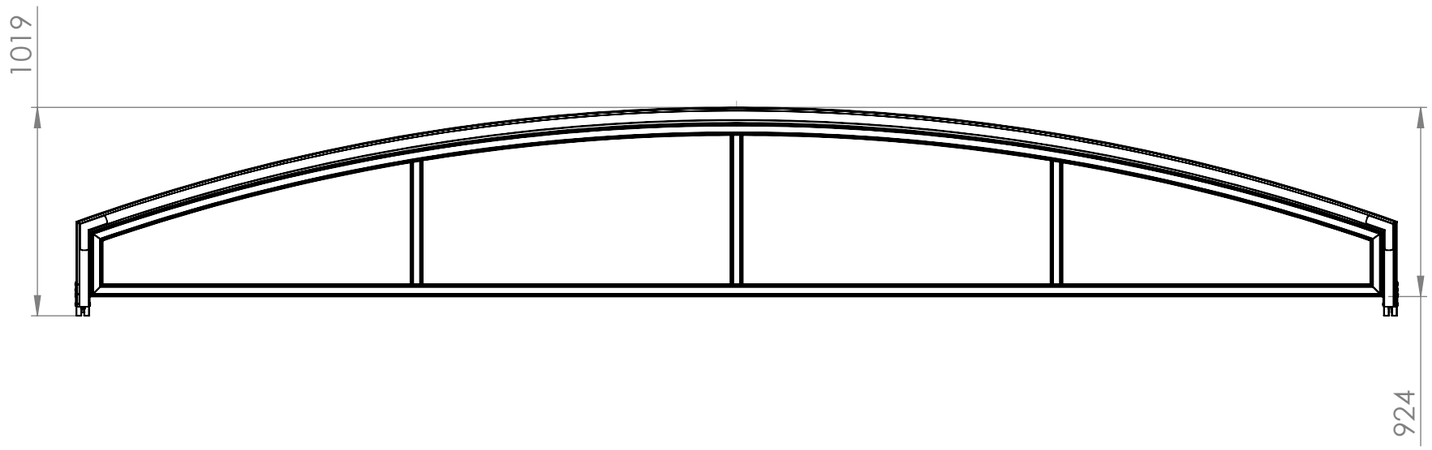


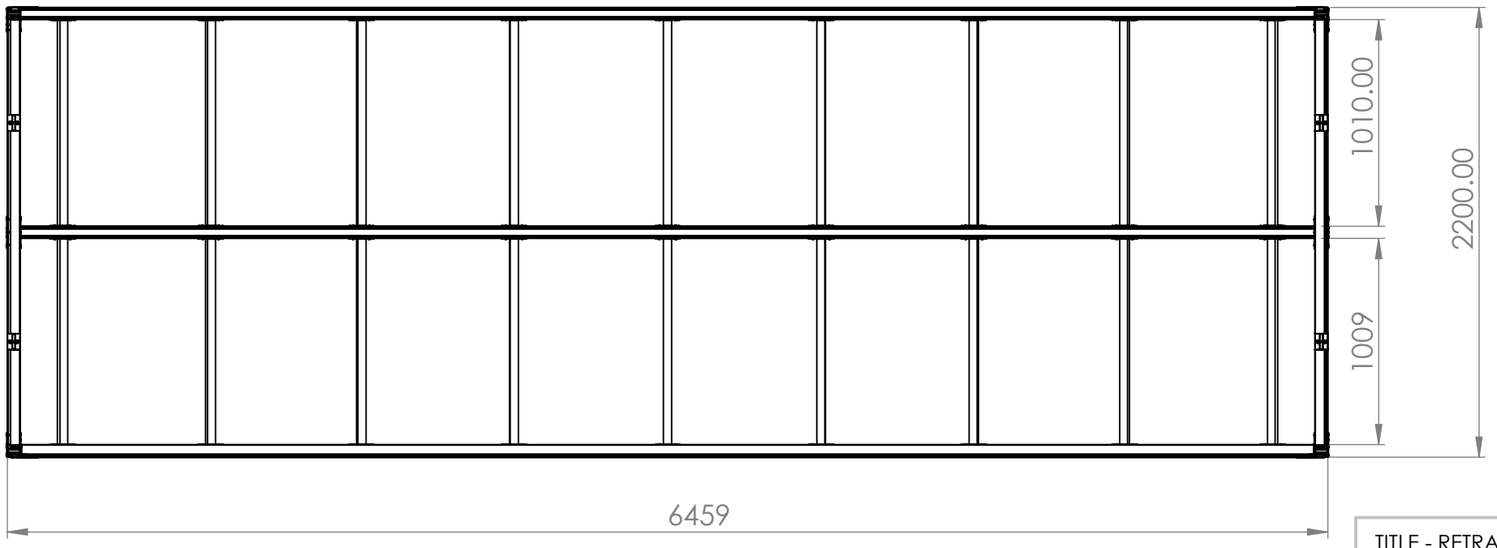


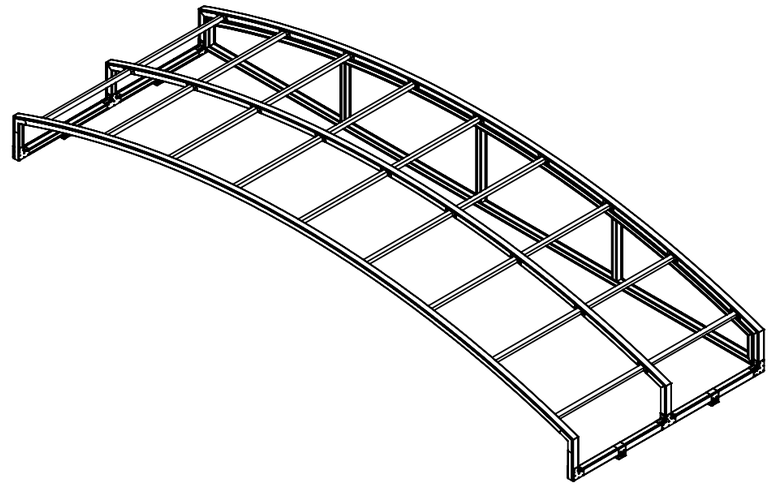


TITLE - RETRACTABLE ROOF				NIHVA TECHNOLOGIES PVT.LTD.PUNE
DWG NO - NTPL268-PM			QTY - 1	Website - www.nihva.com
	NAME	SIGNATURE	DATE	PROJECT NO - NTPL268-PM- AD
DRAWN	S.W		03-03-2025	PRODUCT - RETRACTABLE ROOF
CHK'D	P.M.		03-03-2025	SITE LOCATION - GUJARAT
APPV'D	V.T.		03-03-2025	
if any queries contact - supportautomation@nihva.com				REVISION -
ALL DIMENSION ARE IN mm			A3	SCALE - SHEET 14 OF 16


ITEM NO.	PART NUMBER	DESCRIPTION	QTY.
1	NTPL-268-PM-PANEL_03	PANEL_03 FRAME	1

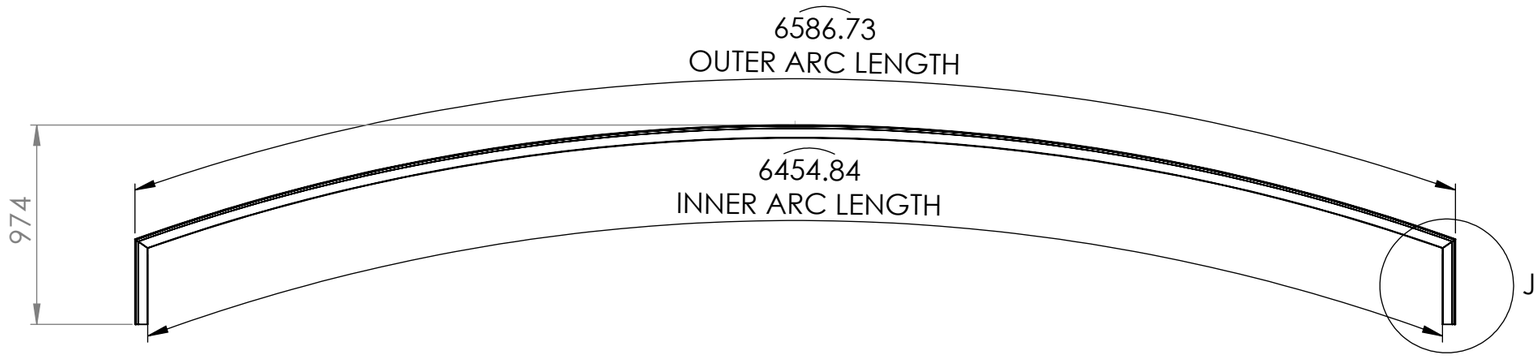

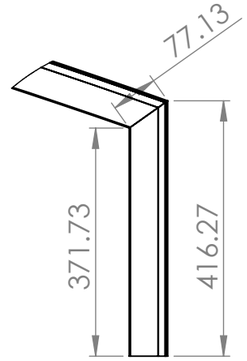

DETAIL J
SCALE 1 : 10

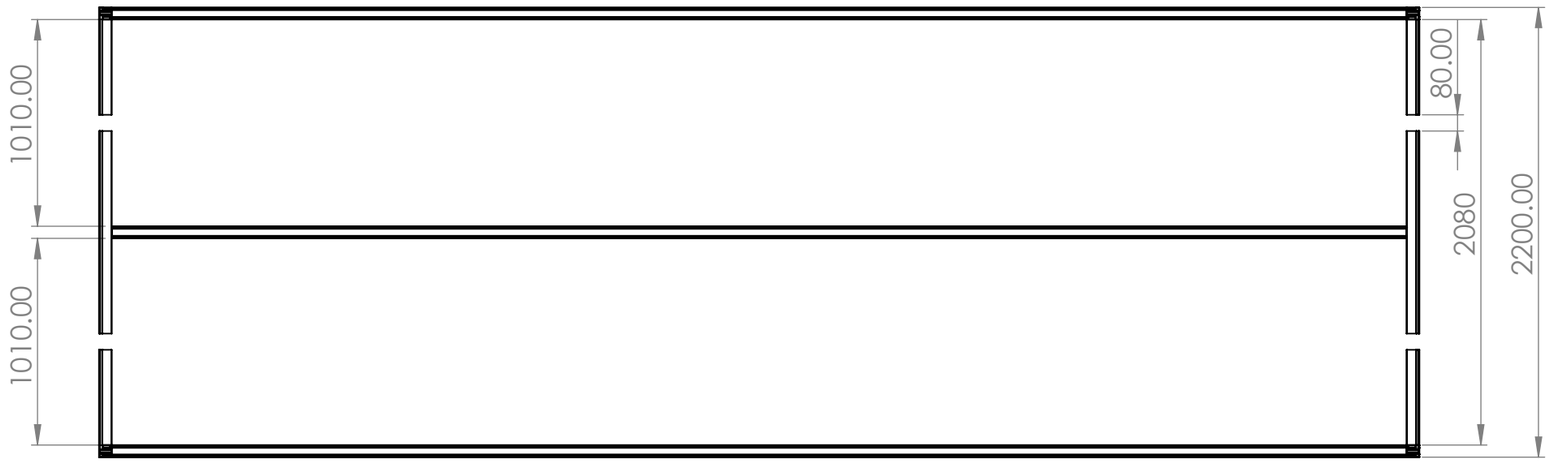

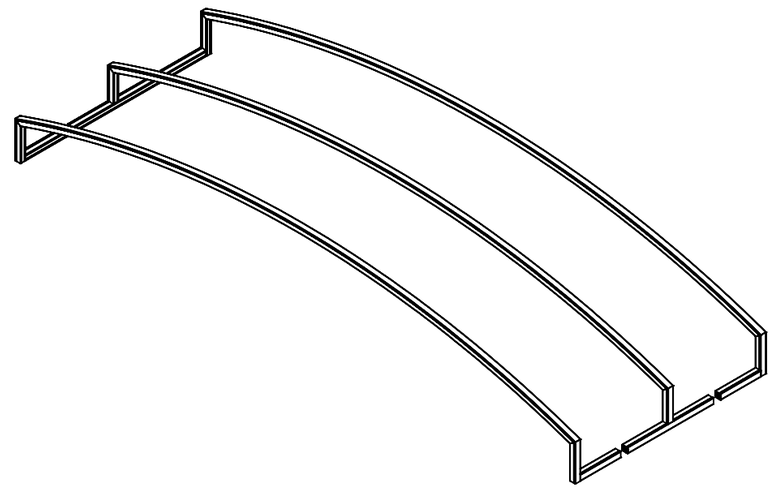



PANEL_03

TITLE - RETRACTABLE ROOF				
DWG NO - NTPL268-PM			QTY - 1	
	NAME	SIGNATURE	DATE	PROJECT NO - NTPL268-PM- AD
DRAWN	S.W		03-03-2025	PRODUCT - RETRACTABLE ROOF
CHK'D	P.M.		03-03-2025	SITE LOCATION - GUJARAT
APPV'D	V.T.		03-03-2025	
if any queries contact - supportautomation@nihva.com				REVISION -
ALL DIMENSION ARE IN mm			A3	SCALE - SHEET 15 OF 16


NIHVA TECHNOLOGIES PVT.LTD.PUNE
Website - www.nihva.com

ITEM NO.	PART NUMBER	DESCRIPTION	QTY.
1	ENCLOSURE NTPL-268-PM-PANEL_03	ENCLOSURE _03	1

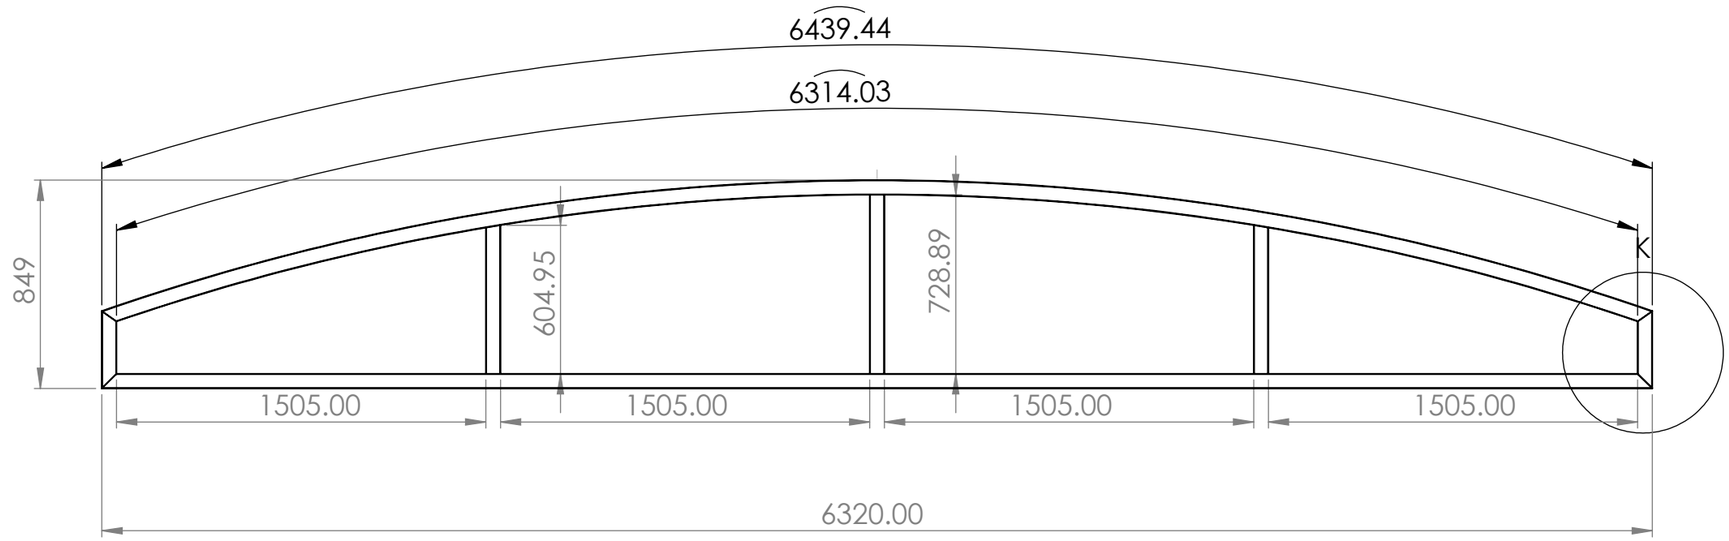

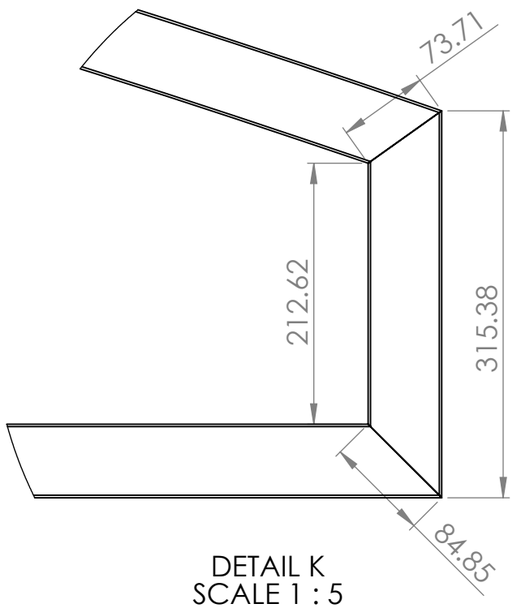

DETAIL K
SCALE 1 : 5

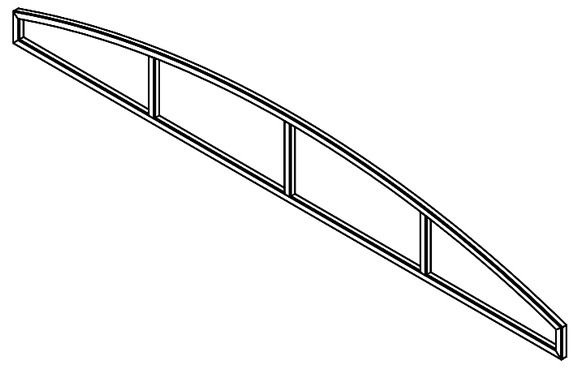

TITLE - RETRACTABLE ROOF				NIHVA TECHNOLOGIES PVT.LTD.PUNE Website - www.nihva.com
DWG NO - NTPL268-PM			QTY - 1	
	NAME	SIGNATURE	DATE	PROJECT NO - NTPL268-PM- AD
DRAWN	S.W		03-03-2025	PRODUCT - RETRACTABLE ROOF
CHK'D	P.M.		03-03-2025	SITE LOCATION - GUJARAT
APPV'D	V.T.		03-03-2025	
if any queries contact - supportautomation@nihva.com				REVISION -
ALL DIMENSION ARE IN mm			A3	SCALE - SHEET 16 OF 16