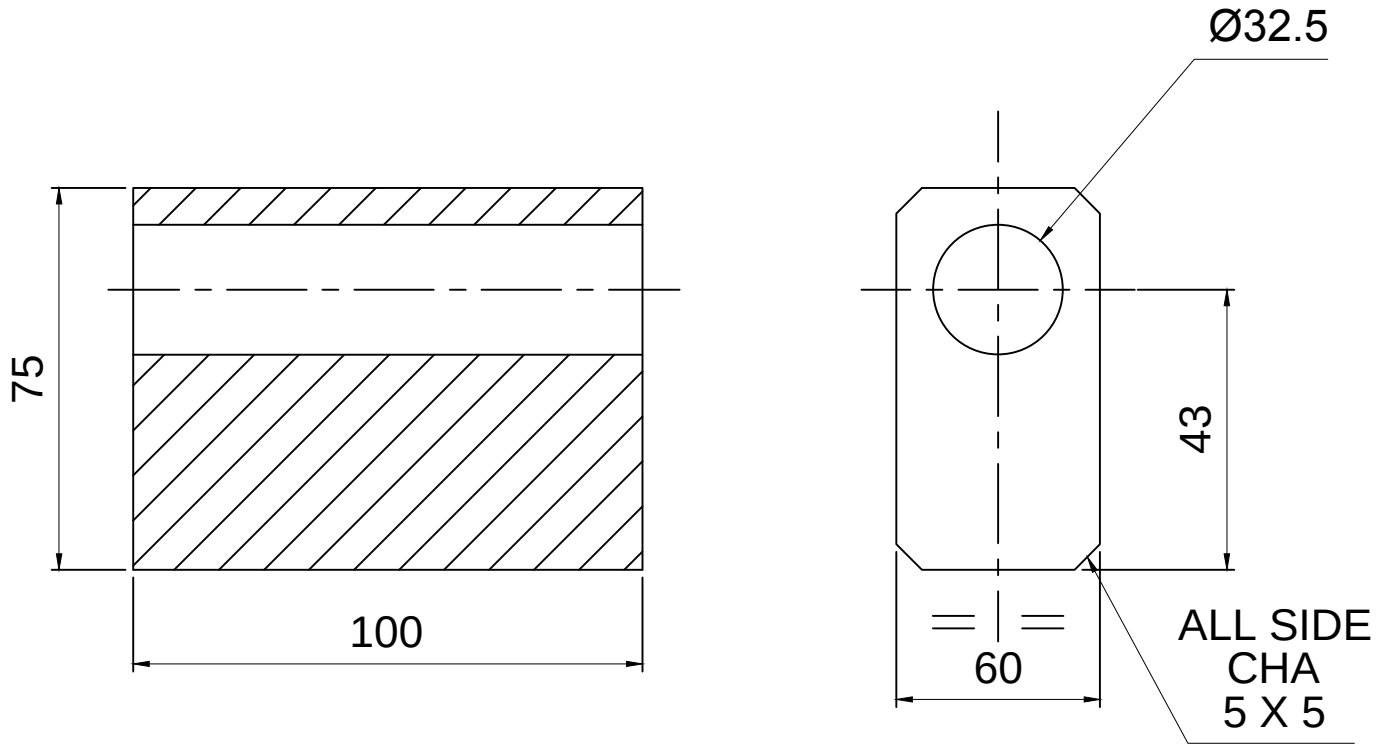


BACK SIDE HINGE BLOCK = 5 NOS
MTL = M.S
75 X 60 THK X 100L = 5 NOS

This drawing & design is the property of NIHVA TECHNOLOGIES. Not to be sold or copied to any other concern.

TITLE: BACK SIDE HINGE BLOCK				NIHVA TECHNOLOGIES PVT. LTD. PUNE Tel : 020 66304033 Email:- info@nihva.com Website:- www.nihva.com	
	NAME	SIGN	DATE		
DRAWN	P.V.A		28.06.2019	CLIENT -	
CHECK	V.M.T		28.06.2019	PROJECT - NDL456	
APPRD.				SITE LOCATION -	
If any queries contact : design@nihva.com				DWG. NO. : NIHVA/19-20/VDR/082	
ALL DIMENSION ARE IN mm				SCALE: NTS	WT: REV- 00