
15-11-16

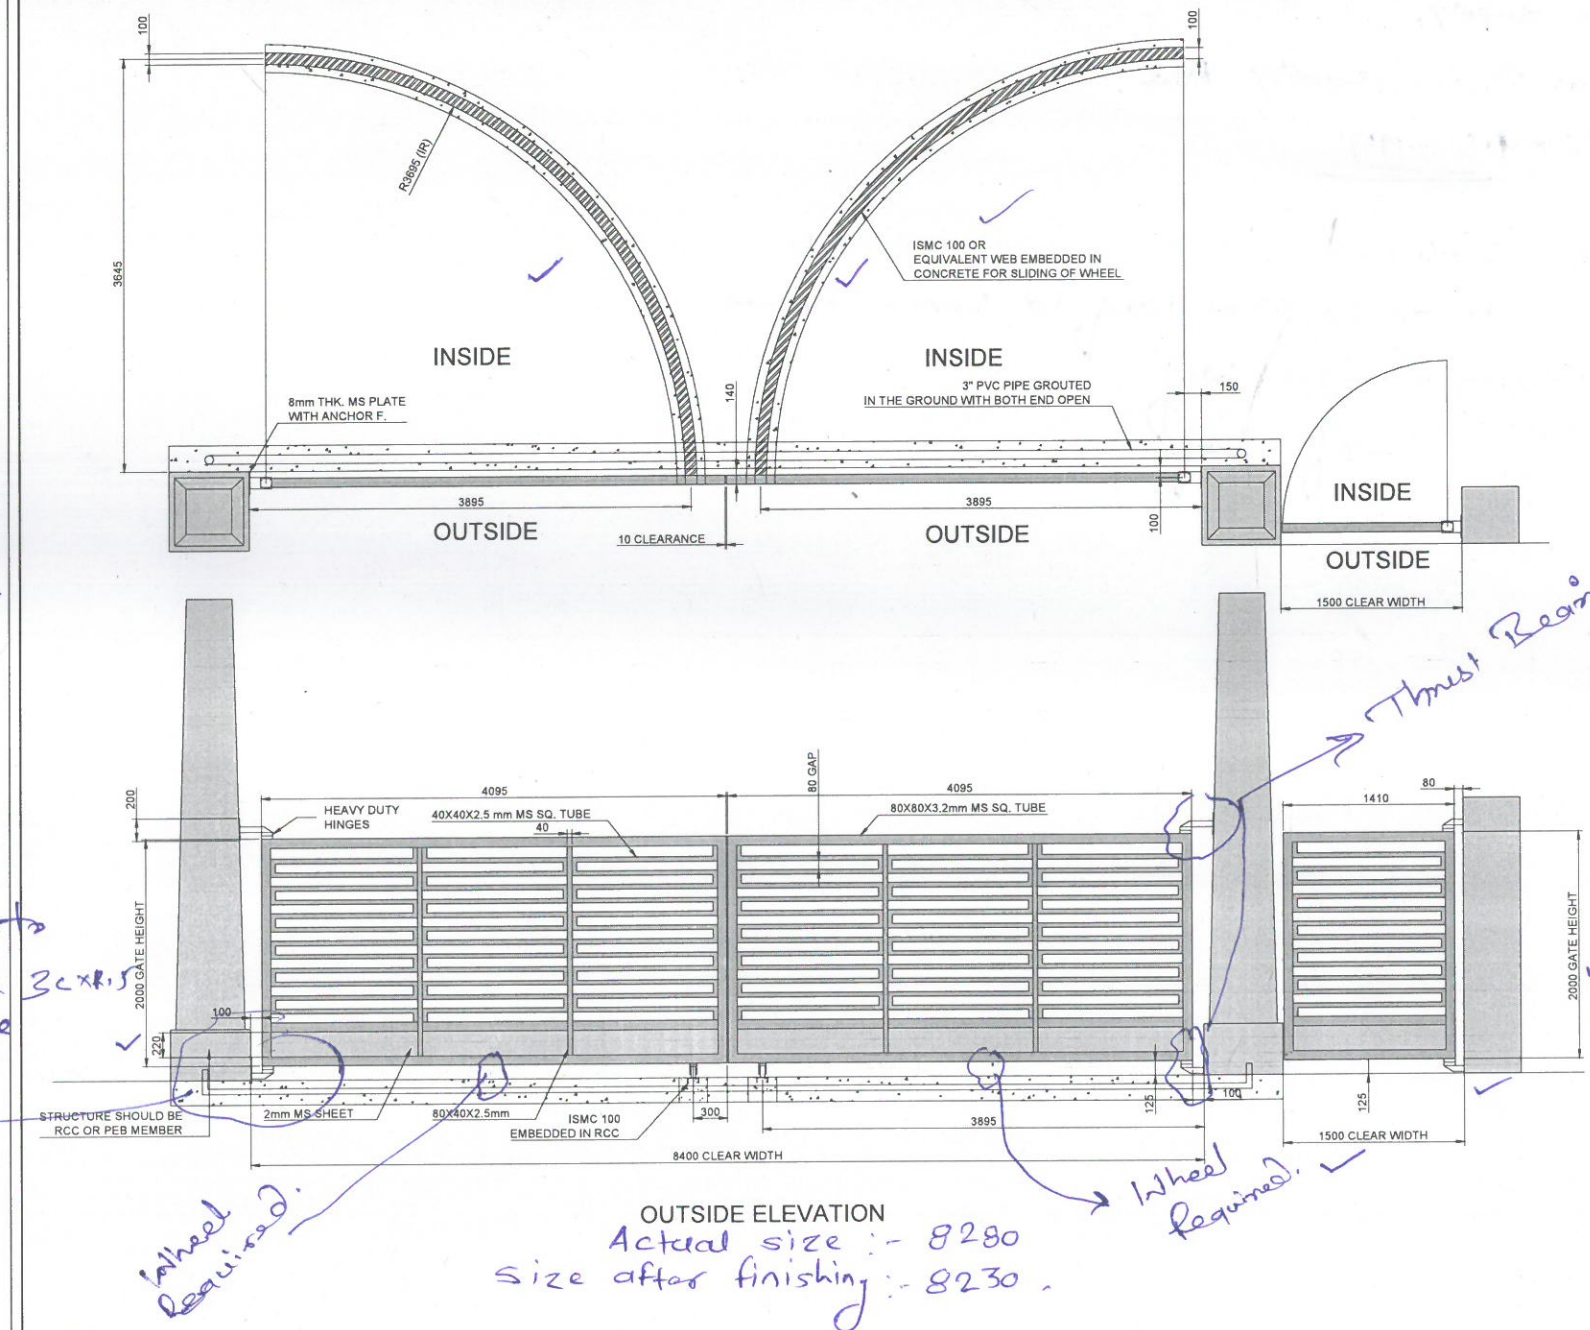

OUTSIDE ELEVATION

Actual size :- 8280

Size after finishing :- 8230.

M/S NIHVA TO arrange for grouting 'C' Channel on top Priority.

M/S NIHVA TO select necessary members to convert these door into Automatic door.

DIMENSION :

CLEAR WIDTH	CLEAR HEIGHT	QUANTITY
8400 mm	2000 mm	01 NOS.
1500 mm	2000 mm	01 NOS.

MATERIAL :

THICKNESS :

MODIFICATIONS DONE:-

1.GATE SHIFTED TOWARD INSIDE FOR UPGRADE TO AUTOMATIC SWING DOOR IN FUTURE.

2. 3 INCH PVC PIPE SHOULD BE PROVIDED IN GROUND FOR INTEGRATION OF SWING DOOR.

NIHVA
NIHVA TECHNOLOGIES PVT. LTD.

NIHVA TECHNOLOGY
PVT. LTD. PUNE
Email:- info@nihva.com
Website:- www.nihva.com

TITLE:

MANUAL SWING GATE & WICKET GATE

CLIENT'S APPROVAL :

DRJ 15/11/16

CLIENT - LUPIN LIMITED

PROJECT -

SITE LOCATION - SIKKIM

DWG. NO. : NIHVA/16-17/0098/R02

SCALE: 1:1	WT:	SHEET:1 OF 1
DRAWN BY: OMKAR		DATE: 08-11-2016
CHECK : ANIL		DATE: 08-11-2016

If any queries contact : projects@nihva.com

NOTE: ALL DIMENSION ARE IN mm

THIS DRAWING & DESIGNING IS THE PROPERTY OF NIHVA TECHNOLOGIES. NOT BE SOLD OR COPY TO ANY OTHER CONCERN.