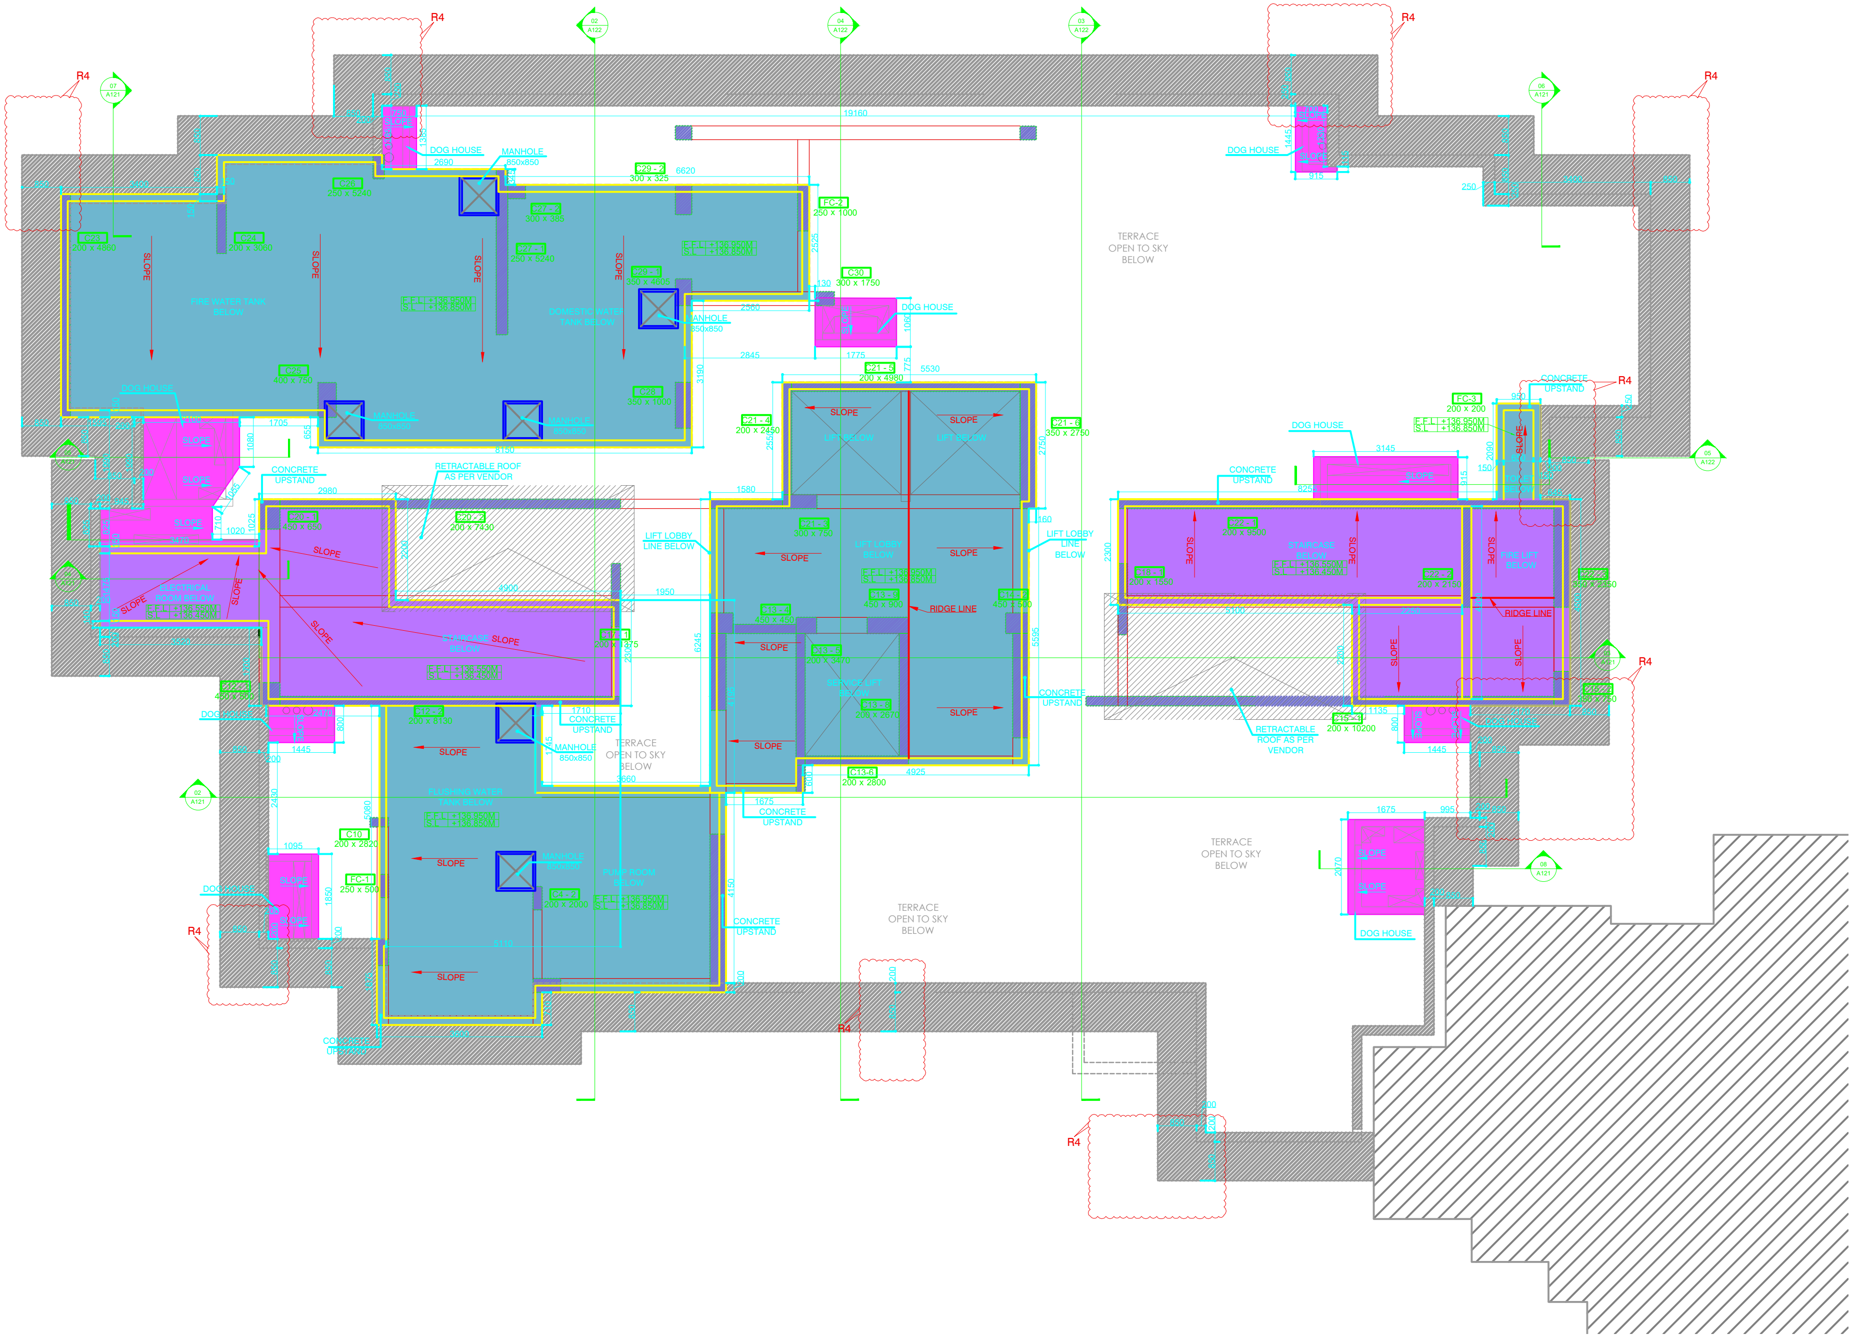
R4
07 A121
02 A122
04 A122
03 A122
06 A121
05 A122
08 A121
02 A121
19160
DOG HOUSE
MANHOLE 850x850
2690
C29 - 2 300 x 325
6620
FC-2 250 x 1000
C26 250 x 5240
C23 200 x 4860
C24 200 x 3060
C27 - 2 300 x 385
C27 - 1 250 x 5240
C29 - 1 350 x 4605
C25 400 x 750
C28 350 x 1000
C30 300 x 1750
SLOPE
FIRE WATER TANK BELOW
DOMESTIC WATER TANK BELOW
E.F.L +136.950M
S.L +136.850M
2560
2845
1775
3190
8150
1705
2980
C21 - 5 200 x 4980
5530
C21 - 4 200 x 2450
C21 - 6 350 x 2750
C21 - 3 300 x 750
LIFT BELOW
LIFT LOBBY BELOW
LIFT LOBBY LINE BELOW
TERRACE OPEN TO SKY BELOW
CONCRETE UPSTAND
RETRACTABLE ROOF AS PER VENDOR
C20 - 1 450 x 650
C20 - 2 200 x 7430
4900
1950
1580
ELECTRICAL ROOM BELOW
STAIRCASE BELOW
C17 - 1 200 x 1375
C12 - 1 450 x 500
C12 - 2 200 x 8130
1710
3660
C13 - 4 450 x 450
C13 - 9 450 x 900
C14 - 2 450 x 500
C13 - 5 200 x 3470
C13 - 8 200 x 2670
SERVICE LIFT BELOW
RIDGE LINE
C13-6 200 x 2800
4925
1675
6245
5595
FLUSHING WATER TANK BELOW
C10 200 x 2820
FC-1 250 x 500
C4 - 2 200 x 2000
PUMP ROOM BELOW
5110
4150
3470
2470
1445
1095
1850
FC-3 200 x 200
E.F.L +136.950M
S.L +136.850M
TOILET BELOW
3145
8255
C22 - 1 200 x 9500
C18 - 1 200 x 1550
E.F.L +136.550M
S.L +136.450M
C22 - 2 200 x 2150
C22 - 3 350 x 2350
FIRE LIFT BELOW
5100
2250
C15 - 1 200 x 10200
C15 - 2 350 x 750
RETRACTABLE ROOF AS PER VENDOR
1135
2120
2070
995