

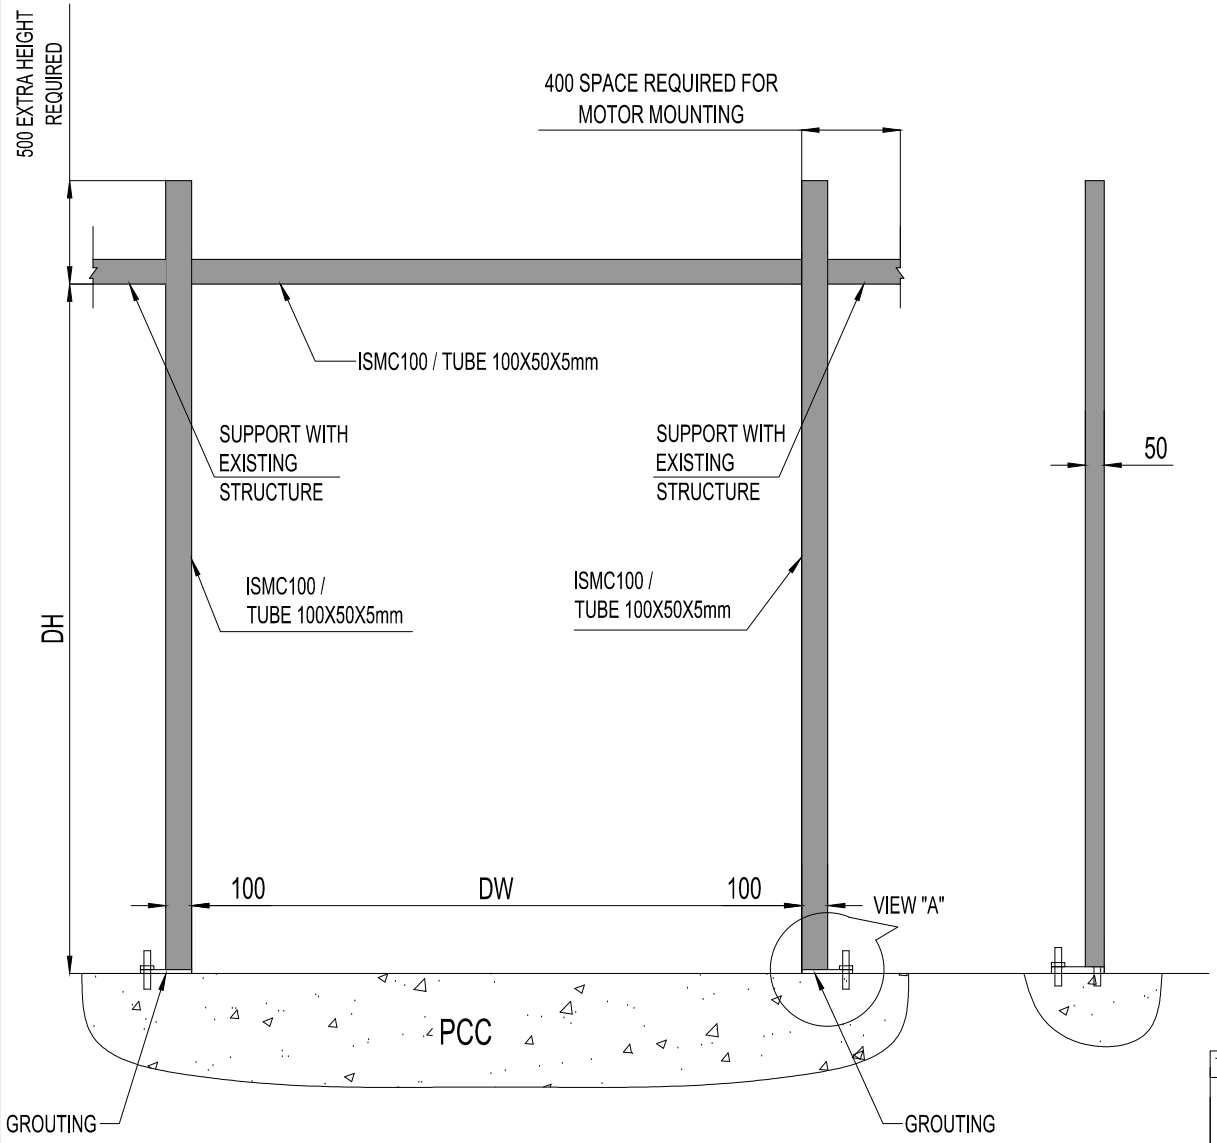


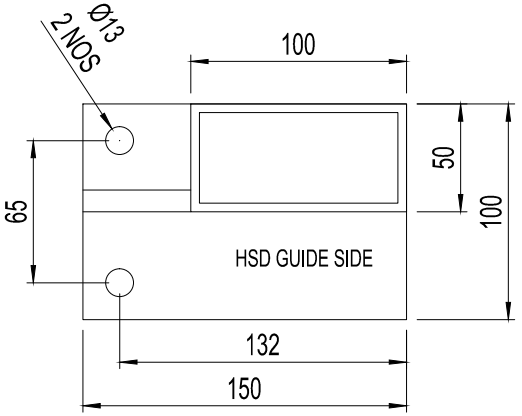

TOP VIEW

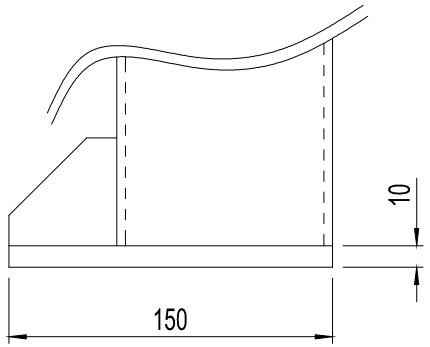

ELEVATION

DETAIL VIEW "A"

3000	2300	01 NO
CLEAR WIDTH(DW)	CLEAR HEIGHT(DH)	QTY

REV NO	DATE	DRAWN	REMARK
R01	17.06.2020	P.A	1. GROUTING PLATE DETAILS ADDED

This drawing & design is the property of NIHVA TECHNOLOGIES. Not to be sold or copied to any other concern.

TITLE: HIGH SPEED DOOR RP300 STRUCTURE

	NAME	SIGN	DATE
DRAWN	P.A		09.03.2020
CHECK	G.J		09.03.2020
APPV'ED			

If any queries contact : design@nihva.com

ALL DIMENSION ARE IN mm

NIHVA TECHNOLOGIES PVT. LTD.
NIHVA TECHNOLOGIES PVT. LTD. PUNE
Tel : 020 66304033
Email:- info@nihva.com
Website:- www.nihva.com

CLIENT :- LEAN AUTOMATION PVT LTD

PROJECT :-

LOCATION :- CHAKAN

DWG. NO. :- NIHVA/19-20/0239/R01 REV.:-R01

SCALE: NTS WT: SHEET: 01 OF 01