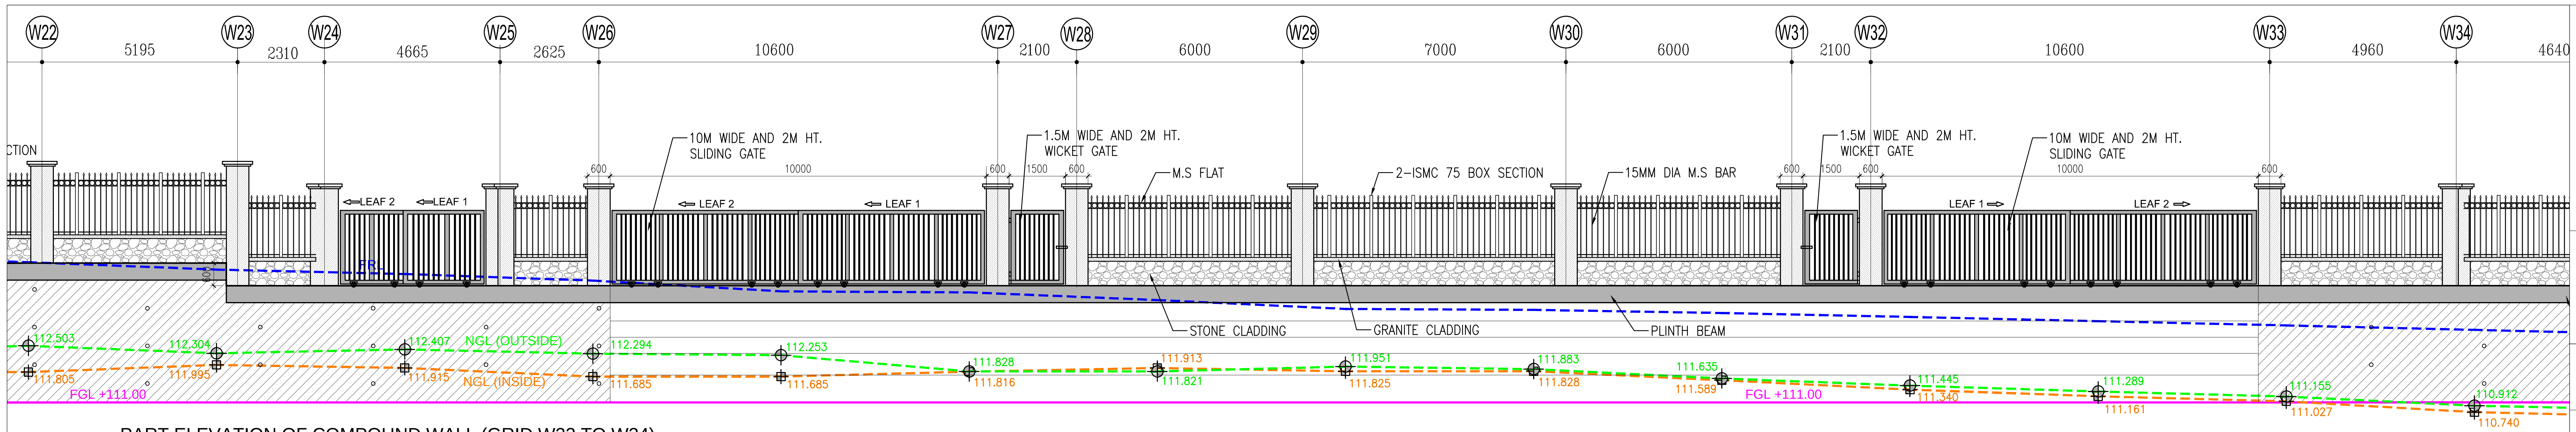

PART ELEVATION OF COMPOUND WALL (GRID W22 TO W34)

SCALE 1:100

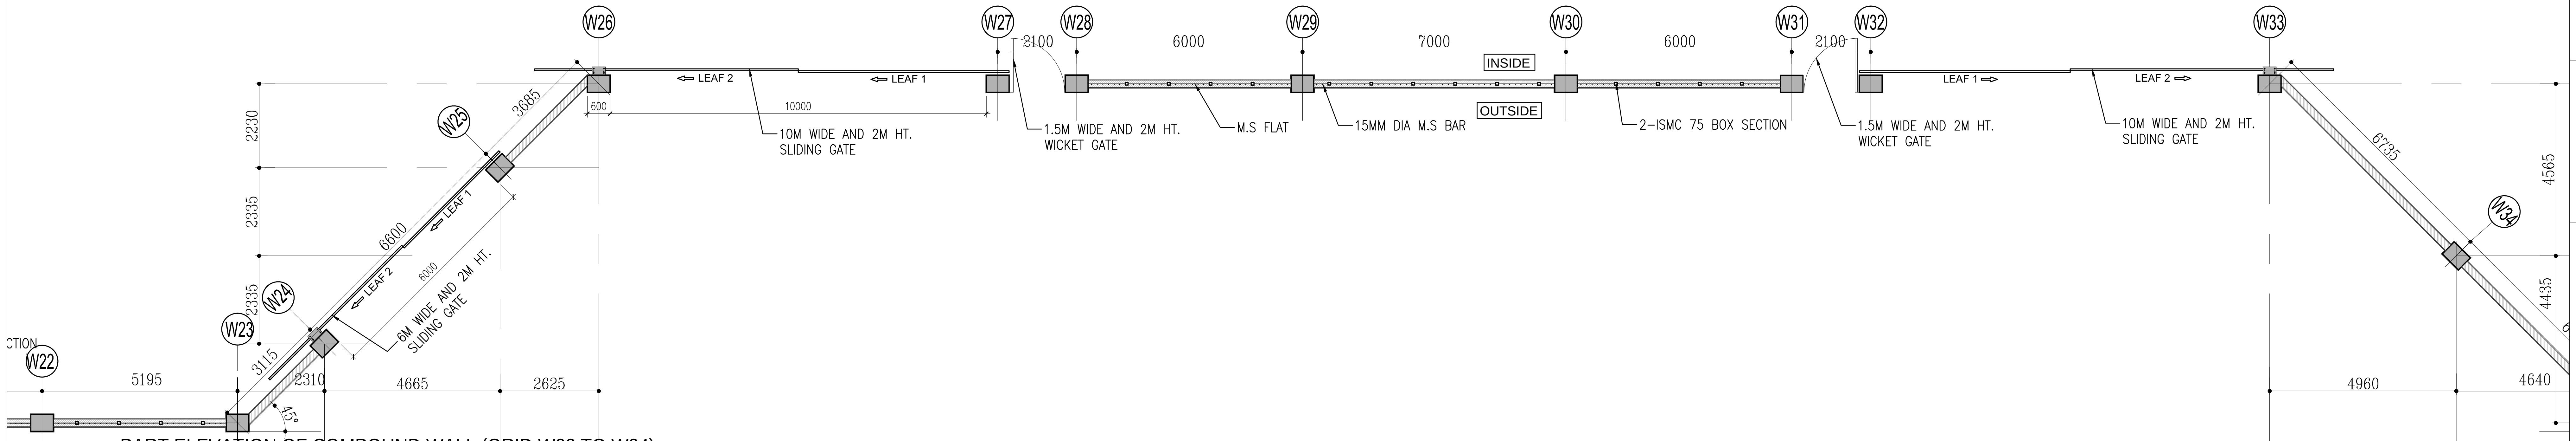

PART ELEVATION OF COMPOUND WALL (GRID W22 TO W34)

SCALE 1:100

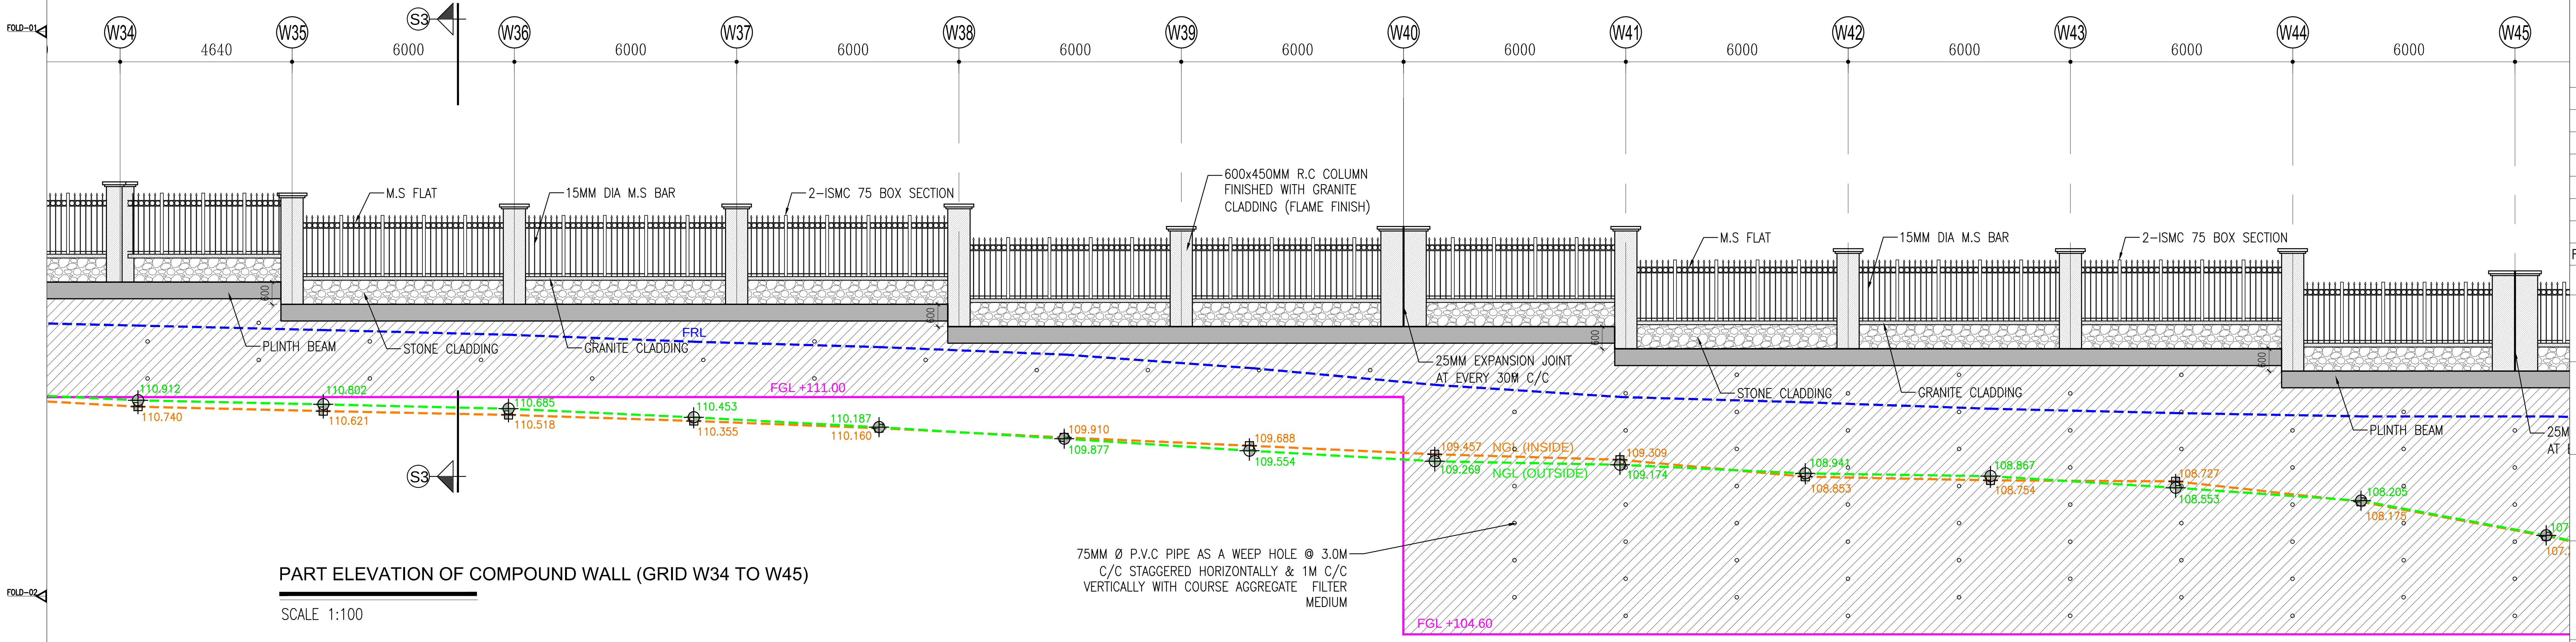

PART ELEVATION OF COMPOUND WALL (GRID W34 TO W45)

SCALE 1:100

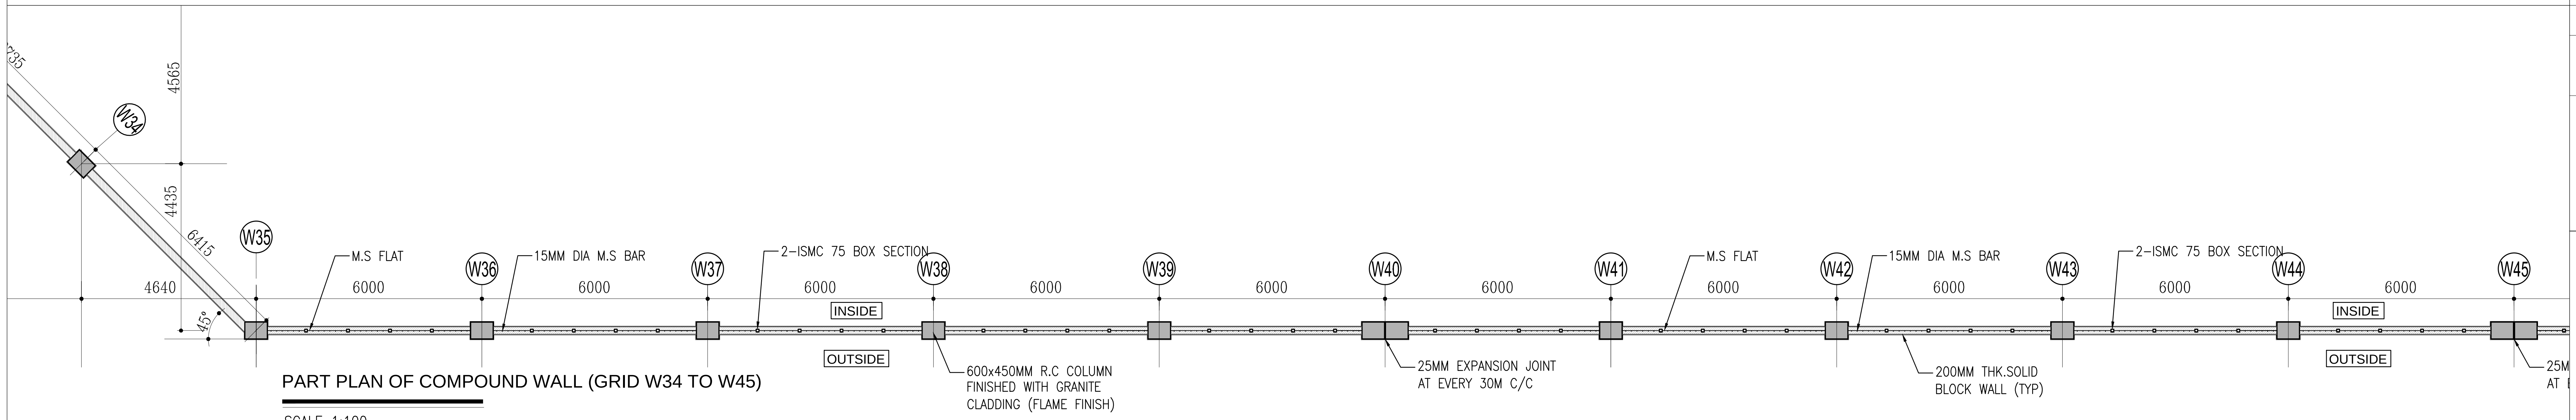
W34
W35
W36
W37
W38
W39
W40
W41
W42
W43
W44
W45
6735
4565
4435
6415
4640
45°
6000
M.S FLAT
15MM DIA M.S BAR
2-ISMC 75 BOX SECTION
INSIDE
OUTSIDE
600x450MM R.C COLUMN FINISHED WITH GRANITE CLADDING (FLAME FINISH)
25MM EXPANSION JOINT AT EVERY 30M C/C
200MM THK.SOLID BLOCK WALL (TYP)
FOLD-03
FOLD-04

PART PLAN OF COMPOUND WALL (GRID W34 TO W45)

SCALE 1:100

KEY PLAN :-

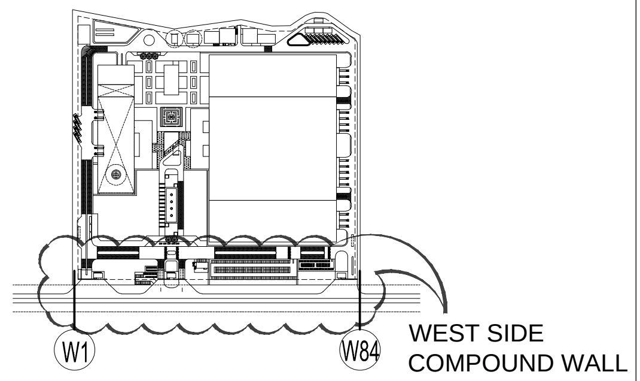

LEGEND :-

- ■ R.C.C COLUMN/PLINTH BEAM
- ▨ 200mm THICK SOLID BLOCK WALL

N

NOTE:-

25MM EXPANSION JOINT AT EVERY 30M C/C

NOTE:-

- FRL - FORMED ROAD LEVEL
- FGL - FORMED GROUND LEVEL
- NGL - NATURAL GROUND LEVEL (OUTSIDE)
- NGL - NATURAL GROUND LEVEL (INSIDE)

LEGEND :-

- ☐ GRANITE CLADDING FOR COLUMN
- ▨ GRANITE CLADDING FOR COMPOUND WALL
- ▩ STONE PITCHING

Construction work shall be executed only as per the latest revision drawing. Once a revision drawing is issued, the validity of the previous revision drawing stands cancelled and as such construction shall not be carried out as per superseded revisions. The Contractor is expected to:
1. Maintain a register of Drawing Receipts, listing drawing number & revision number, title, from whom received, date received, number of copies received, details of transmittal from the issuer & any other relevant details to be advised from time to time.
2. Archive all previous revision issues immediately upon receipt of a new revision and no superseded drawing shall remain in the site of works except in the Contractor's archives for record and reference purposes only.
3. While archiving superseded drawing, the Contractor is expected to stamp all previously issued drawings / prints appropriately, mentioning the date and revision number of the new revision on account of which the previous revision is archived.
4. The Contractor shall allow the reprerentative of Client / PMC / Architect to inspect Contractor's archives for ensuring compliance.
5. Any work carried out by the Contractor using a superseded drawing after the issue of a new revision is liable for rejection and reinstatement as per new revision at Contractor's risk and cost without any entitlement to extension of time

REV.	DESCRIPTION	DATE	BY	CHD.
T1	ISSUED FOR SITE DEVELOPMENT TENDER	10.11.17	AM	GBK

AMENDMENT

GRAPHIC SCALE:
0 0.50M 2.50M 4.50M
0.50M 0 1.50M 3.50M 5.50M

CLIENT:

Emerson Process Management India private Limited, Pune

PROJECT:

Proposed Manufacturing facility for Emerson at Chakan, Pune

DRAWING TITLE:

WEST SIDE COMPOUND WALL
PART PLAN, ELEVATION AND
SECTION DETAILS

SHEET 2 OF 5

SCALE : 1:100
DRAWN : A.MALATHI
DATE : 18.09.17
CHKD : G.BERNARD
REV

DRAWING NO:
EPMIPL-P-SITE-AR00-04-00-226443
T1

PROJECT MANAGEMENT:

CBRE South Asia Pvt. Ltd | Project Management Group - Pune
3rd Floor, East Wing | Nyati Unitree
Samrat Ashok Marg (Nagar Road)
Yerwada | Pune 411 006 - India
T (91 20) 40190 100 | F (91 20) 2605 5405

design | interiors | engineering | construction management

C.R.Narayana Rao (Consultants) Private Limited

No. 10, Karpagambal Nagar,
Mylapore, Chennai-600 004.
India.
www.crn.co.in

THESE DRAWINGS ARE UNDER COPYRIGHT AND ARE THE PROPERTY OF CRN. NONE OF THE DRAWINGS AND RELATED DOCUMENTS CAN BE REPRODUCED, COPIED IN WHOLE OR IN PART WITHOUT PRIOR EXPRESSED WRITTEN CONSENT OF CRN. THESE DRAWINGS CANNOT BE HANDED OVER TO A THIRD PARTY OR USED FOR ANY PURPOSE, OTHER THAN THAT FOR WHICH IT HAS BEEN LOANED. AFTER FULFILLING THE PURPOSE OF ISSUE THE DRAWINGS SHALL BE RETURNED TO CRN.

WEST SIDE COMPOUND WALL