


Abbrevation's:
WOW-Wall Opening Width
WOH-Wall Opening Height
CH- Clear Height
UC-Under Cut
FFL-Finished Floor Level

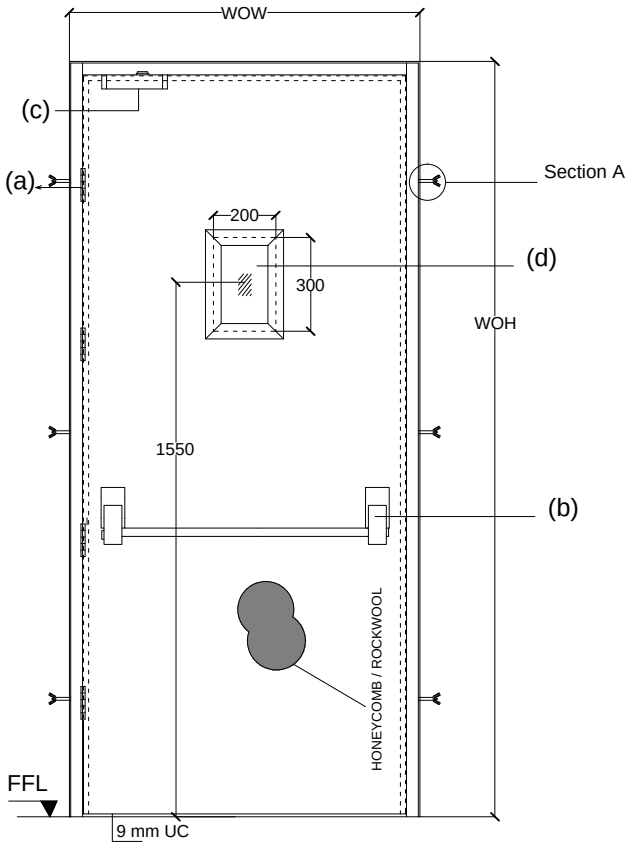

ELEVATION

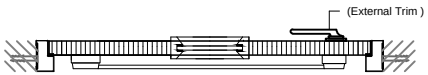

Top View

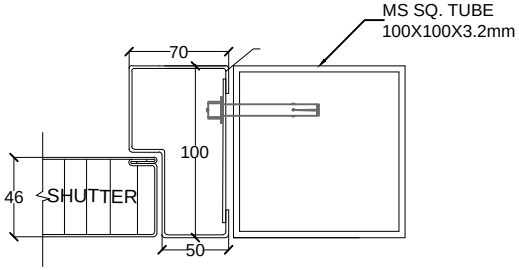

ASSESORIES DETALES

(a) HINGES: SS hinges 100x75x3mm

(b) LOCK : Panic Bar-Dorma single point latching PHA2000
Outer trim-Dorma for panic without cylinder PHT03

(c) DOOR CLOSER : TS68

(d) VISION PANEL- 5mm THK. FIRE GLASS SIZE- 200X300mm.

Shutter thickness : 46 mm
Frame Sheet thick : 1.5 mm
Shutter sheet thick : 1.2 mm
Fixing : On MS STRUCTURE OF MS SQ. TUBE 100X100X3.2mm WITH BOLT

NOTE:- *All Dimensions are in mm.
*Tolerance:-All Linear Dimensions ±3mm,Others ±0.5mm.
*The Drawing Is For Location of Hardware only. Drawing Does Not Represent The Hardware For More Clarity, Please Go Through Hardware Broucher.

Fire door size

WOW	WOH	TYPE 1	TYPE 2	TYPE 3	TYPE 4	QUANTITY
900	2100			2		2

COLOR OF DOOR- RAL 3002 CARMINE RED

REV NO	DATE	DESCRIPTION
REV -0	18/11/17	INITIAL DRAWING
REV -1	25/11/17	COLOR OF DOOR REVISED FROM RAL 9010 TO RAL 3002.

This drawing & designing is the property of NIHVA TECHNOLOGIES. Not to be sold or copied to any other concern.

TITLE: SINGLE LEAF FIRE RATED DOORS

	SIGN	DATE
DRAWN	OMKAR	18/11/17
CHECK	SHEKHAR	18/11/17
APPROVAL	SHEKHAR	18/11/17

If any queries contact : design@nihva.com

ALL DIMENSION ARE IN mm

NIHVA TECHNOLOGIES PVT. LTD.
NIHVA TECHNOLOGIES PVT. LTD. PUNE
Tel : 020 66304033
Email:- info@nihva.com
Website:- www.nihva.com

CLIENT -
PROJECT -
SITE -
DWG. NO. : NIHVA/17-18/VDR/0179/R01 | REV- 1
SCALE: NTS | WT: | SHEET: 01 OF 01