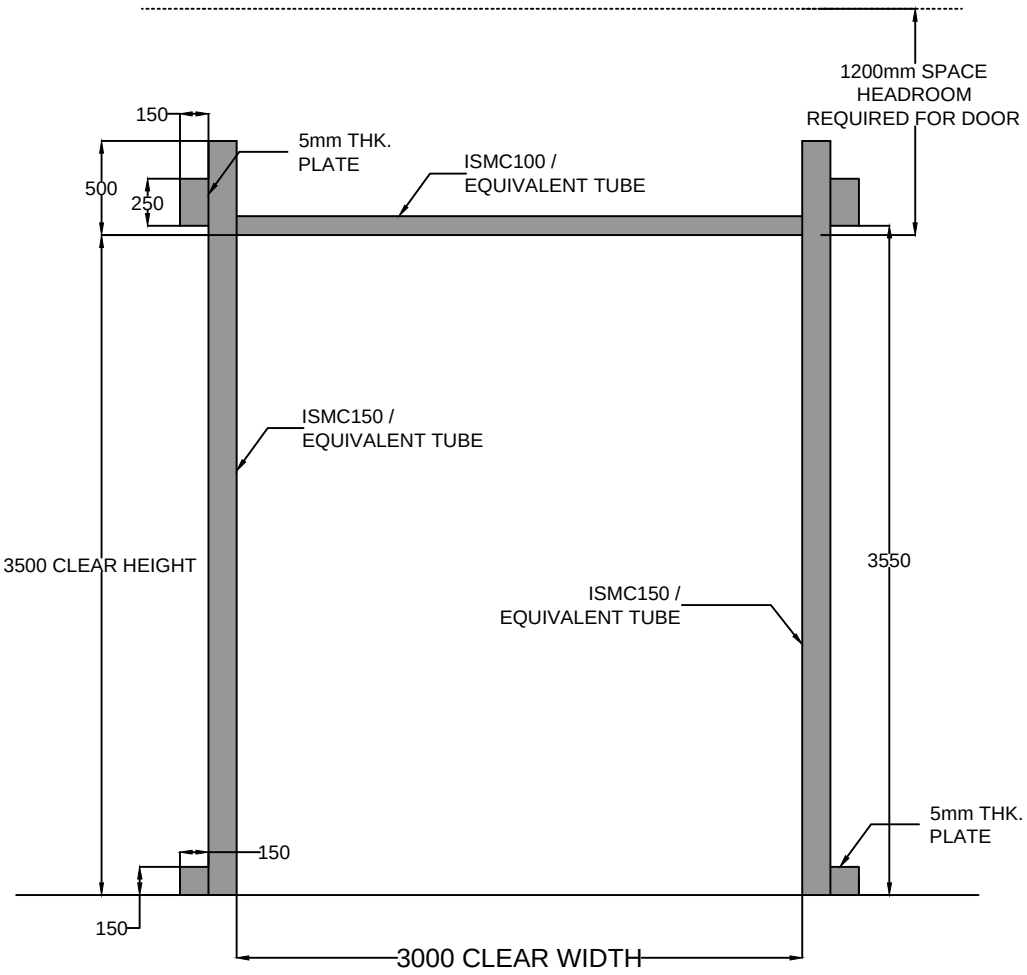

MS STRUCTURE FOR RR 3000 ISO

This drawing & design is the property of NIHVA TECHNOLOGIES. Not to be sold or copied to any other concern.

TITLE

STRUCTURE FOR RR3000 ISO

CLIENT APPROVAL

ALL DIMENSION ARE IN mm

NIHVA TECHNOLOGIES PVT. LTD. PUNE
Tel : 020 66304033
Email:- info@nihva.com
Website:- www.nihva.com

	SIGN	DATE	
DRAWN	SURAJ	22/09/17	CLIENT -FERRERO INDIA PVT. LTD.
CHECK	SHEKHAR	22/09/17	PROJECT -
REV.			SITE -BARAMATI.
APPRD.	SHEKHAR	22/09/17	DWG. NO. -NIHVA/17-18/0211
MFG			SCALE: NTS | WT: | SHEET: 01 OF 01
Ref. No.			If any queries contact : projects@nihva.com