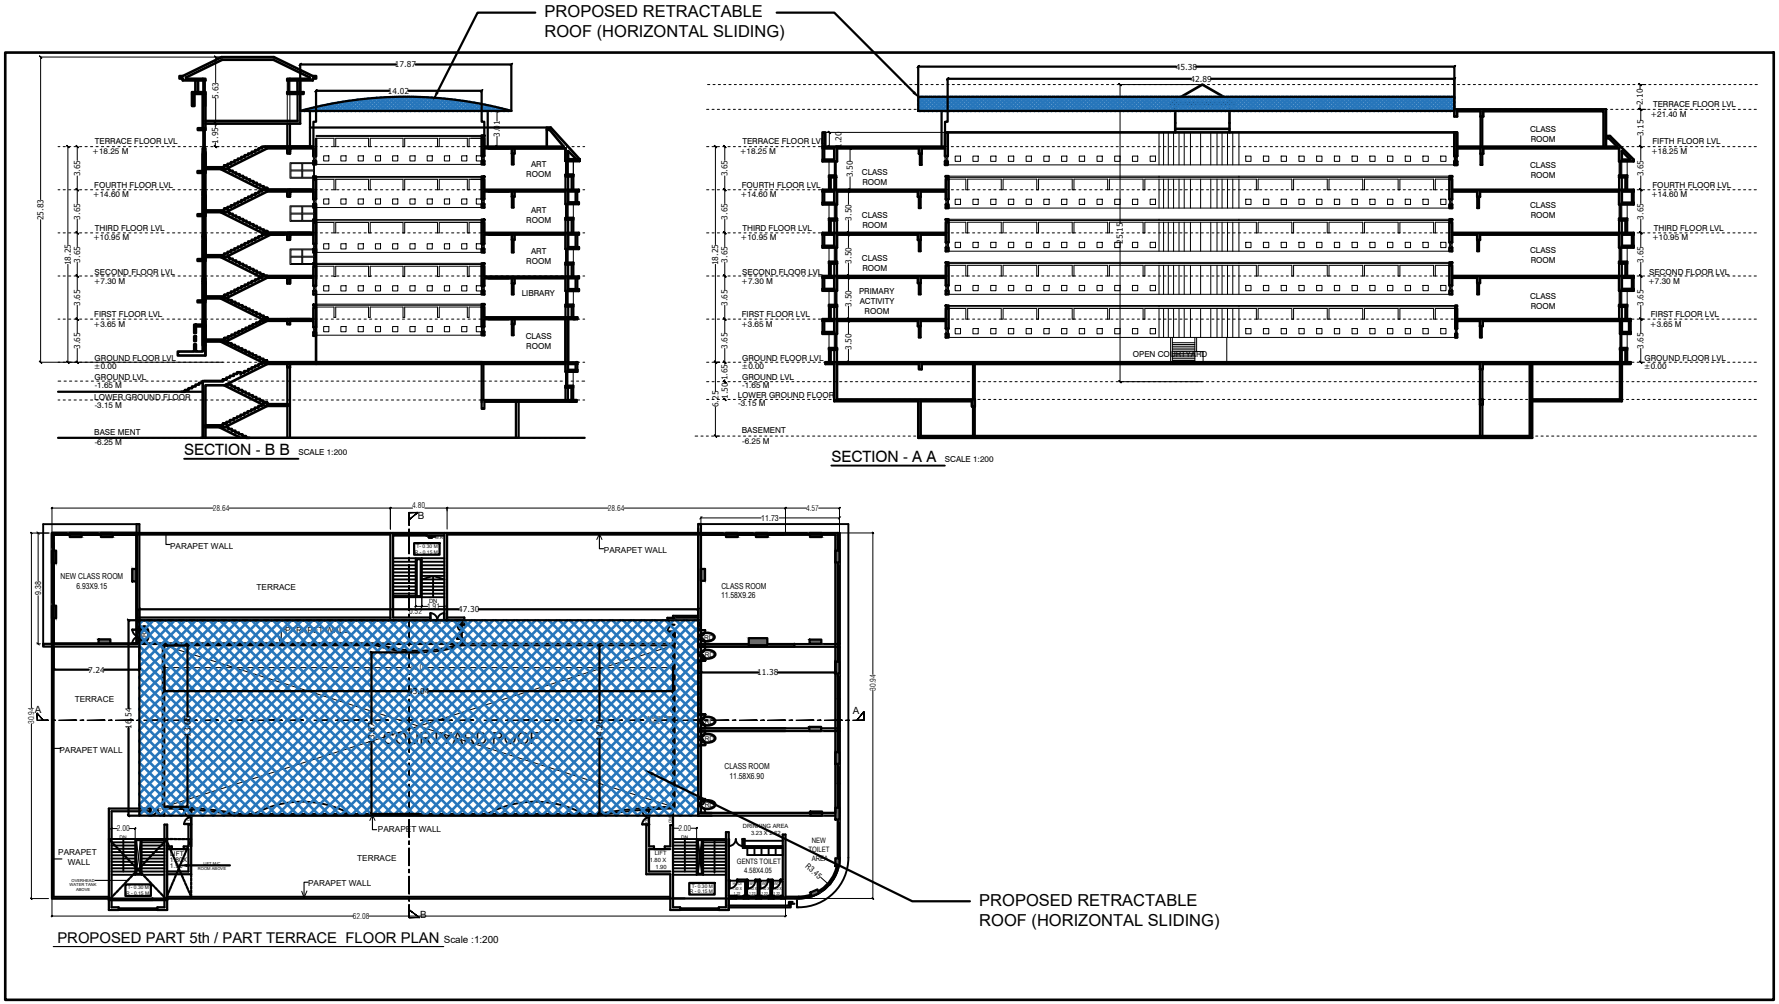

PROPOSED RETRACTABLE
ROOF (HORIZONTAL SLIDING)
TERRACE FLOOR LVL +16.25 M
FOURTH FLOOR LVL +14.60 M
THIRD FLOOR LVL +10.95 M
SECOND FLOOR LVL +7.30 M
FIRST FLOOR LVL +3.65 M
GROUND FLOOR LVL ±0.00
GROUND LVL -1.65 M
LOWER GROUND FLOOR -3.15 M
BASE MENT -6.25 M
ART ROOM
ART ROOM
ART ROOM
LIBRARY
CLASS ROOM
SECTION - B B SCALE 1:200
TERRACE FLOOR LVL +21.40 M
FIFTH FLOOR LVL +18.25 M
FOURTH FLOOR LVL +14.60 M
THIRD FLOOR LVL +10.95 M
SECOND FLOOR LVL +7.30 M
FIRST FLOOR LVL +3.65 M
GROUND FLOOR LVL ±0.00
GROUND LVL -1.65 M
LOWER GROUND FLOOR -3.15 M
BASEMENT -6.25 M
CLASS ROOM
PRIMARY ACTIVITY ROOM
OPEN COURTYARD
SECTION - A A SCALE 1:200
PARAPET WALL
TERRACE
NEW CLASS ROOM 6.93X9.15
CLASS ROOM 11.58X9.26
COURTYARD ROOF
CLASS ROOM 11.58X6.90
GENTS TOILET 4.58X4.05
NEW TOILET BLOCK
PROPOSED PART 5th / PART TERRACE FLOOR PLAN Scale :1:200
PROPOSED RETRACTABLE
ROOF (HORIZONTAL SLIDING)