




Client scope
*Civil foundation need to be done for tracks approx.500mm *Bollards need to shift forward *Roof need to be shift at top approx.300mm

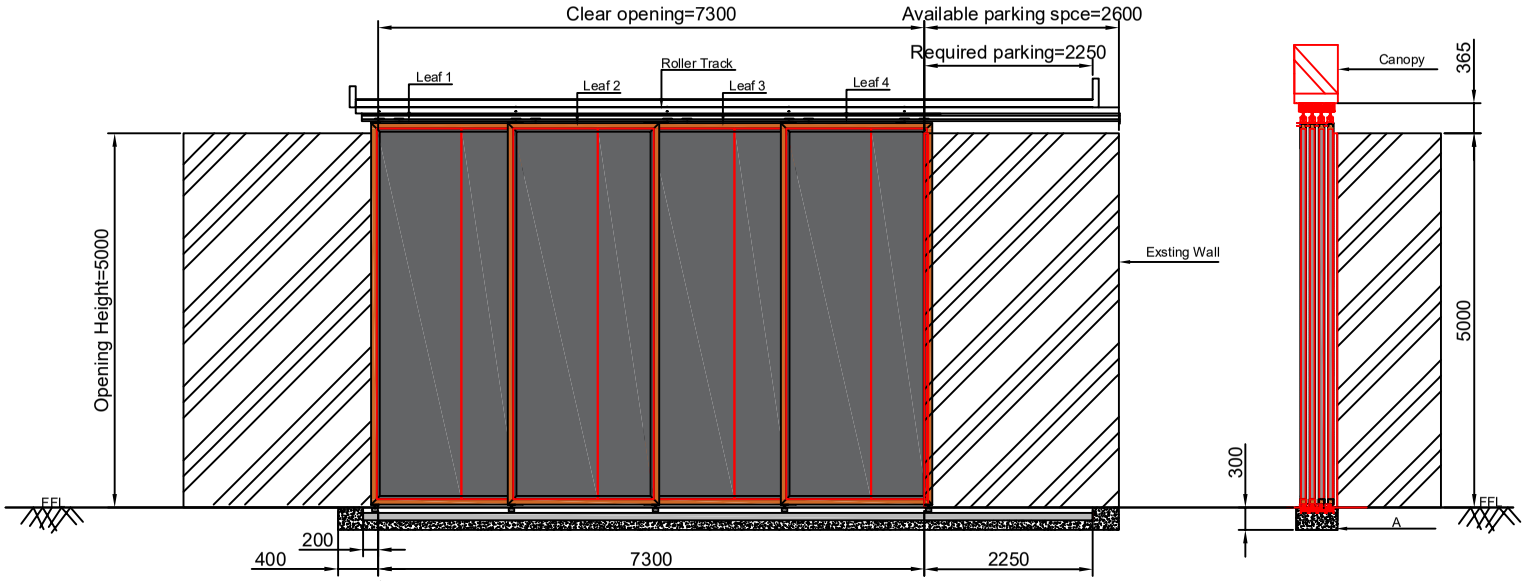

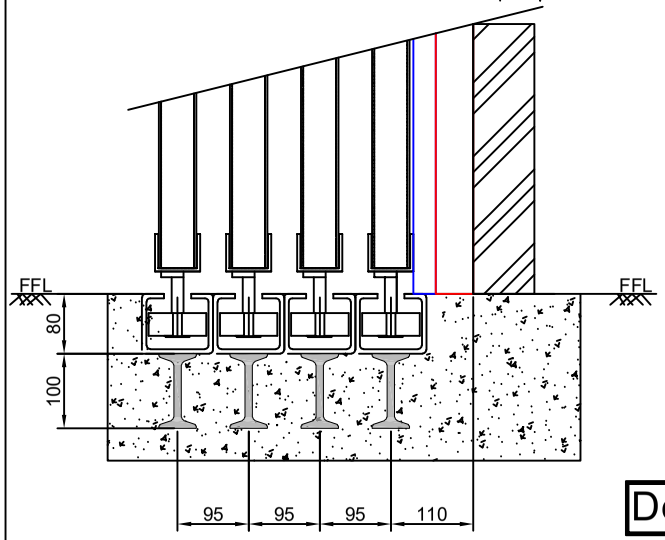

Deatil A

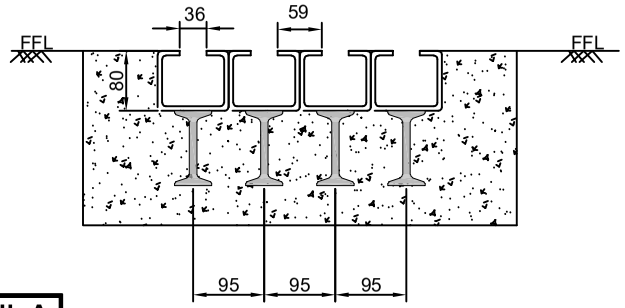

Note:--

1. All dimension are in MM
2. All Civil work will be in client scope
3. Manufacturing,civil and installation tolerance will be ±10mm
4. Top and Bottom track should be in parallal within ±3mm

This drawing & design is the property of NIHVA TECHNOLOGIES. Not to be sold or copied to any other concern.

TITLE:- 4 LEAF RIGHT SIDE CRM DOOR 01

NIHVA TECHNOLOGIES PVT. LTD.
NIHVA TECHNOLOGIES PVT. LTD. PUNE
Tel : 020 66304033
Email:- info@nihva.com
Website:- www.nihva.com

	NAME	DATE	SIGN
DRAWN	SUJATA	26/04/2022	
CHECK	M.SUTAR	26/04/2022	
APPRD.	V.TARAK	26/04/2022	

CLIENT - LESTECH
LOCATION - POSCO MANGAON
PRODUCT - SLIDING DOOR
If any queries contact : design@nihva.com
DWG NO:-NIHVA/22-23/CLT/0014 REV- 0
ALL DIMENSION ARE IN mm
SCALE: NTS SCALE:-- 1:1 SHEET: 01 OF 01

Rev No.	Revision	Date	Revised By