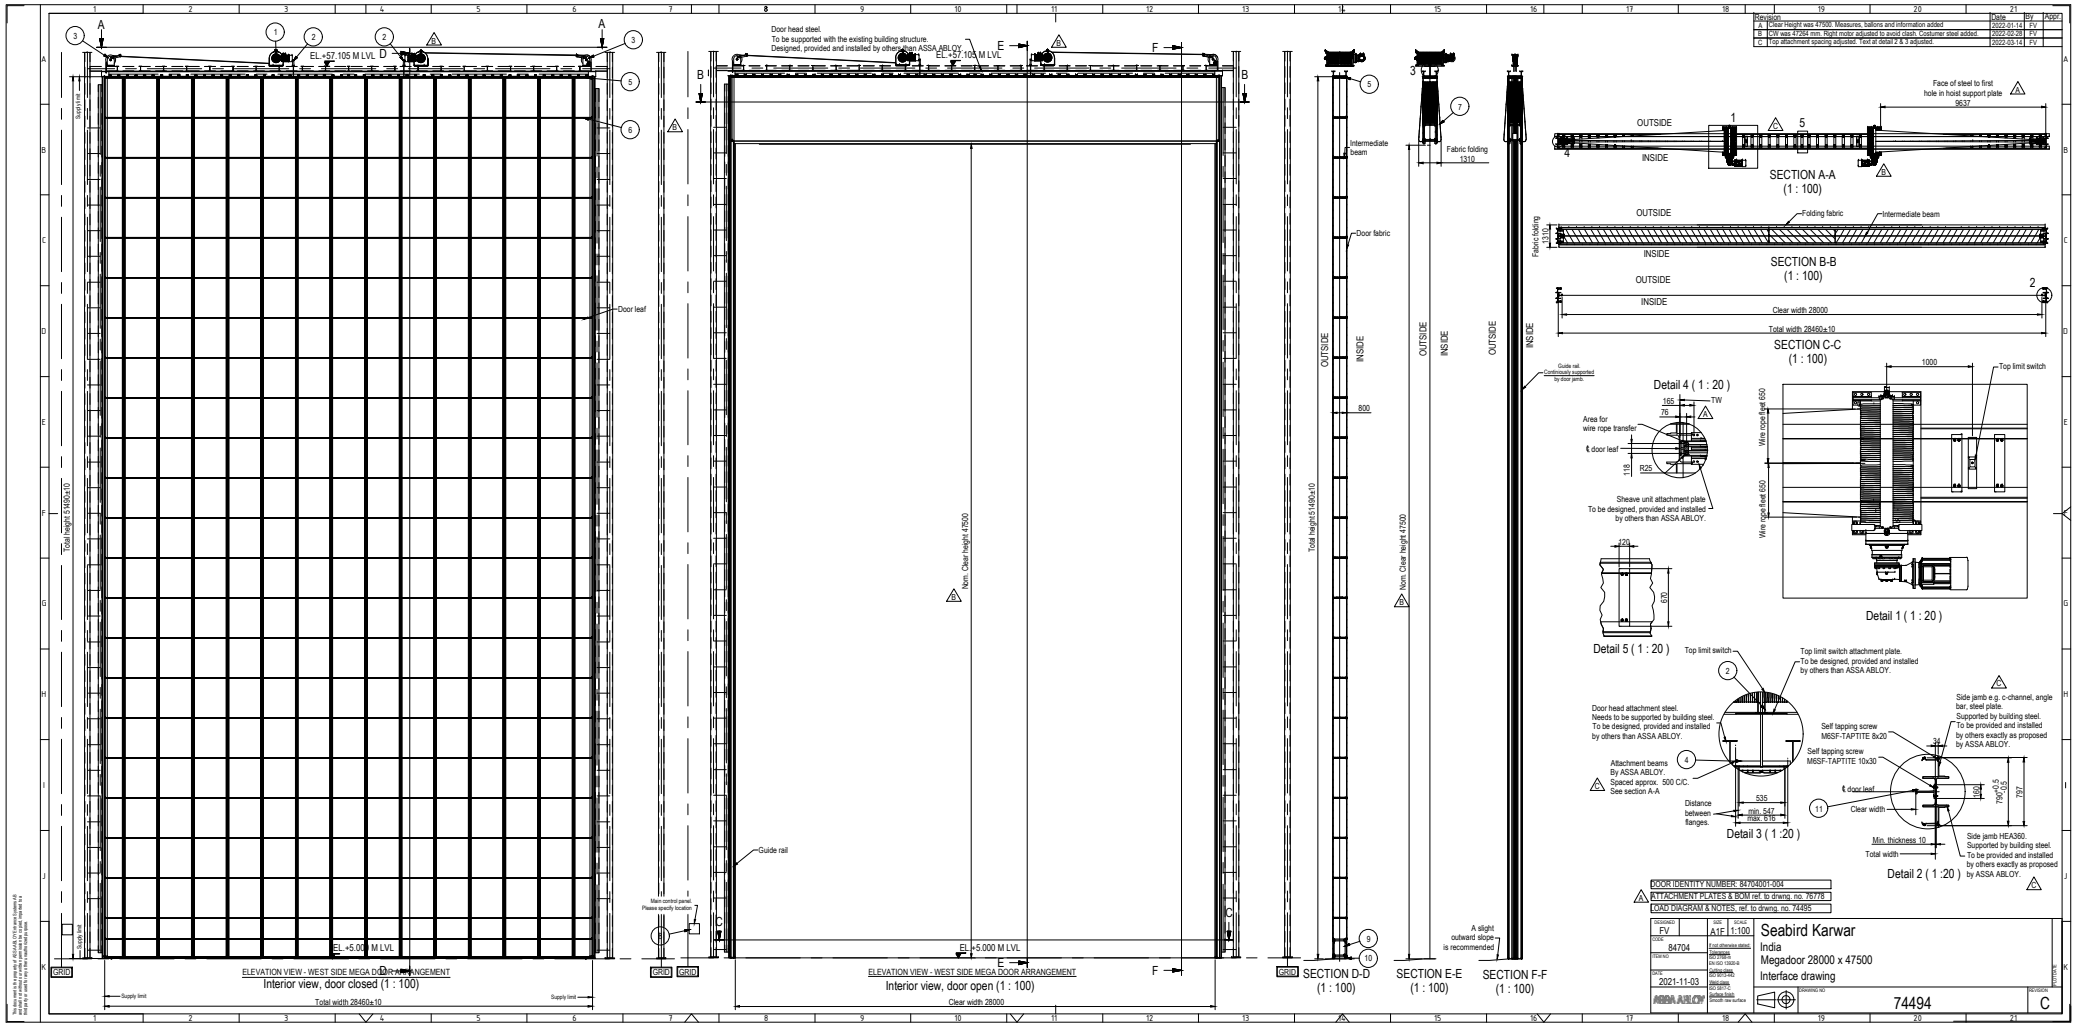

Revision
A Clear Height was 47500. Measures, ballons and information added 2022-01-14 FV
B C/W was 47254 mm. Right motor adjusted to avoid clash. Costumer steel added. 2022-02-28 FV
C Top attachment spacing adjusted. Text at detail 2 & 3 adjusted. 2022-03-14 FV
EL. +57.105 M LVL
EL. +5.000 M LVL
Door head steel.
To be supported with the existing building structure.
Designed, provided and installed by others than ASSA ABLOY.
Total height 51490±10
Nom. Clear height 47500
Door leaf
Door fabric
Guide rail
Intermediate beam
Fabric folding 1310
Main control panel.
Please specify location
Supply limit
Total width 28460±10
Clear width 28000
ELEVATION VIEW - WEST SIDE MEGA DOOR ARRANGEMENT
Interior view, door closed (1 : 100)
ELEVATION VIEW - WEST SIDE MEGA DOOR ARRANGEMENT
Interior view, door open (1 : 100)
SECTION D-D (1 : 100)
SECTION E-E (1 : 100)
SECTION F-F (1 : 100)
A slight outward slope is recommended
SECTION A-A (1 : 100)
Face of steel to first hole in hoist support plate
9637
SECTION B-B (1 : 100)
Folding fabric
SECTION C-C (1 : 100)
Clear width 28000
Total width 28460±10
Detail 1 (1 : 20)
Top limit switch
Wire rope fleet 650
Detail 4 (1 : 20)
Area for wire rope transfer
Sheave unit attachment plate
To be designed, provided and installed by others than ASSA ABLOY.
Detail 5 (1 : 20)
Detail 3 (1 :20)
Top limit switch attachment plate.
To be designed, provided and installed by others than ASSA ABLOY.
Door head attachment steel.
Needs to be supported by building steel.
To be designed, provided and installed by others than ASSA ABLOY.
Attachment beams
By ASSA ABLOY.
Spaced approx. 500 C/C.
See section A-A
Self tapping screw M6SF-TAPTITE 8x20
Self tapping screw M6SF-TAPTITE 10x30
Distance between flanges.
Side jamb e.g. c-channel, angle bar, steel plate.
Supported by building steel.
To be provided and installed by others exactly as proposed by ASSA ABLOY.
Side jamb HEA360.
Supported by building steel.
To be provided and installed by others exactly as proposed by ASSA ABLOY.
Min. thickness 10
Detail 2 (1 :20)
DOOR IDENTITY NUMBER: 84704001-004
ATTACHMENT PLATES & BOM ref. to drwng. no. 76778
CIND DIAGRAM & NOTES. ref to drwng. no. 74495
DESIGNED FV
SIZE A1F
SCALE 1:100
CODE 84704
ITEM NO
DATE 2021-11-03
ASSA ABLOY
Seabird Karwar
India
Megadoor 28000 x 47500
Interface drawing
DRAWING NO 74494
REVISION C