
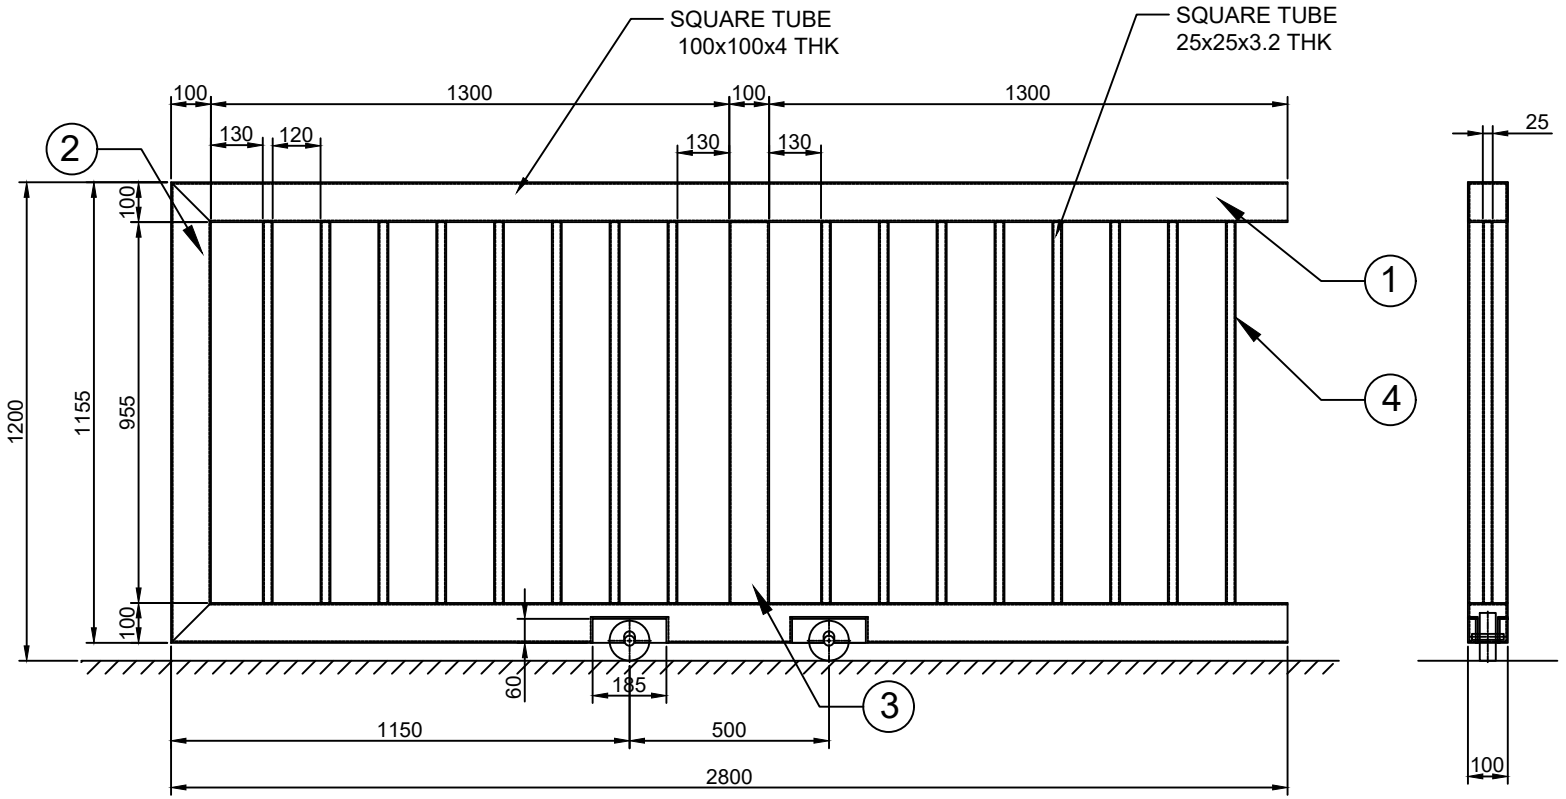


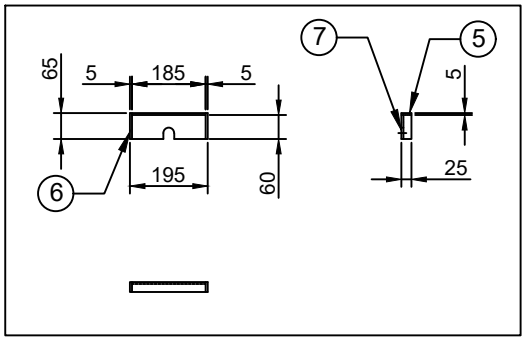

BOM				
SL NO.	DESCRIPTION	SPECIFICATION	QTY	WEIGHT
1	MS SQ. TUBE	100 X100 X 4 X 2800 L	2 NOS	66.32
2	MS SQ. TUBE	100 X 100 X 4 X1155 L	1 NO	13.68
3	MS SQ. TUBE	100 X 100 X 4 X 955 L	1 NO	11.31
4	MS SQ. TUBE	25X25X3.2X955L	16 NOS	31.36
5	MS FLAT	25X5X185L	4 NOS	0.73
6	MS FLAT	25X5X65	8 NOS	0.51
7	MS FLAT	60X5X185	4 NOS	1.74
	TOTAL			123.4000

This drawing & design is the property of NIHVA TECHNOLOGIES. Not to be sold or copied to any other concern.

TITLE:- GATE MODIFICATION

NIHVA TECHNOLOGIES PVT. LTD. PUNE
Tel : 020 66304033
Email:- info@nihva.com
Website:- www.nihva.com

	NAME	DATE	SIGN
DRAWN	NIRMALA	02/06/2023	
CHECK	A.K.	02/06/2023	
APPRD.	V.T.	02/06/2023	

CLIENT - IKEA
LOCATION - MUMBAI
PRODUCT - SLIDING GATE | QTY- 1
If any queries contact : design1@nihva.com | DWG NO:- NIHVA/23-24/MFG /0131 | REV-00
ALL DIMENSION ARE IN mm | SCALE: NTS | SCALE:-- 1:1 | SHEET: 01 OF 01

Rev No.	Revision	Date	Revised By