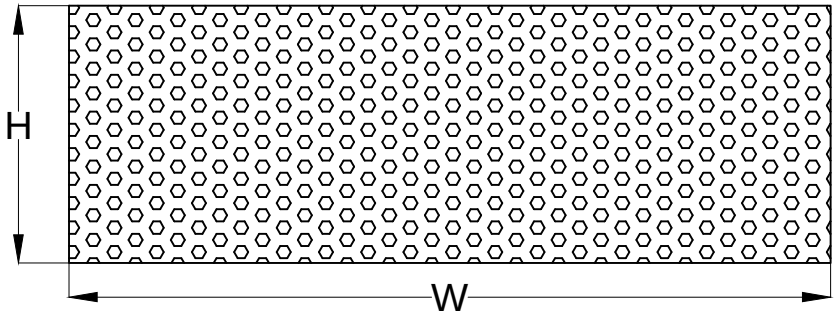

F.V

S.V

T.V

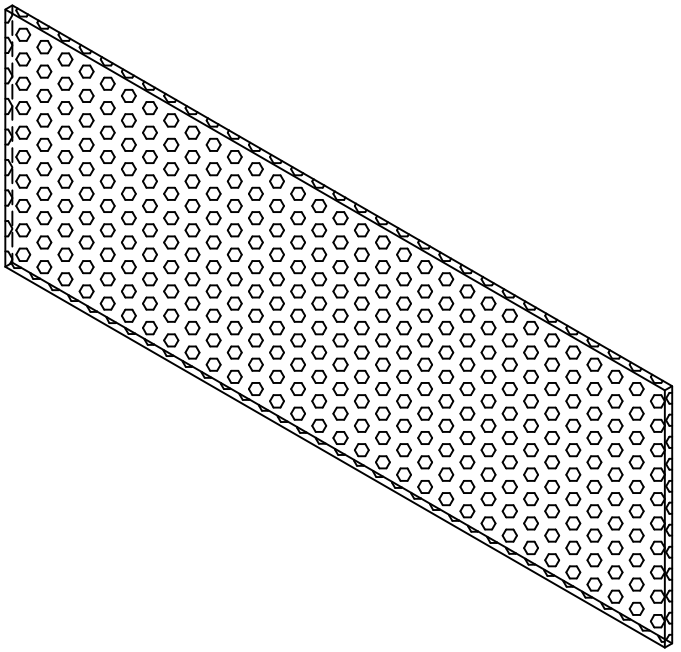

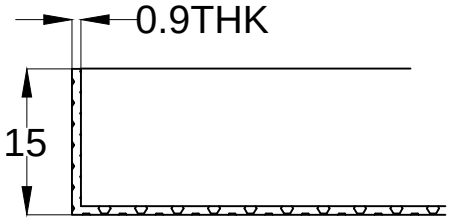

DETAIL VIEW 'A'.
(BENDING VIEW)

SR NO	SIZE	QTY	MATERIAL
1	1435mmX456mmX0.9mm	09 NOS	MILD STEEL
2	1441mmX456mmX0.9mm	01 NO	MILD STEEL

SR NO	SPECIFICATION		MATERIAL
1	MS SHHET 0.9THK	INNER SHEET	MILD STEEL

This drawing & designing is the property of NIHVA TECHNOLOGIES. Not to be sold or copied to any other concern.

TITLE
SLIDING GATE SHEET DRAWING

	Name	SIGN	DATE
DRAWN	SURAJ		05/12/18
CHECK	PRADEEP		05/12/18
APPROVAL	R.D		05/12/18

If any queries contact : design@nihva.com

ALL DIMENSION ARE IN mm

NIHVA
NIHVA TECHNOLOGIES PVT. LTD.
NIHVA TECHNOLOGIES PVT. LTD. PUNE
Tel : 020 66304033
Website:- www.nihva.com
Email:- info@nihva.com

CLIENT -

PROJECT -

SITE LOCATION -MODINAGAR,UTTAR PRADESH.

DWG. NO. : NIHVA/18-19/VDR/249 REV.:- 0

SCALE: NTS WT: SHEET: 01 OF 01