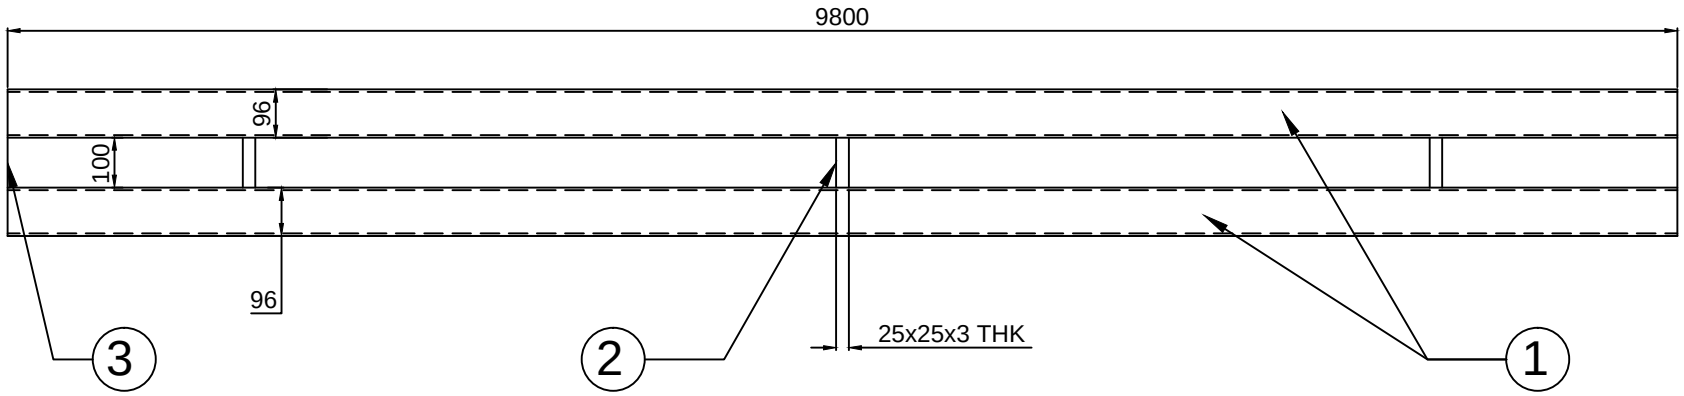

SR NO	DESCRIPTION	SPECIFICATION	QTY
3	MS FLAT	50 X 10 X 300L	4 NOS
2	SQ. TUBE	38 X 38 X 4 THK X 100L	6 NOS
1	R. TUBE	96 X 48 X 4.8 THK X L	NOS

This drawing & design is the property of NIHVA TECHNOLOGIES. Not to be sold or copied to any other concern.

TITLE

STRUCTURE BEAM

	NAME	SIGN	DATE
DRAWN	P.A		11.12.19
CHECK	G.J		11.12.19
APPRD.			

If any queries contact : design@nihva.com

ALL DIMENSION ARE IN mm

NIHVA TECHNOLOGIES PVT. LTD.

NIHVA TECHNOLOGIES PVT. LTD. PUNE
Tel : 020 66304033
Email:- info@nihva.com
Website:- www.nihva.com

CLIENT -

PROJECT -

SITE LOCATION -

DWG. NO. : NIHVA/19-20/VDR/244

SCALE: NTS | WT: | REV- 00