
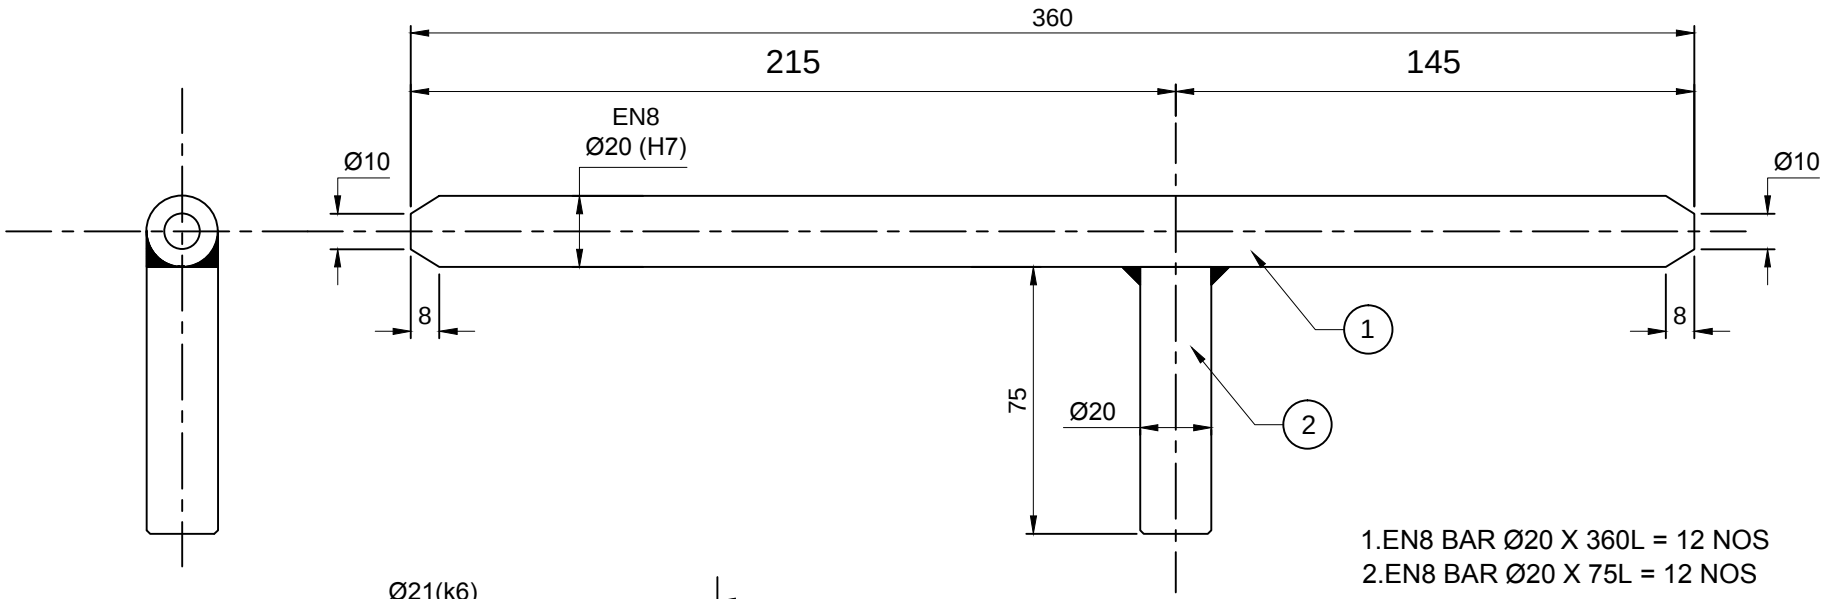


1.EN8 BAR Ø20 X 360L = 12 NOS
2.EN8 BAR Ø20 X 75L = 12 NOS

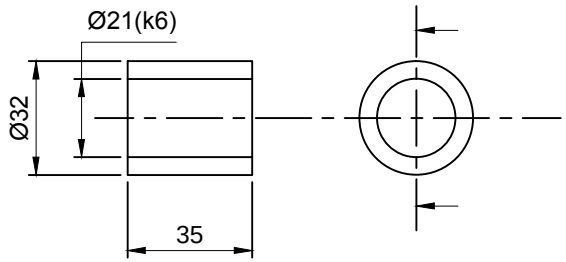

3. M.S BUSH
OD32 X ID22 X 35L = 36 NOS

This drawing & design is the property of NIHVA TECHNOLOGIES. Not to be sold or copied to any other concern.

TITLE	TOWER BOLT			NIHVA TECHNOLOGIES PVT. LTD. PUNE
	NAME	SIGN	DATE	NIHVA TECHNOLOGIES PVT. LTD. Website:- www.nihva.com
DRAWN	P.A		21.02.2020	Tel : 020 66304033 Email:- info@nihva.com
CHECK	G.J		21.02.2020	CLIENT -
APPRD.				PROJECT -
				SITE LOCATION -

If any queries contact : design@nihva.com	DWG. NO. : NIHVA/19-20/VDR/326	REV- R00
ALL DIMENSION ARE IN mm	SCALE: NTS WT:	SHEET: 01 OF 01