
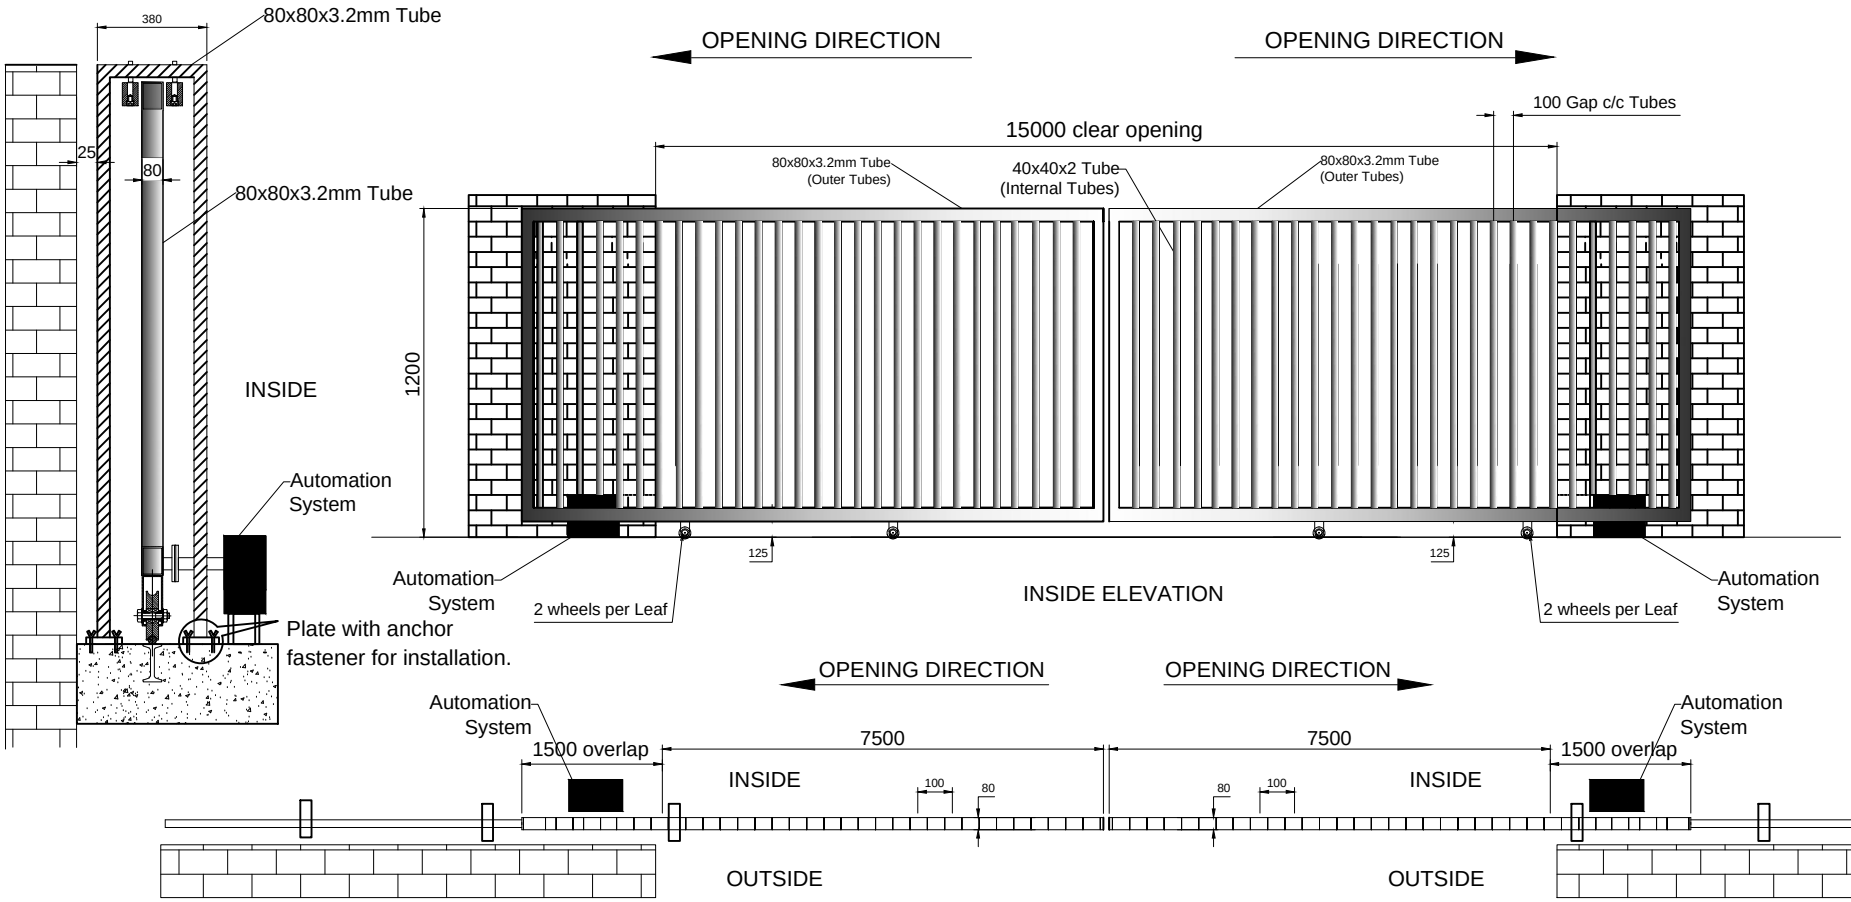


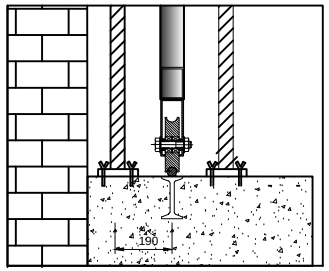

Clear Opening size -15000mm x 1200mm
Total No. of Leaf - 2 Leaf
NOTE :- *ALL REQ. CIVIL WORK WILL BE IN CLIENT SCOPE.

DOUBLE LEAF SLIDING GATE

This drawing & designing is the property of NIHVA TECHNOLOGIES. Not be sold or copy to any other concern.

TITLE: DOUBLE LEAF MOTORISED SLIDING GATE	NIHVA TECHNOLOGIES PVT. LTD.	NIHVA TECHNOLOGY PVT. LTD. PUNE Tel : 020 66304033 Email:- info@nihva.com Website:- www.nihva.com

	SIGN	DATE	
DRAWN	OMKAR	27/02/16	CLIENT - HYOSUNG T&D
CHECK	ANIL	27/02/16	PROJECT -
REV.	01		SITE -
APPROVAL			DWG. NO. : NIHVA/15-16/226

If any queries contact : projects@nihva.com

ALL DIMENSION ARE IN mm

SCALE: 01 | WT: | SHEET: 01 OF 01